


COLUMN LAY-OUT PLAN

30 x 18 M | 557 M2 | 4 BAYS | SLOPE 1:10 | C.H = 10,670 | SINGLE SLOPE - COLUMNS BOTH SIDES

FSW - FAR SIDE WALL

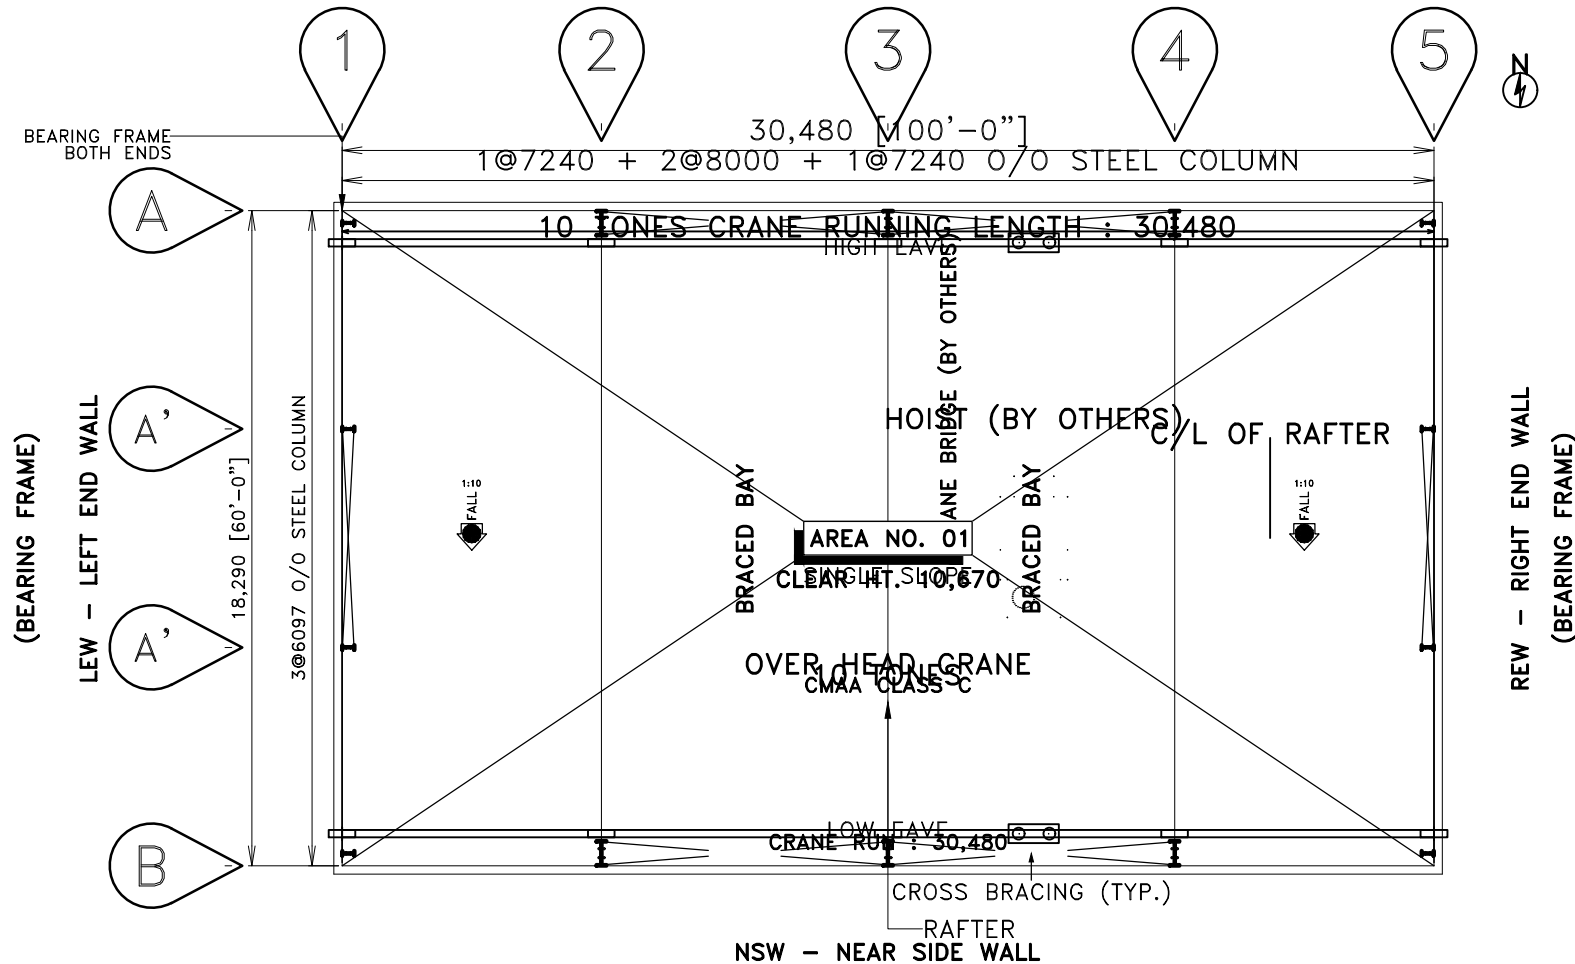

GENERAL NOTES

1. ALL DIMENSIONS ARE IN MM.
2. PROPOSAL DRAWING - NOT FOR CONSTRUCTION.
3. PROPOSAL DRAWING IS INDICATIVE ONLY; FINAL DIMENSIONS & LEVELS WILL BE SHOWN IN THE APPROVAL DRAWING AT THE DESIGN STAGE.
4. FOR DETAILED DESCRIPTION, REFER TO THE TECHNICAL & FINANCIAL PROPOSAL.

THIS DOCUMENT IS A PROPOSAL DRAWING OF
MAIMAAR STEEL (PVT) LTD - NOT FOR CONSTRUCTION

THE BUILDING HAS BEEN DESIGNED TO
SUPPORT IT'S OWN DEAD LOAD PLUS:

LIVE LOAD ON ROOF 0.57 KN/SQ.M.
LIVE LOAD ON FRAME 0.57 KN/SQ.M.
WIND SPEED (3-SEC GUST) 130 KPH
EXPOSURE CATEGORY B
ADD'L. COLLATERAL LOAD 0
ROOF SNOW LOAD -
SEISMIC LOAD ZONE 2B
TEMPERATURE LOAD -
RAINFALL INTENSITY 150 MM/HR

AS PER MBMA 2006 METAL BUILDING SYSTEMS
MANUAL

00	05-SEP-2026		M.H	YEA
REV. NO.	DATE	DSN	DRN	CHK

PROJECT NAME :
UNNAMED PROJECT

CUSTOMER :
UNNAMED CLIENT

STEEL CONTRACTOR :



MAIMAAR STEEL (PVT) LTD

LAHORE OFFICE
235, FIRST FLOOR, LALAZAR COMMERCIAL AREA,
RAIWIND ROAD, LAHORE, PAKISTAN
WEB: WWW.MAIMAARGROUP.COM
CELL : +(92-300) 807 4007

QUOTE NO. : MSPL-26-276

BLDG. NO. : 01

BLDG. NAME. :

NO. OF IDENTICAL BLDG. : 1


DRAWING TITLE :
COLUMN LAYOUT PLAN

SCALE 1:214	SHEET SIZE A4	SHEET NO. PRO-01
----------------	------------------	---------------------

18.3M SPAN | C.H 10.7M | HIGH EAVE 13.4M | SLOPE 1:10

ROOF SHEETING:

1. CEMENT MORTAR (S-TYPE) + 50MM FIBERGLASS INSULATION (12KG/M3)

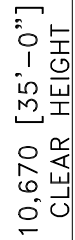

1. ALL DIMENSIONS ARE IN MM.
2. PROPOSAL DRAWING – NOT FOR CONSTRUCTION.
3. PROPOSAL DRAWING IS INDICATIVE ONLY; FINAL DIMENSIONS & LEVELS WILL BE SHOWN IN THE APPROVAL DRAWING AT THE DESIGN STAGE.
4. FOR DETAILED DESCRIPTION, REFER TO THE TECHNICAL & FINANCIAL PROPOSAL.

KEY BUILDING DATA

HEIGHTS, SLOPE & GRIDS AS SHOWN ON THE SECTION.

PROJECT NAME :
UNNAMED PROJECT

CUSTOMER : UNNAMED CLIENT



LAHORE OFFICE
238, FIRST FLOOR, LALAZAR COMMERCIAL AREA,
RAIWIND ROAD, LAHORE, PAKISTAN
WEB: WWW.MAIMAARGROUP.COM
CELL : +(92-300) 807 4007

NO. OF IDENTICAL BLDG.	: 1
------------------------	-----

SCALE 1:209	SHEET SIZE A4	SHEET NO. PRO-02
----------------	------------------	---------------------