

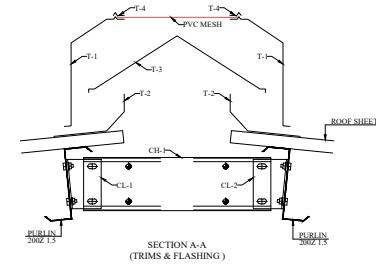
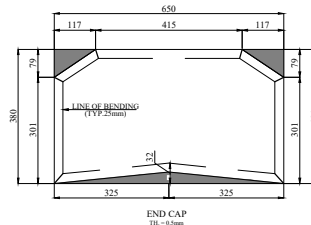
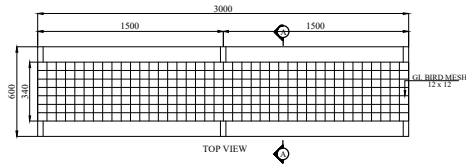
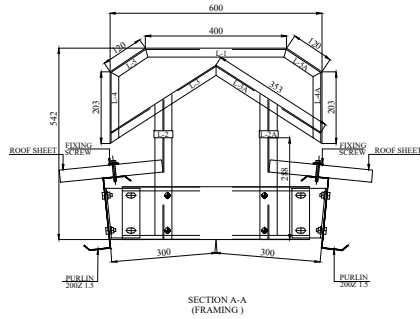
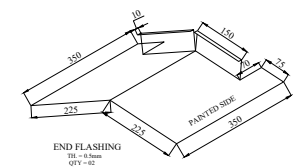
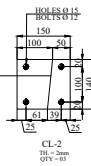
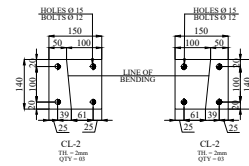
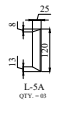
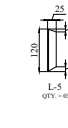
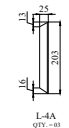
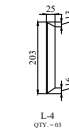
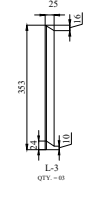
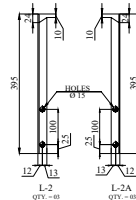
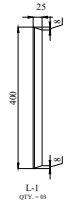
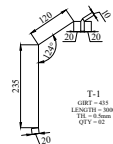
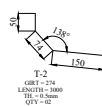


NOTE: ALL ANGLE IRON ARE 25x25x3mm Th.

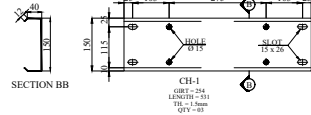

MATERIAL LIST OF HARDWARE			
S.NO.	MARK	LENGTH	QTY.
1	MSB	12 x 35	36
2	SCREW	5.5 x 25	100

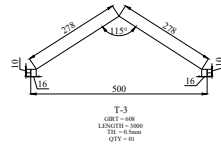

- NOTES:
1. THE QUANTITIES FOR EACH ITEM MENTIONED IN THIS DRAWING ARE 01 NO. VENTILATOR.
 2. QUANTITY OF IDENTICAL VENTILATOR = 11 NO.

RIDGE VENTILATOR DETAILS

FOR APPROVAL :

IN ORDER TO SCHEDULE THIS PROJECT IN AN EFFICIENT MANNER , KINDLY RETURN THESE DRAWINGS WITH YOUR ANY CHANGES MADE AFTER THE COMMENTS MARKED IN RED

APPROVAL OF THESE DRAWINGS MAY DELAY THE FABRICATION SCHEDULE AND SUBSEQUENTLY THE DELIVERY OF THE BUILDING.

PLEASE TICK MARK ONLY ONE OF THE FOLLOWING

- ☐ " APPROVED AS IS "
- ☐ " APPROVED AS NOTED "
- ☐ " RESUBMIT AS NOTED "

APPROVE : _____

SIGNATURE: _____

DATE : _____

REV	DATE	DESCRIPTION	DRAWN BY	CHK BY	APR BY
00	10/04/2025	ISSUED FOR APPROVAL	M.A	S.R	NAS



MAIMAAR STEEL Pvt.Ltd
238, Raiwind Road, Thokar Niaz Baig, Lahore, Pakistan
E-mail: nasir.abbas@maimaargroup.com
E-mail: maimaar.steel@gmail.com
Website: www.maimaargroup.com
E-mail: info@maimaargroup.com
Mob-I : +(92-300) 807 4017 ,+(92-333) 807 1115

JOB NO./QUOTE NO.	MSPL-203	BUILDING #	01
PROJECT NAME	WAREHOUSE		
CUSTOMER	DHL		
JOB SITE LOCATION	RAWAT		

RIDGE VENTILATOR DETAILS			DWG NO.
			20