


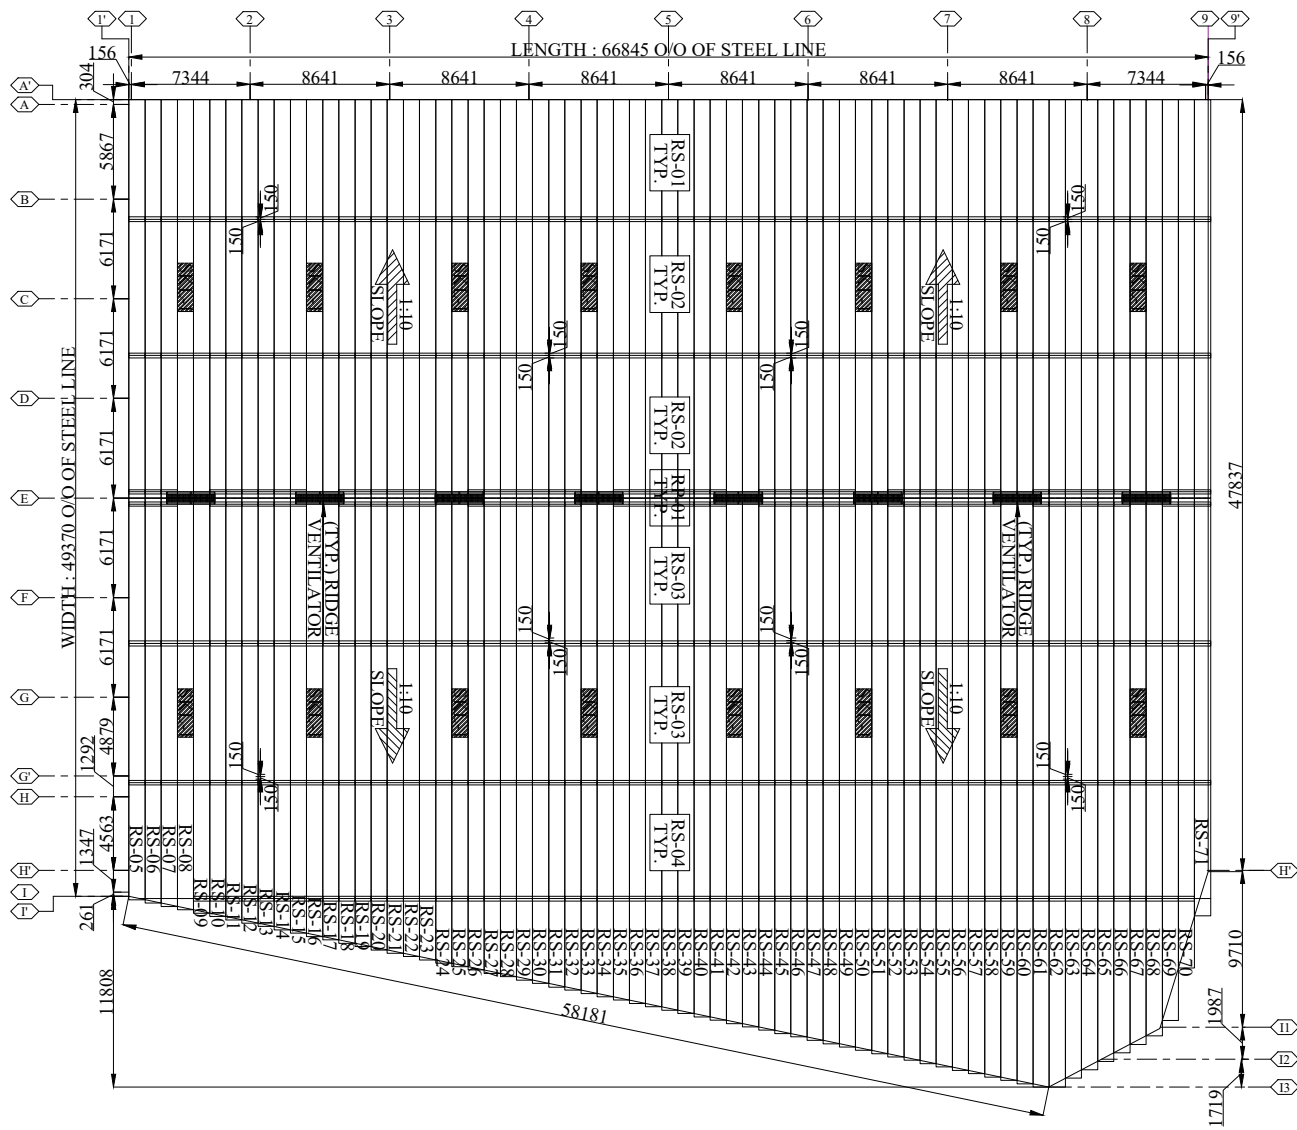

ROOF SHEETS TABLE				
DESCRIPTIONS	PART	LENGTH (MM)	WIDTH (MM)	QUANTITY
ROOF SHEET	RS-01	7,569	1,000	67
ROOF SHEET	RS-02	8,738	1,000	134
ROOF SHEET	RS-03	8,911	1,000	134
ROOF SHEET	RS-04	7,477	1,000	62
ROOF SHEET	RS-05	7,399	1,000	1
ROOF SHEET	RS-06	7,606	1,000	1
ROOF SHEET	RS-07	7,813	1,000	1
ROOF SHEET	RS-08	8,020	1,000	1
ROOF SHEET	RS-09	1,051	1,000	1
ROOF SHEET	RS-10	1,258	1,000	1
ROOF SHEET	RS-11	1,466	1,000	1
ROOF SHEET	RS-12	1,673	1,000	1
ROOF SHEET	RS-13	1,880	1,000	1
ROOF SHEET	RS-14	2,087	1,000	1
ROOF SHEET	RS-15	2,295	1,000	1
ROOF SHEET	RS-16	2,502	1,000	1
ROOF SHEET	RS-17	2,709	1,000	1
ROOF SHEET	RS-18	2,917	1,000	1
ROOF SHEET	RS-19	3,124	1,000	1
ROOF SHEET	RS-20	3,331	1,000	1
ROOF SHEET	RS-21	3,538	1,000	1
ROOF SHEET	RS-22	3,738	1,000	1
ROOF SHEET	RS-23	3,953	1,000	1
ROOF SHEET	RS-24	4,160	1,000	1
ROOF SHEET	RS-25	4,367	1,000	1
ROOF SHEET	RS-26	4,575	1,000	1
ROOF SHEET	RS-27	4,782	1,000	1
ROOF SHEET	RS-28	4,989	1,000	1
ROOF SHEET	RS-29	5,202	1,000	1
ROOF SHEET	RS-30	5,407	1,000	1
ROOF SHEET	RS-31	5,631	1,000	1
ROOF SHEET	RS-32	5,823	1,000	1
ROOF SHEET	RS-33	6,031	1,000	1

ROOF SHEETS TABLE				
DESCRIPTIONS	PART	LENGTH (MM)	WIDTH (MM)	QUANTITY
ROOF SHEET	RS-34	6,239	1,000	1
ROOF SHEET	RS-35	6,439	1,000	1
ROOF SHEET	RS-36	6,652	1,000	1
ROOF SHEET	RS-37	6,852	1,000	1
ROOF SHEET	RS-38	7,062	1,000	1
ROOF SHEET	RS-39	7,262	1,000	1
ROOF SHEET	RS-40	7,477	1,000	1
ROOF SHEET	RS-41	7,683	1,000	1
ROOF SHEET	RS-42	7,899	1,000	1
ROOF SHEET	RS-43	8,104	1,000	1
ROOF SHEET	RS-44	8,302	1,000	1
ROOF SHEET	RS-45	8,519	1,000	1
ROOF SHEET	RS-46	8,718	1,000	1
ROOF SHEET	RS-47	8,928	1,000	1
ROOF SHEET	RS-48	9,139	1,000	1
ROOF SHEET	RS-49	9,349	1,000	1
ROOF SHEET	RS-50	9,548	1,000	1
ROOF SHEET	RS-51	9,765	1,000	1
ROOF SHEET	RS-52	9,965	1,000	1
ROOF SHEET	RS-53	10,165	1,000	1
ROOF SHEET	RS-54	10,381	1,000	1
ROOF SHEET	RS-55	10,585	1,000	1
ROOF SHEET	RS-56	10,801	1,000	1
ROOF SHEET	RS-57	10990	1,000	1
ROOF SHEET	RS-58	11,215	1,000	1
ROOF SHEET	RS-59	11,416	1,000	1
ROOF SHEET	RS-60	11,625	1,000	1
ROOF SHEET	RS-61	11,823	1,000	1
ROOF SHEET	RS-62	11,823	1,000	1
ROOF SHEET	RS-63	11,277	1,000	1
ROOF SHEET	RS-64	10,749	1,000	1
ROOF SHEET	RS-65	10,231	1,000	1
ROOF SHEET	RS-66	9,699	1,000	1
ROOF SHEET	RS-67	9,182	1,000	1
ROOF SHEET	RS-68	4,669	1,000	1
ROOF SHEET	RS-69	7,693	1,000	1
ROOF SHEET	RS-70	4,455	1,000	1
ROOF SHEET	RS-71	8,393	1,000	1

ROOF SHEETING PLAN

NOTE:
50mm FIBER GLASS INSULATION

SKY LIGHT & ROOF MONITOR				
DESCRIPTIONS	PART	LENGTH (MM)	WIDTH (MM)	QUANTITY
SKY LIGHT	SKL-01	3,000	1,000	16
RIDGE VENTILATOR	RV-01	3,000	---	8

FOR APPROVAL :

IN ORDER TO SCHEDULE THIS PROJECT IN AN EFFICIENT MANNER , KINDLY RETURN THESE DRAWINGS WITH YOUR ANY CHANGES MADE AFTER THE COMMENTS MARKED IN RED

APPROVAL OF THESE DRAWINGS MAY DELAY THE FABRICATION SCHEDULE AND SUBSEQUENTLY THE DELIVERY OF THE BUILDING.

PLEASE TICK MARK ONLY ONE OF THE FOLLOWING

☐ " APPROVED AS IS "

☐ " APPROVED AS NOTED "

☐ " RESUBMIT AS NOTED "

APPROVE : _____

SIGNATURE: _____

DATE : _____

REV

DATE

DESCRIPTION

DRAWN BY

CHK BY

APR BY

00	10/04/2025	ISSUED FOR APPROVAL	M.A	S.R	NAS
----	------------	---------------------	-----	-----	-----

MAIMAAR

MAIMAAR STEEL Pvt.Ltd
238, Raiwind Road, Thokar Niaz Baig, Lahore, Pakistan
E-mail: nasir.abbas@maimaargroup.com
E-mail: maimaar.steel@gmail.com
Website: www.maimaargroup.com
E-mail: info@maimaargroup.com
Mob-I : +(92-300) 807 4017 ,+(92-333) 807 1115

JOB NO./QUOTE NO.

MSPL-203

BUILDING #

01

PROJECT NAME

WAREHOUSE

CUSTOMER

DHL

JOB SITE LOCATION

RAWAT

ROOF SHEETING PLAN

DWG NO.
18