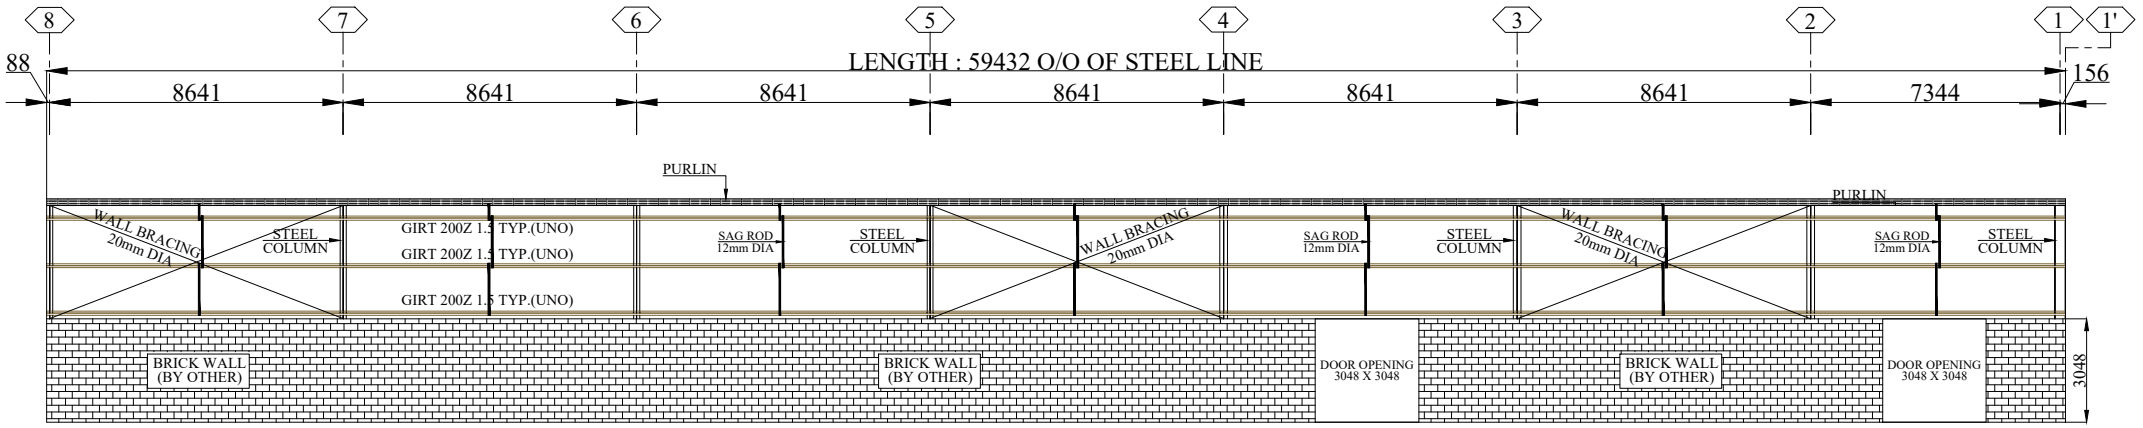

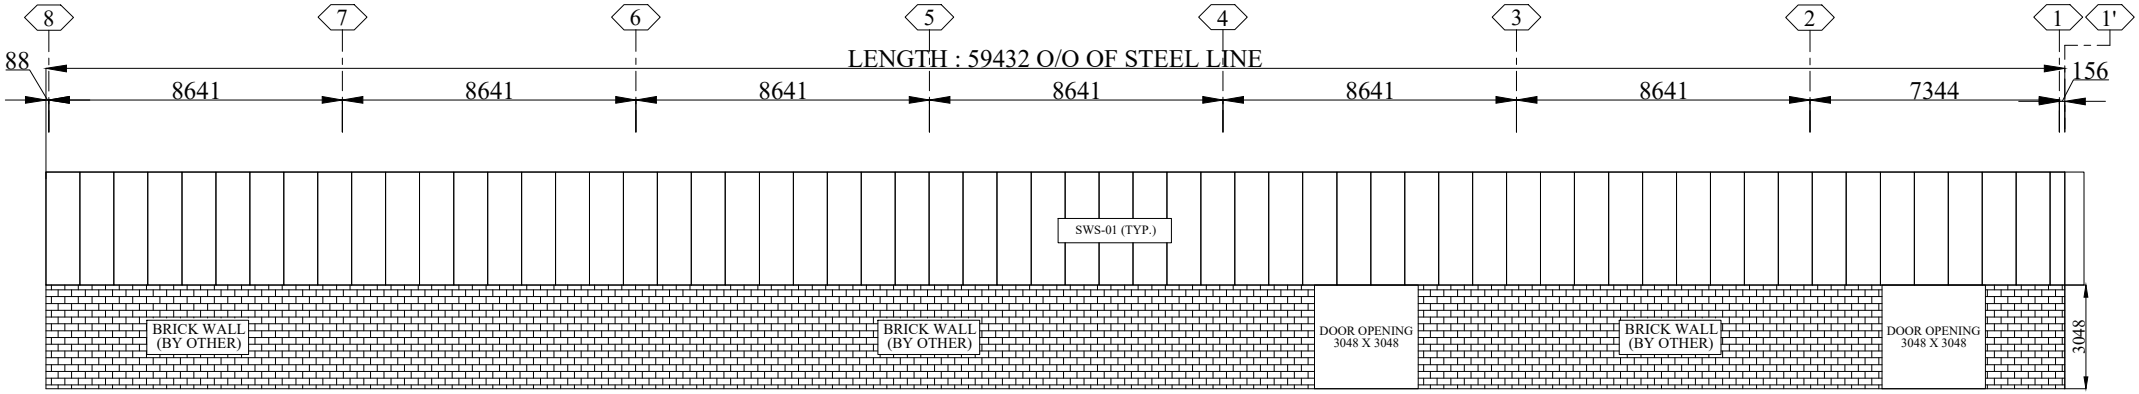

SIDE WALL FRAMING & SHEETING @ G.L I'

SIDE WALL SHEETING

DESCRIPTIONS	PART	LENGTH (MM)	WIDTH (MM)	QUANTITY
SIDE WALL SHEET	SWS-01	3,332	1,000	60

FOR APPROVAL :

IN ORDER TO SCHEDULE THIS PROJECT IN AN EFFICIENT MANNER , KINDLY RETURN THESE DRAWINGS WITH YOUR ANY CHANGES MADE AFTER THE COMMENTS MARKED IN RED APPROVAL OF THESE DRAWINGS MAY DELAY THE FABRICATION SCHEDULE AND SUBSEQUENTLY THE DELIVERY OF THE BUILDING.

PLEASE TICK MARK ONLY ONE OF THE FOLLOWIMG

☐ " APPROVED AS IS "
☐ " APPROVED AS NOTED"
☐ " RESUBMIT AS NOTED "

APPROVE : _____
SIGNATURE: _____
DATE : _____

REV	DATE	DESCRIPTION	DRAWN BY	CHK BY	APR BY
00	10/04/2025	ISSUED FOR APPROVAL	M.A	S.R	NAS

MAIMAAR

MAIMAAR STEEL Pvt.Ltd
238, Raiwind Road, Thokar Niaz Baig, Lahore, Pakistan
E-mail: nasir.abbas@maimaargroup.com
E-mail: maimaar.steel@gmail.com
Website: www.maimaargroup.com
E-mail: info@maimaargroup.com
Mob-1 : +(92-300) 807 4017 ,+(92-333) 807 1115

JOB NO./QUOTE NO.	MSPL-203		BUILDING #	01
PROJECT NAME	WAREHOUSE			
CUSTOMER	DHL			
JOB SITE LOCATION	RAWAT			

SIDE WALL FRAMING & SHEETING @ G.L I'

DWG NO. 22