
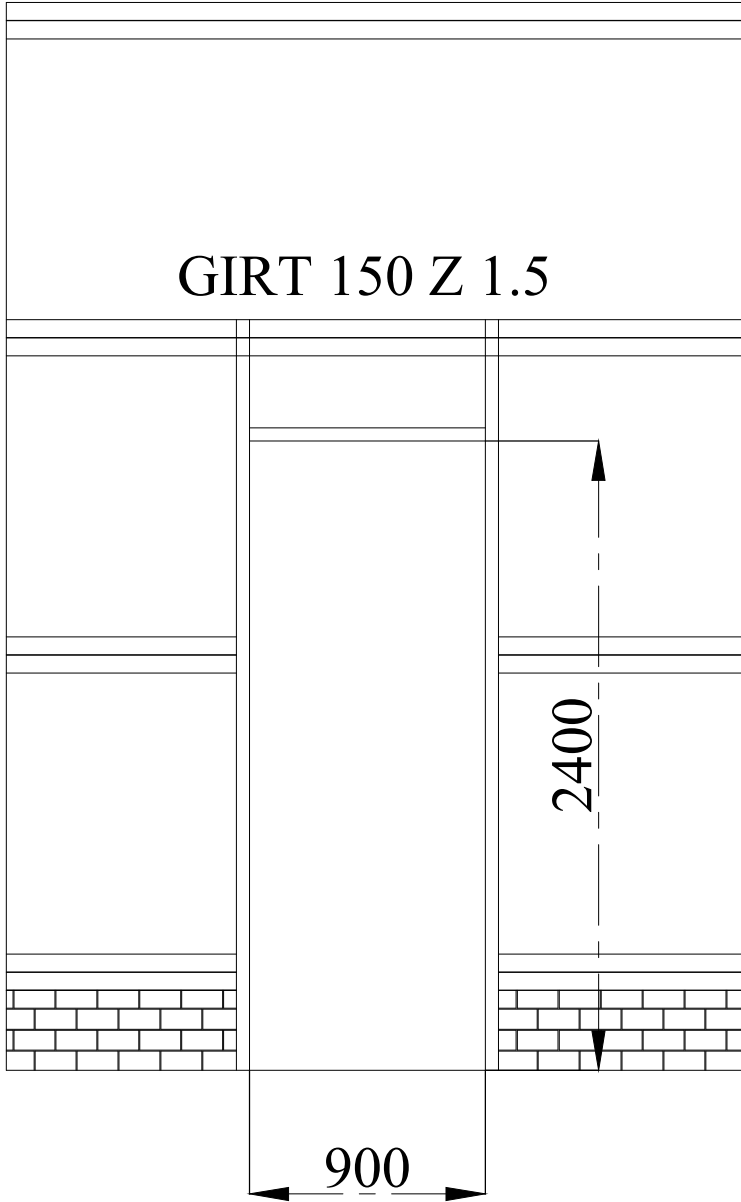
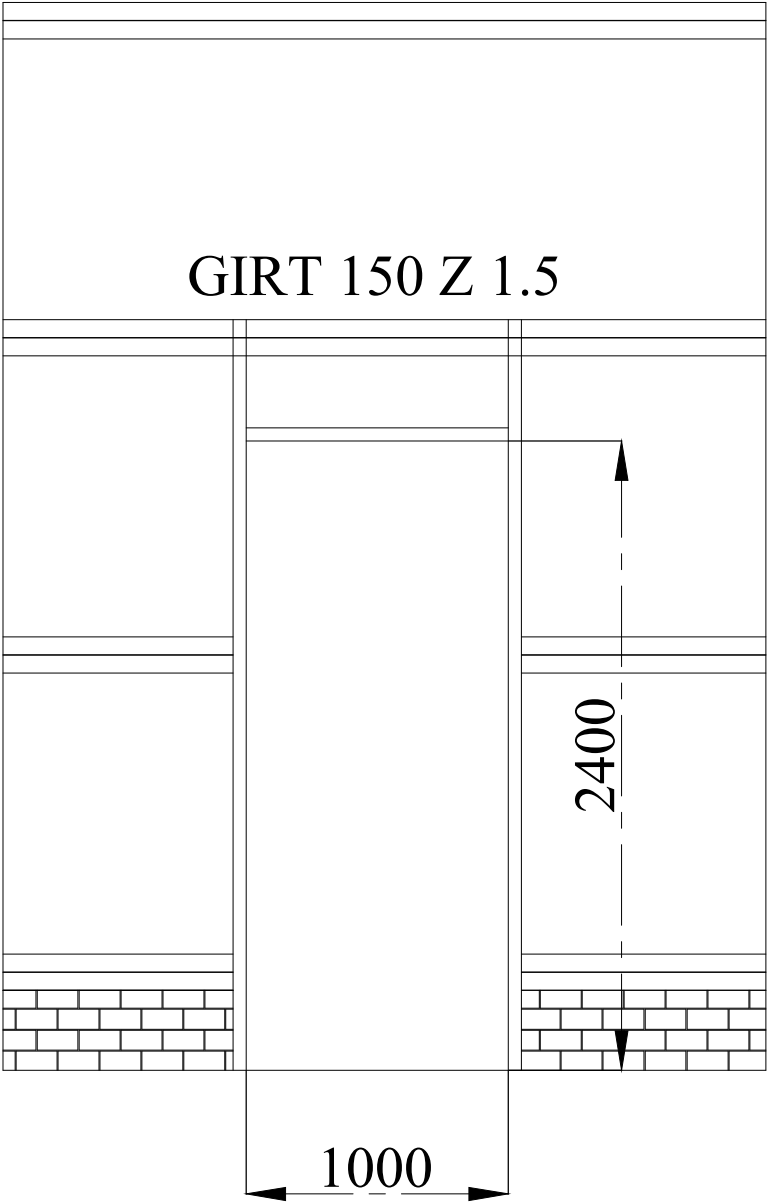


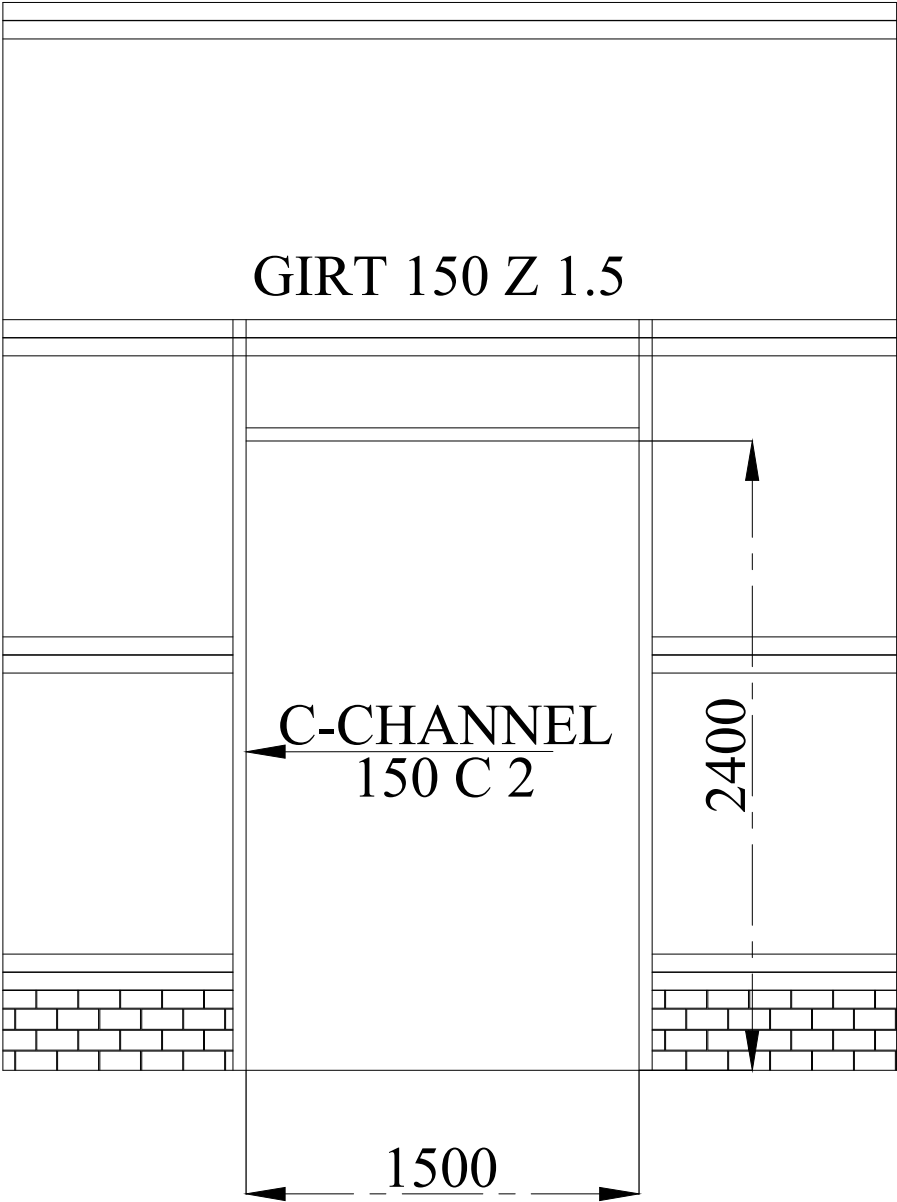

- NOTE :-**
- THE HEIGHT OF THE PARTITION WALL IS UP TO THE BOTTOM OF THE LINER.
 - ROCK WALL INSULATION USE IN PARTITION WALL.
 - 0.5mm PPGL LINER SHEET BOTH SIDES OF PARTITION WALL.
 - PARTITION WALLS GIRTS SPACING WILL BE 1210mm & THERE WILL C - CHANNEL OF 2mm THICKNESS ON TOP OF PARTITION WALL.

TYPICAL DOOR OPENING FRAMING

FOR APPROVAL :
IN ORDER TO SCHEDULE THIS PROJECT
IN AN EFFICIENT MANNER , KINDLY
RETURN THESE DRAWINGS WITH YOUR
ANY CHANGES MADE AFTER THE
COMMENTS MARKED IN RED
APPROVAL OF THESE DRAWINGS MAY
DELAY THE FABRICATION SCHEDULE AND
SUBSEQUENTLY THE DELIVERY OF THE
BUILDING.
PLEASE TICK MARK ONLY ONE OF THE FOLLOWING

☐ " APPROVED AS IS "
☐ " APPROVED AS NOTED "
☐ " RESUBMIT AS NOTED "

APPROVE : _____
SIGNATURE: _____
DATE : _____

PROJECT TITLE:
NATIONAL DATA CENTER



LEAD CONSULTANT:
AL IMAM Enterprises Pvt. Ltd.
ARCHITECTURE – INTERIOR DESIGN – URBAN DESIGN
47–L Model Town Extension Lahore – PAKISTAN
Tel: +92–42–3516 4262
Fax: +92–42–3516 7902
Email: info@alimam.biz
Web: http://www.alimam.biz



These Drawings Remain The Property of AL IMAM Enterprises (Pvt) Ltd
And Any Reproduction Without Authorization is Unlawful

ISSUED FOR CONSTRUCTION

CONTRACTOR

Action Required By

☐ A. APPROVAL
☐ B. APPROVAL AS NOTED
☐ C. APPROVED AS NOTED / RESUBMIT
☐ D. NO APPROVED AS NOTED / RESUBMIT
☐ E. REJECTED
☐ F. OTHER/ SIGNATURE /DATE

01	ISSUED FOR CONSTRUCTION	22–07–2025	
REV.	DESCRIPTION	DATE	
DRAWN BY:	AL–IMAM	DESIGNED BY :	AL–IMAM
CHECKED BY:	AL–IMAM	PROJECT NO:	815/CBD/DC/LHR
DATE :	22–07–2025	SCALE:	AS SHOWN

DRAWING TITLE:

TYPICAL DOOR OPENING FRAMING

DRAWING NUMBER:

18