
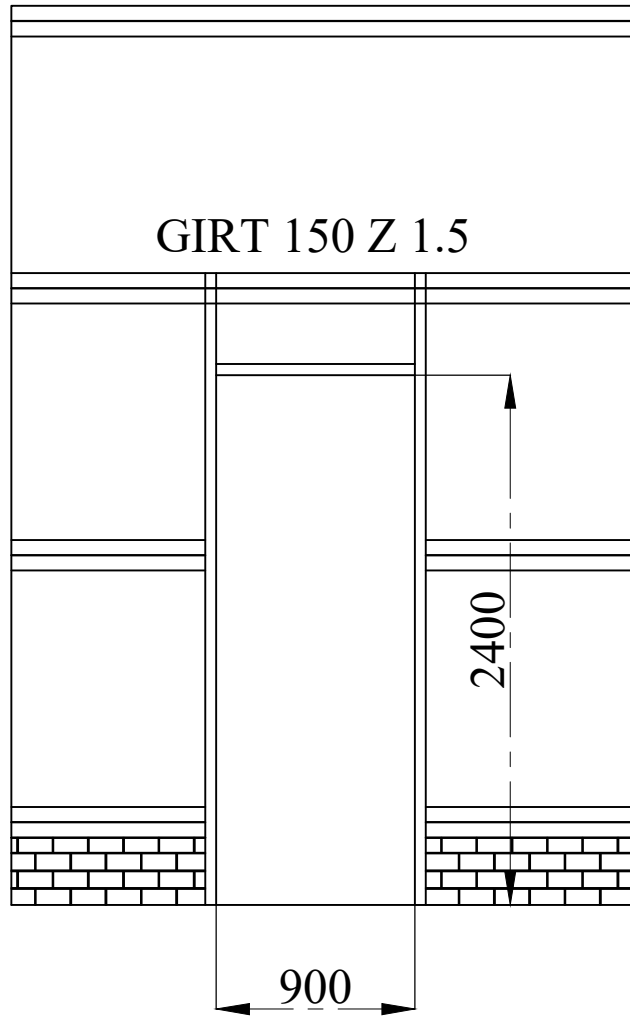
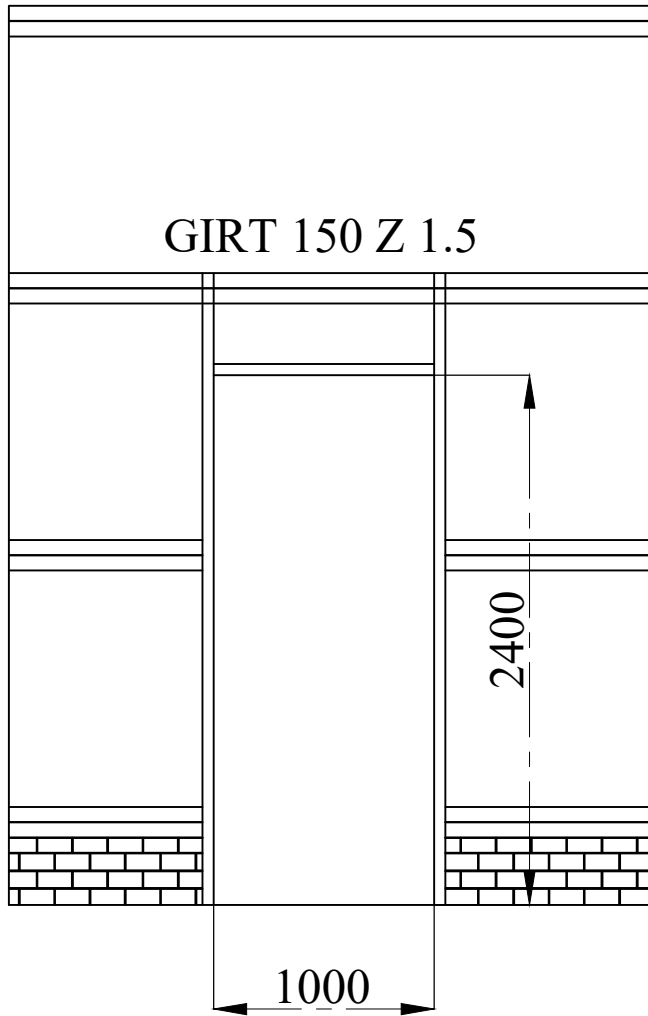


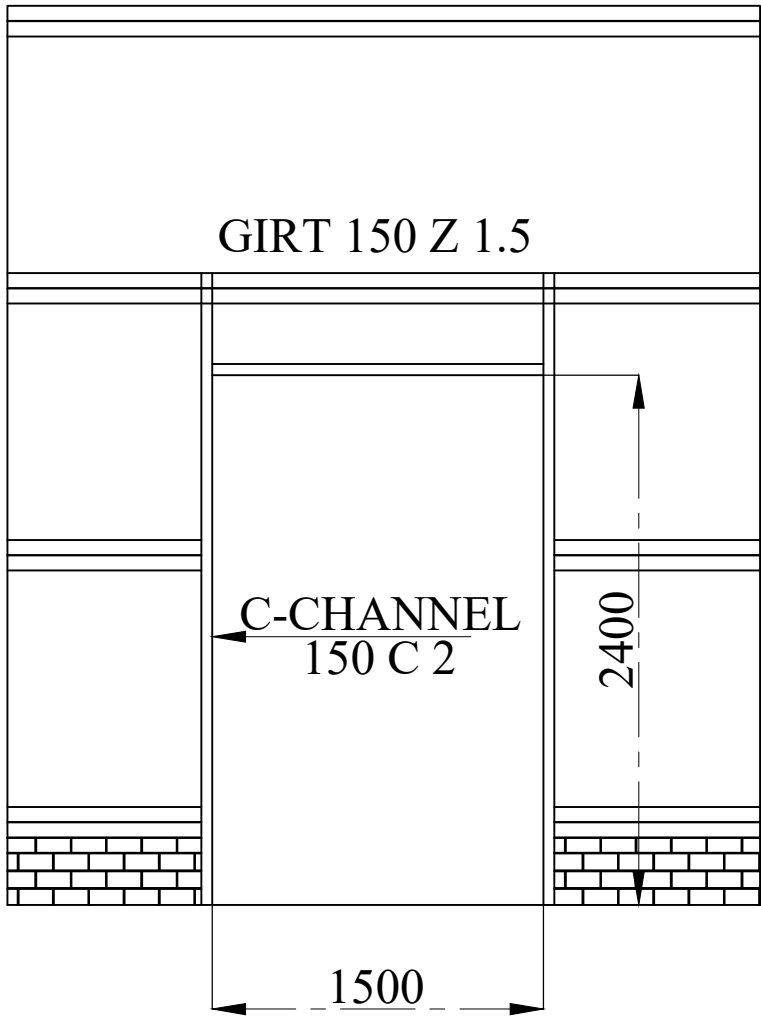

NOTE :-

- THE HEIGHT OF THE PARTITION WALL IS UP TO THE BOTTOM OF THE LINER.
- ROCK WALL INSULATION USE IN PARTITION WALL.
- 0.5mm PPGL LINER SHEET BOTH SIDES OF PARTITION WALL.
- PARTITION WALLS GIRTS SPACING WILL BE 1210mm & THERE WILL C - CHANNEL OF 2mm THICKNESS ON TOP OF PARTITION WALL.

TYPICAL DOOR OPENING FRAMING

FOR APPROVAL :

IN ORDER TO SCHEDULE THIS PROJECT IN AN EFFICIENT MANNER , KINDLY RETURN THESE DRAWINGS WITH YOUR ANY CHANGES MADE AFTER THE COMMENTS MARKED IN RED APPROVAL OF THESE DRAWINGS MAY DELAY THE FABRICATION SCHEDULE AND SUBSEQUENTLY THE DELIVERY OF THE BUILDING. PLEASE TICK MARK ONLY ONE OF THE FOLLOWING

☐ " APPROVED AS IS "
☐ " APPROVED AS NOTED "
☐ " RESUBMIT AS NOTED "
APPROVE : _____
SIGNATURE: _____
DATE : _____

PROJECT TITLE:
NATIONAL DATA CENTER

DATA FORT

LEAD CONSULTANT:
AL IMAM Enterprises Pvt. Ltd.
ARCHITECTURE – INTERIOR DESIGN – URBAN DESIGN
47–L Model Town Extension Lahore – PAKISTAN
Tel: +92–42–3516 4282
Fax: +92–42–3516 7802
Email: info@alimam.biz
Web: http://www.alimam.biz

These Drawings Remain The Property of AL IMAM Enterprises (Pvt) Ltd And Any Reproduction Without Authorization Is Unlawful

ISSUED FOR CONSTRUCTION

CONTRACTOR

Action Required By

☐ A. APPROVAL
☐ B. APPROVAL AS NOTED
☐ C. APPROVED AS NOTED / RESUBMIT
☐ D. NO APPROVED AS NOTED / RESUBMIT
☐ E. REJECTED
☐ F. OTHER / SIGNATURE / DATE

01 ISSUED FOR CONSTRUCTION 09-07-2025
REV. DESCRIPTION DATE

DRAWN BY: AL-IMAM DESIGNED BY: AL-IMAM
CHECKED BY: AL-IMAM PROJECT NO: 815/CBD/DC/LHR
DATE: 09-07-2025 SCALE: AS SHOWN

DRAWING TITLE:

TYPICAL DOOR OPENING FRAMING

DRAWING NUMBER:
18