


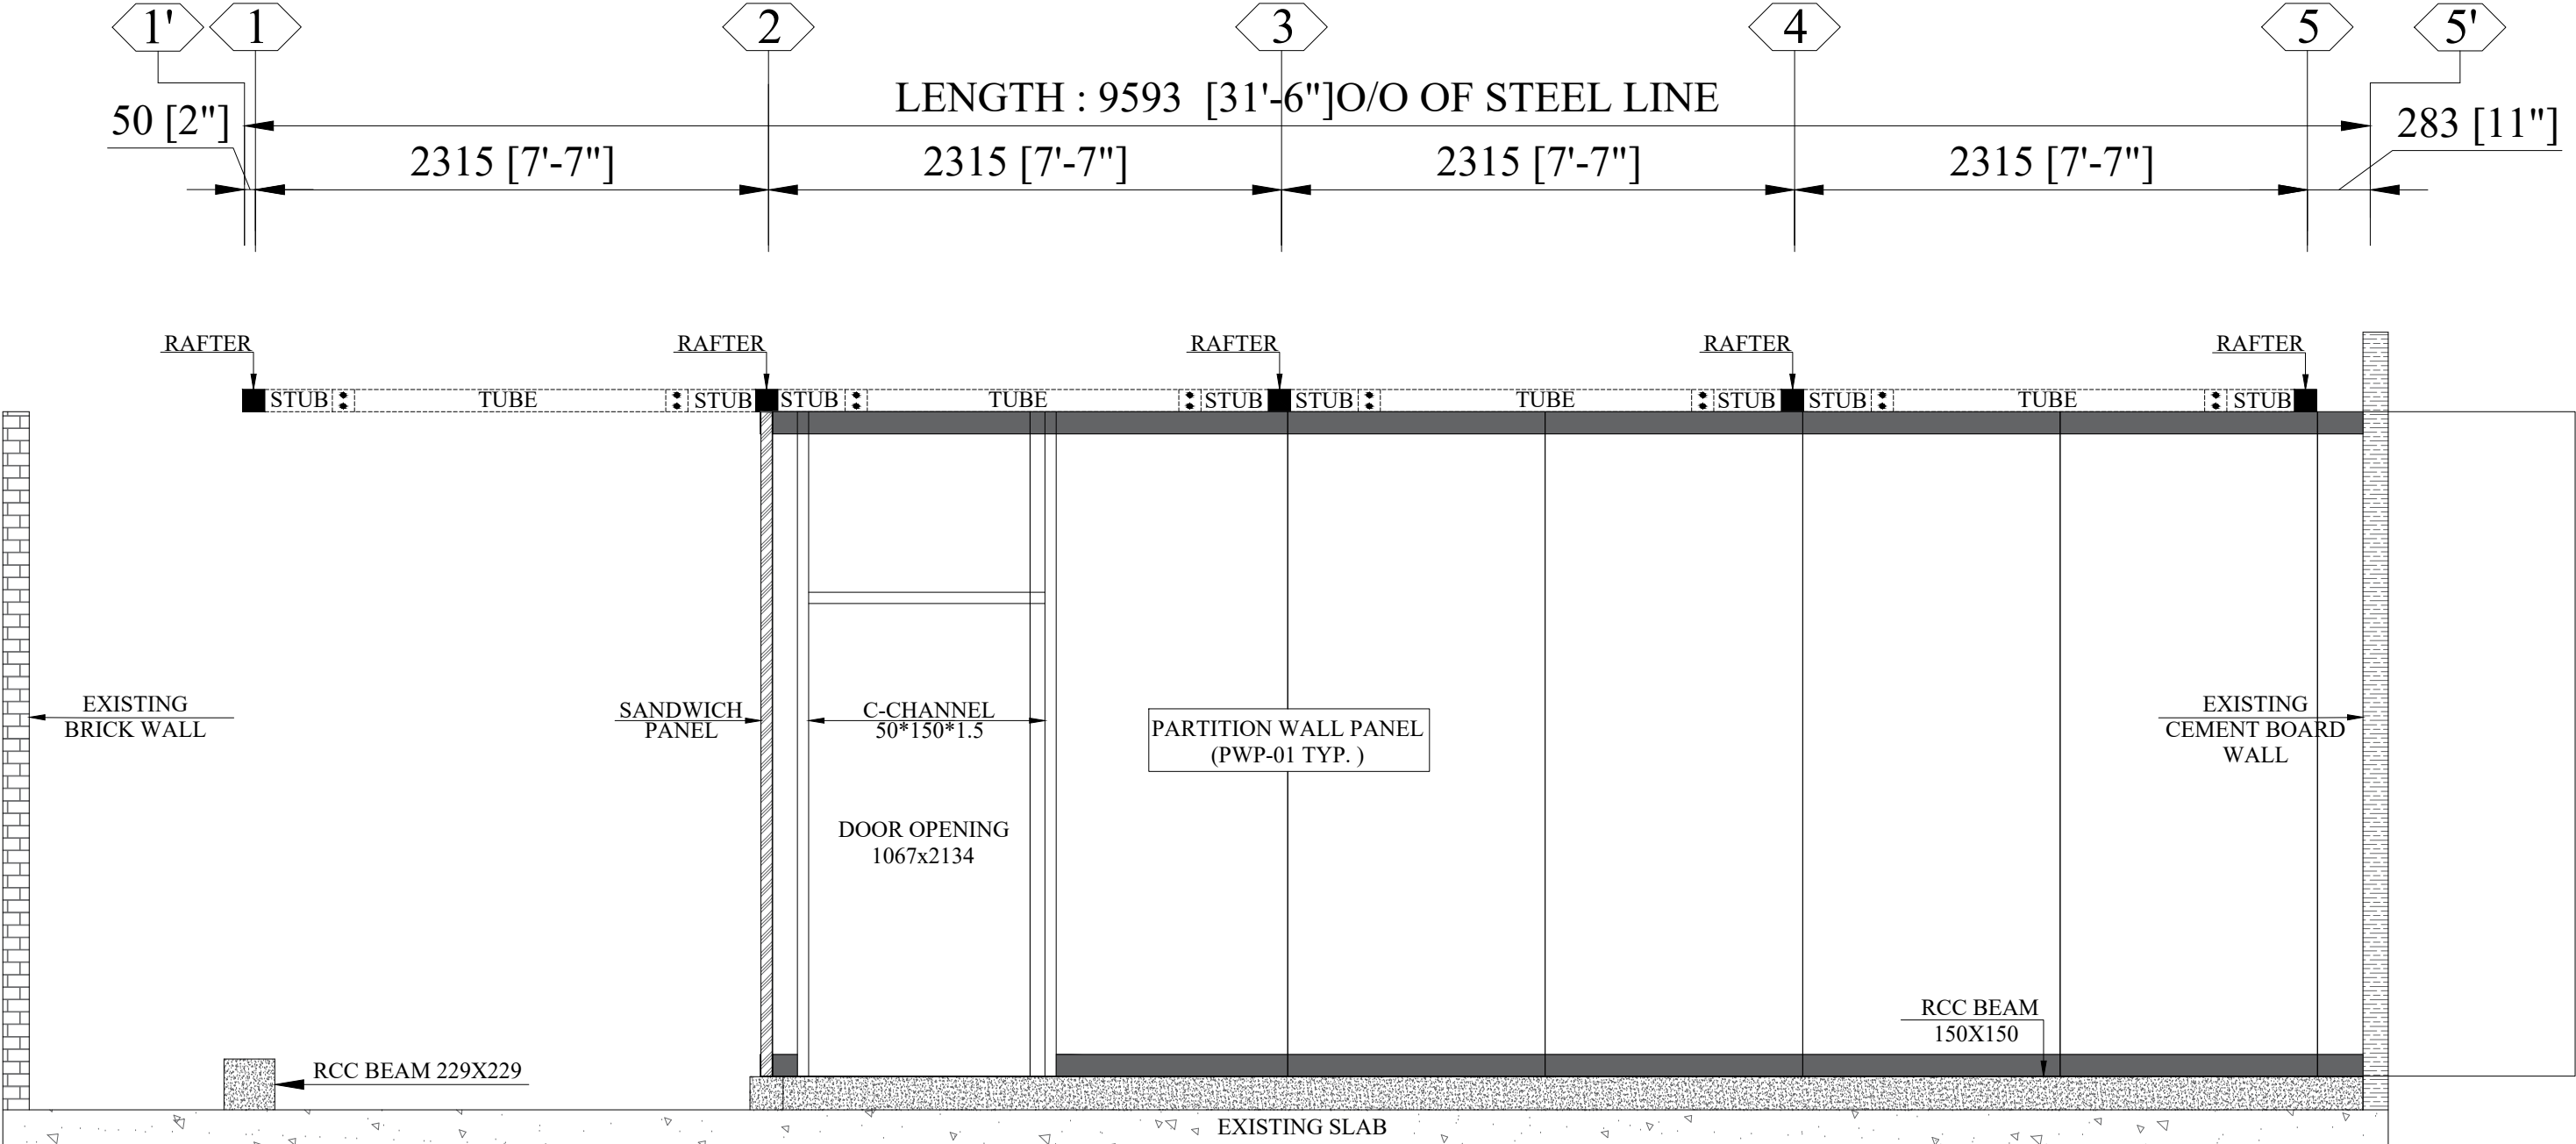

PARTITION WALL MID IN
GRID-A & B

PARTITION WALL PANEL TABLE

DESCRIPTIONS	PART	LENGTH	WIDTH	QUANTITY
PARTITION WALL PANEL-01	PWP-01	2997	1162	07

FOR APPROVAL :
IN ORDER TO SCHEDULE THIS PROJECT
IN AN EFFICIENT MANNER , KINDLY
RETURN THESE DRAWINGS WITH YOUR
ANY CHANGES MADE AFTER THE
COMMENTS MARKED IN RED
APPROVAL OF THESE DRAWINGS MAY
DELAY THE FABRICATION SCHEDULE AND
SUBSEQUENTLY THE DELIVERY OF THE
BUILDING.
PLEASE TICK MARK ONLY ONE OF THE FOLLOWING

☐ " APPROVED AS IS "
☐ " APPROVED AS NOTED"
☐ " RESUBMIT AS NOTED "

APPROVE : _____
SIGNATURE: _____
DATE : _____

REV	DATE	DESCRIPTION	DRAWN BY	CHK BY	APR BY
01	02-Oct-24	ISSUED FOR APPROVAL	M.A	KAS	NAS

MAIMAAR



MAIMAAR STEEL Pvt.Ltd
238, Raiwind Road, Thokar Niaz Baig, Lahore, Pakistan
E-mail: nasir.abbas@maimaargroup.com
E-mail: maimaar.steel@gmail.com
Website: www.maimaargroup.com
E-mail: info@maimaargroup.com
Mob-1 : +(92-300) 807 4017 ,+(92-333) 807 1115

JOB NO./QUOTE NO.	MSPL-140	BUILDING #	01
PROJECT NAME	SUPPLY & INSTALLATION OF MONO SLOPE SANDWICH PANEL ROOM		
CUSTOMER	AWAIS CHAMBER		
JOB SITE LOCATION	LAHORE		

PARTITION WALL MID IN
GRID-A & B

DWG NO.
12