


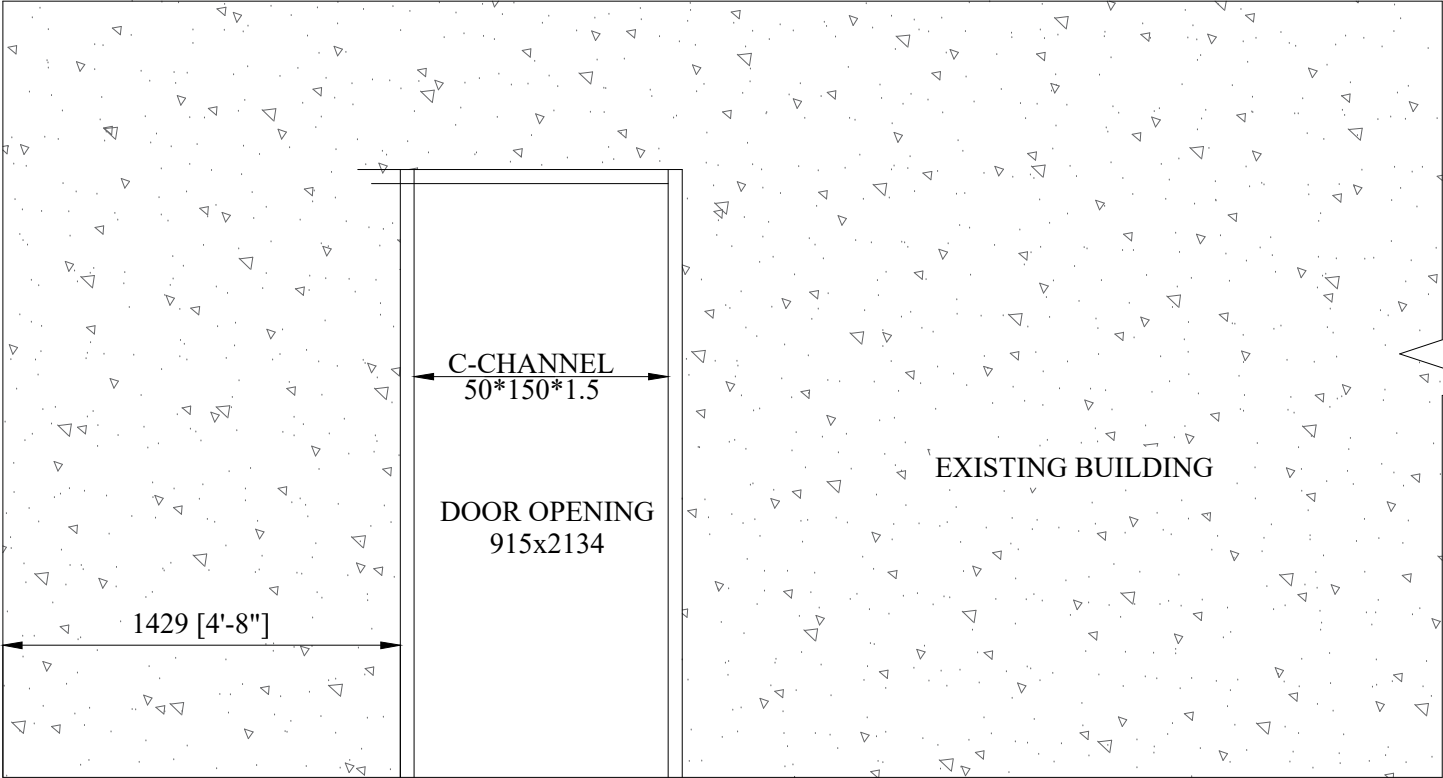

EXISTING END WALL DOOR
ELEVATION & PANEL

REV	DATE	DESCRIPTION	DRAWN BY	CHK BY	APR BY
02	10/10/2024	ISSUED FOR APPROVAL	M.A	KAS	NAS

MAIMAAR

MAIMAAR STEEL Pvt.Ltd
238, Raiwind Road, Thokar Niaz Baig, Lahore, Pakistan
E-mail: nasir.abbas@maimaargroup.com
E-mail: maimaar.steel@gmail.com
Website: www.maimaargroup.com
E-mail: info@maimaargroup.com
Mob-1 : +(92-300) 807 4017 ,+(92-333) 807 1115

JOB NO./QUOTE NO.	MSPL-140	BUILDING #	01
PROJECT NAME	SUPPLY & INSTALLATION OF MONO SLOPE SANDWICH PANEL ROOM		
CUSTOMER	AWAIS CHAMBER		
JOB SITE LOCATION	LAHORE		

EXISTING END WALL DOOR
ELEVATION & PANEL

DWG NO.
14

DOOR PANEL TABLE

DESCRIPTIONS	PART	LENGTH	WIDTH	QUANTITY
DOOR MICRO RIB PANEL–01	DMRP–01	2134	1162	01

FOR APPROVAL :
IN ORDER TO SCHEDULE THIS PROJECT
IN AN EFFICIENT MANNER , KINDLY
RETURN THESE DRAWINGS WITH YOUR
ANY CHANGES MADE AFTER THE
COMMENTS MARKED IN RED
APPROVAL OF THESE DRAWINGS MAY
DELAY THE FABRICATION SCHEDULE AND
SUBSEQUENTLY THE DELIVERY OF THE
BUILDING.
PLEASE TICK MARK ONLY ONE OF THE FOLLOWING

☐ " APPROVED AS IS "
☐ " APPROVED AS NOTED"
☐ " RESUBMIT AS NOTED "

APPROVE : _____
SIGNATURE: _____
DATE : _____