


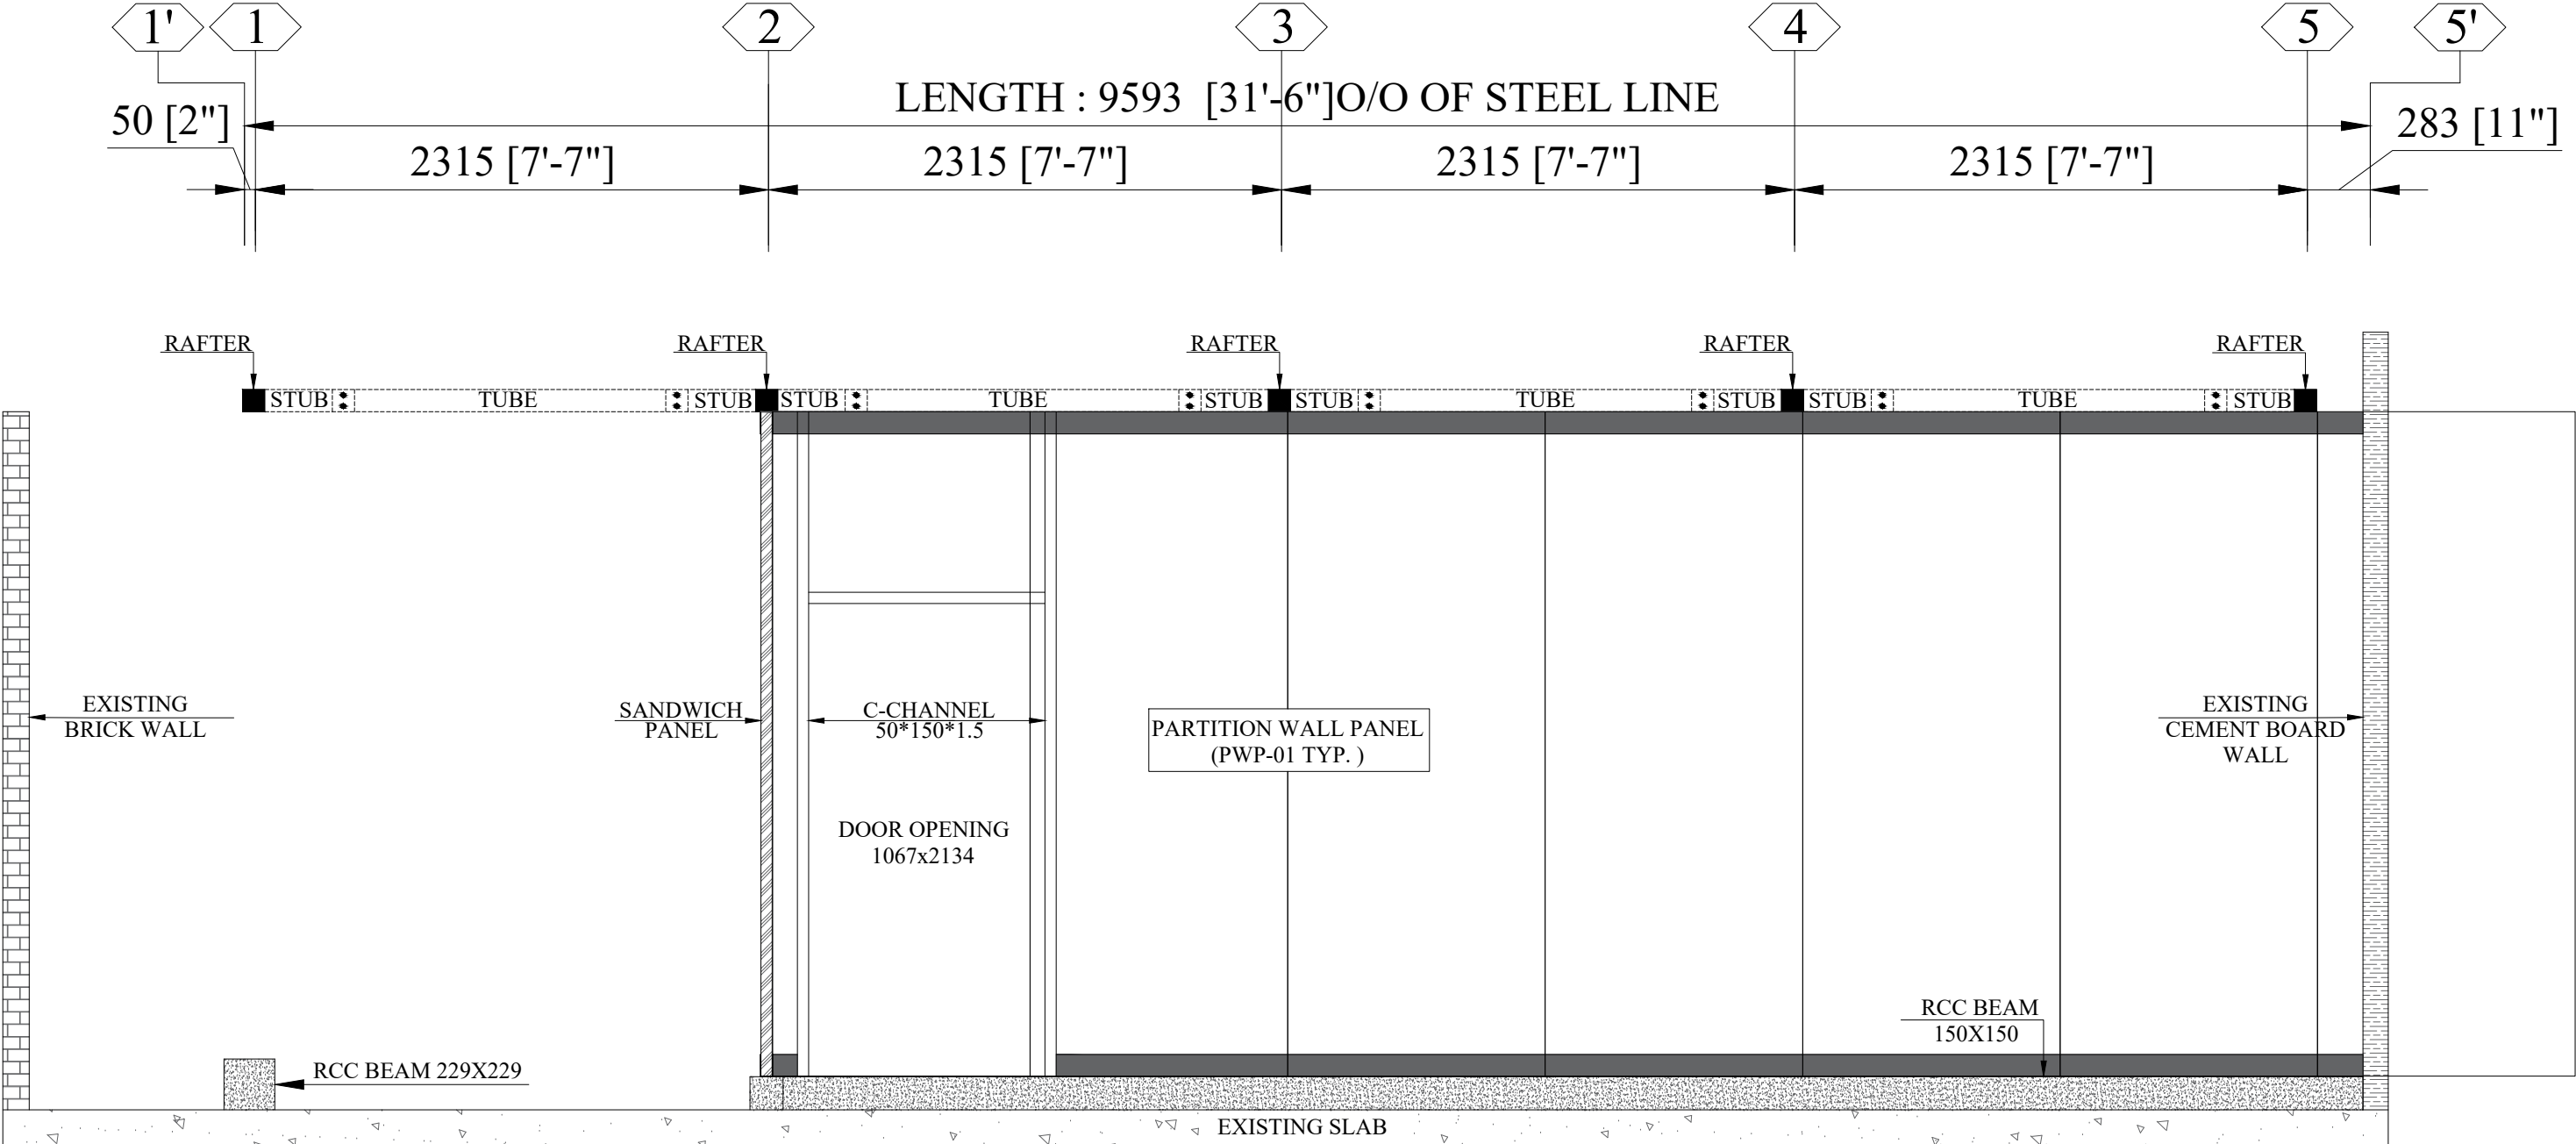

PARTITION WALL MID IN
GRID-A & B

PARTITION WALL PANEL TABLE

DESCRIPTIONS	PART	LENGTH	WIDTH	QUANTITY
PARTITION WALL PANEL-01	PWP-01	2997	1162	07

FOR APPROVAL :
IN ORDER TO SCHEDULE THIS PROJECT
IN AN EFFICIENT MANNER , KINDLY
RETURN THESE DRAWINGS WITH YOUR
ANY CHANGES MADE AFTER THE
COMMENTS MARKED IN RED
APPROVAL OF THESE DRAWINGS MAY
DELAY THE FABRICATION SCHEDULE AND
SUBSEQUENTLY THE DELIVERY OF THE
BUILDING.
PLEASE TICK MARK ONLY ONE OF THE FOLLOWING

☐ " APPROVED AS IS "
☐ " APPROVED AS NOTED"
☐ " RESUBMIT AS NOTED "

APPROVE : _____
SIGNATURE: _____
DATE : _____

REV	DATE	DESCRIPTION	DRAWN BY	CHK BY	APR BY
01	02-Oct-24	ISSUED FOR APPROVAL	M.A	KAS	NAS
MAIMAAR MAIMAAR STEEL Pvt.Ltd 238, Raiwind Road, Thokar Niaz Baig, Lahore, Pakistan E-mail: nasir.abbas@maimaargroup.com E-mail: maimaar.steel@gmail.com Website: www.maimaargroup.com E-mail: info@maimaargroup.com Mob-1 : +(92-300) 807 4017 ,+(92-333) 807 1115					
JOB NO./QUOTE NO.		MSPL-140		BUILDING #	01
PROJECT NAME		SUPPLY & INSTALLATION OF MONO SLOPE SANDWICH PANEL ROOM			
CUSTOMER		AWAIS CHAMBER			
JOB SITE LOCATION		LAHORE			
PARTITION WALL MID IN GRID-A & B					DWG NO.
					12