




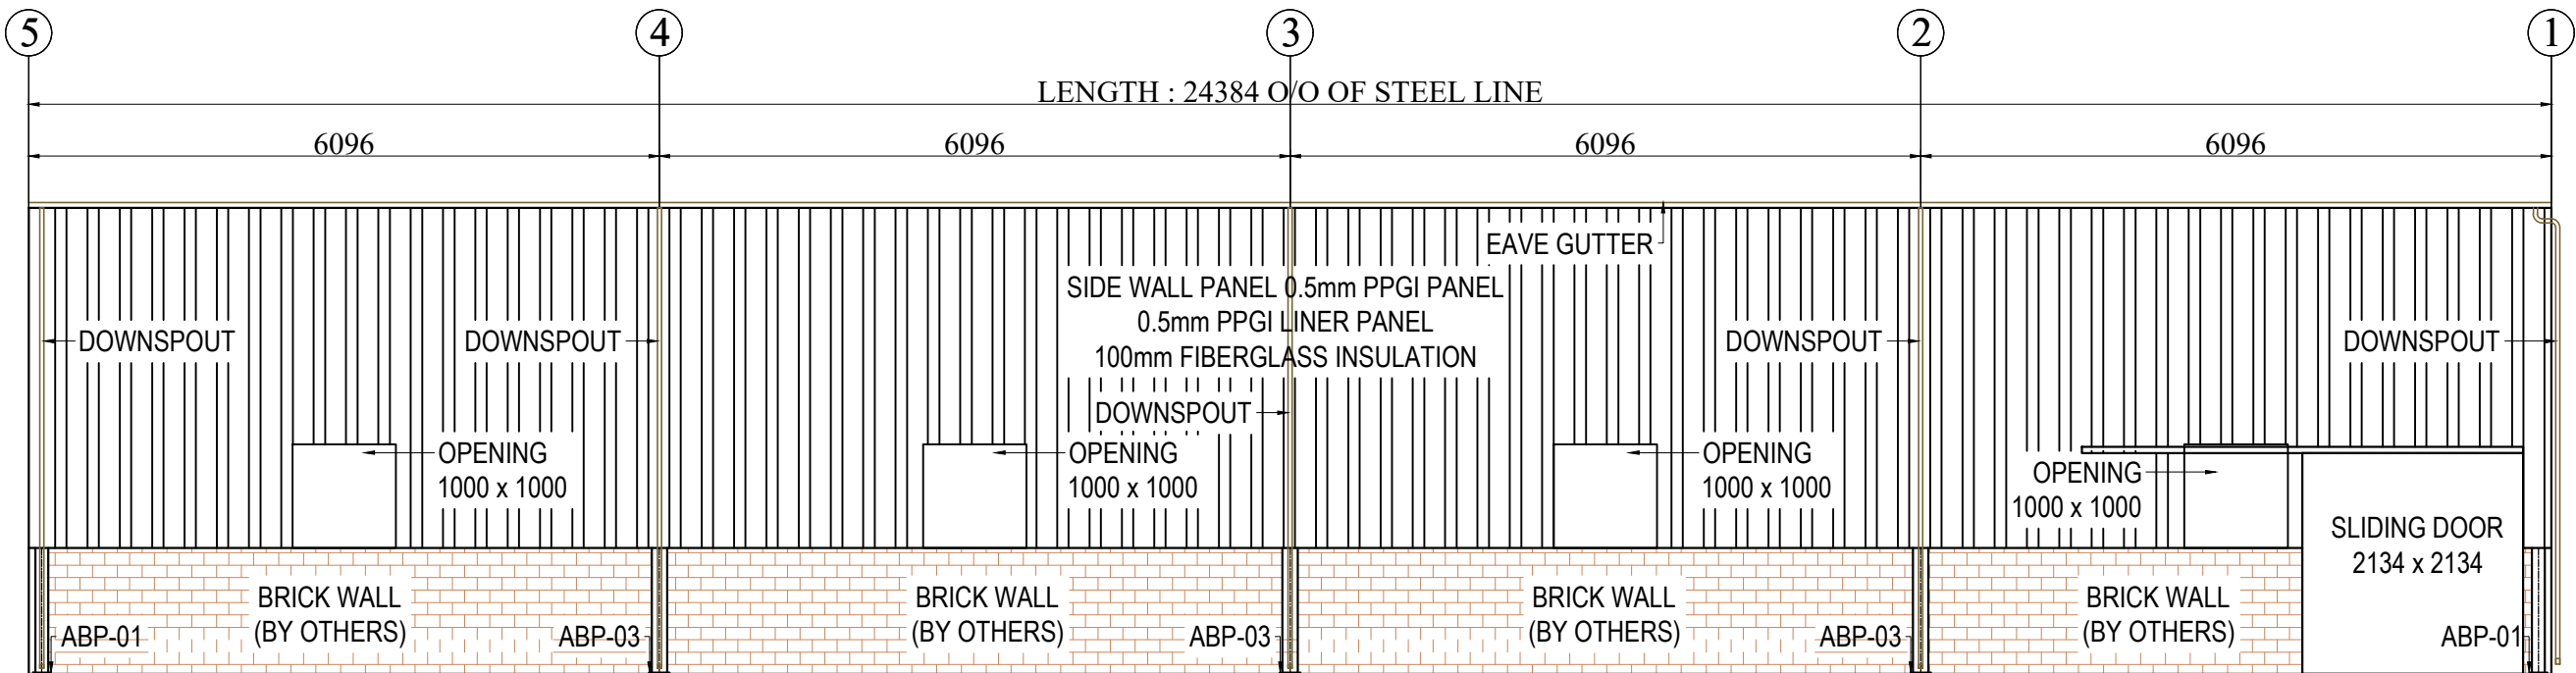

SIDE WALL FRAMING & SHEETING @ GRID - A

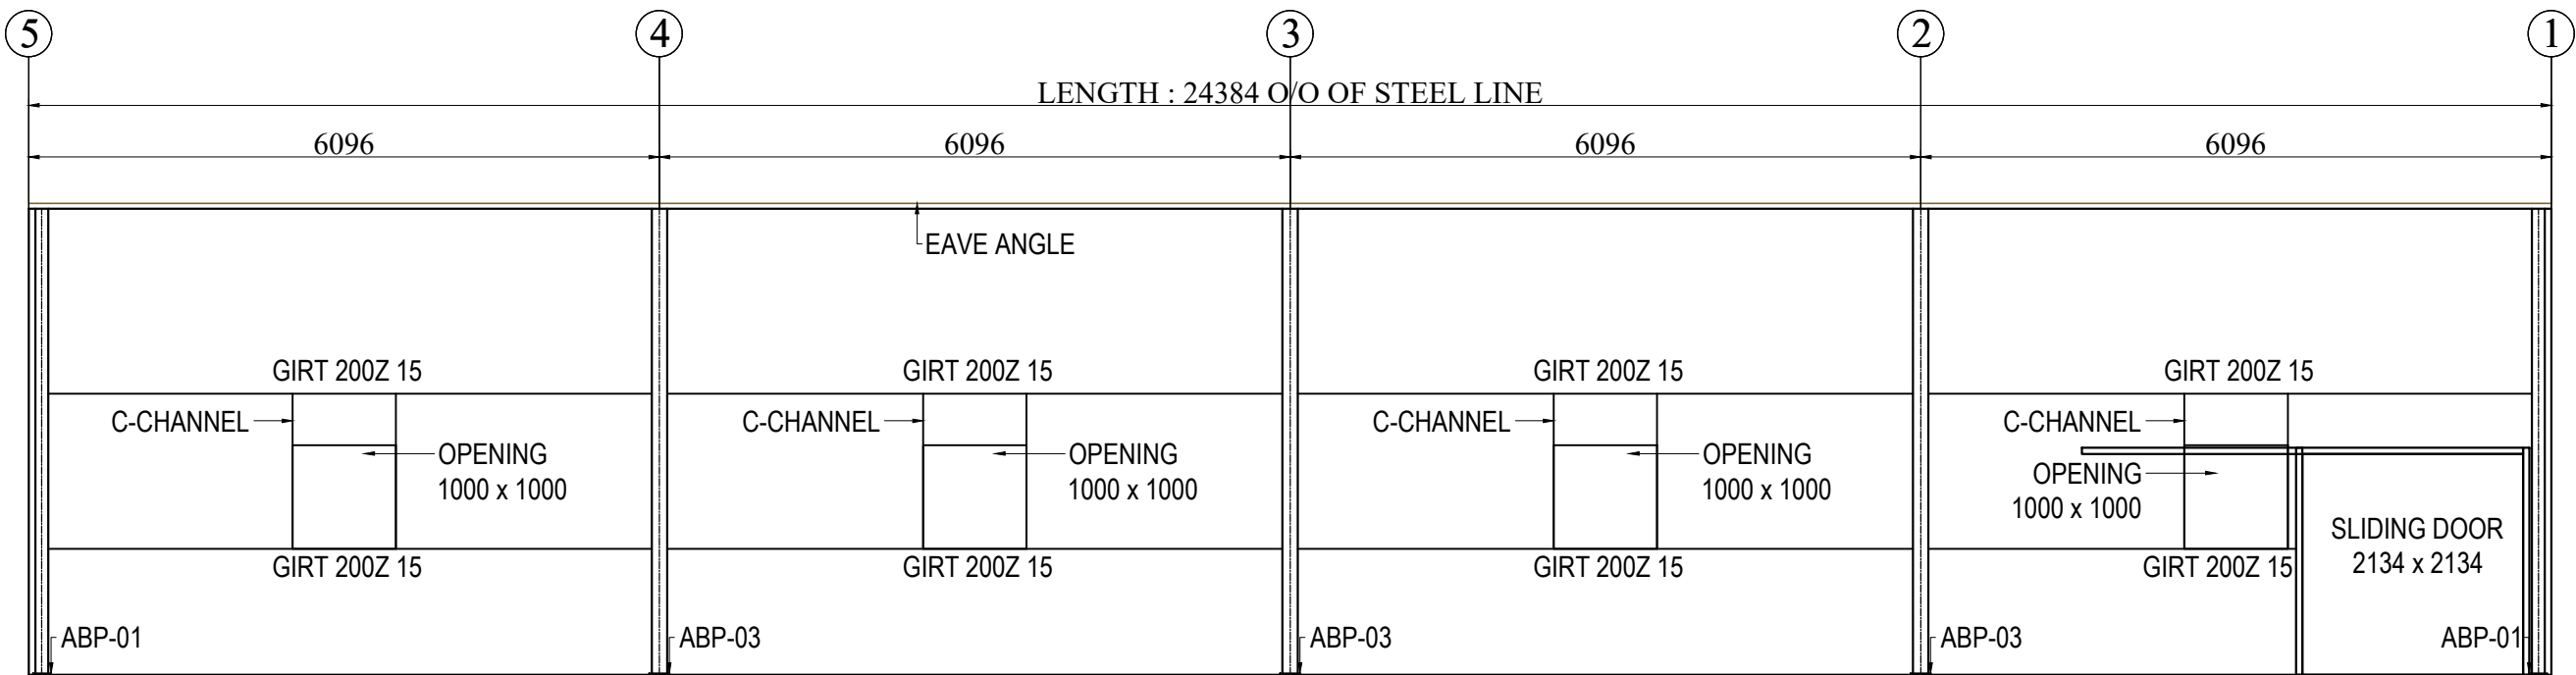

01	13-11-21	ISSUED FOR APPROVAL	R.A	YEA	YEA
00	06-08-21	ISSUED FOR APPROVAL	FZN	YEA	YEA
REV.	DATE	DESCRIPTION	DRWN BY	CHK BY	APR BY

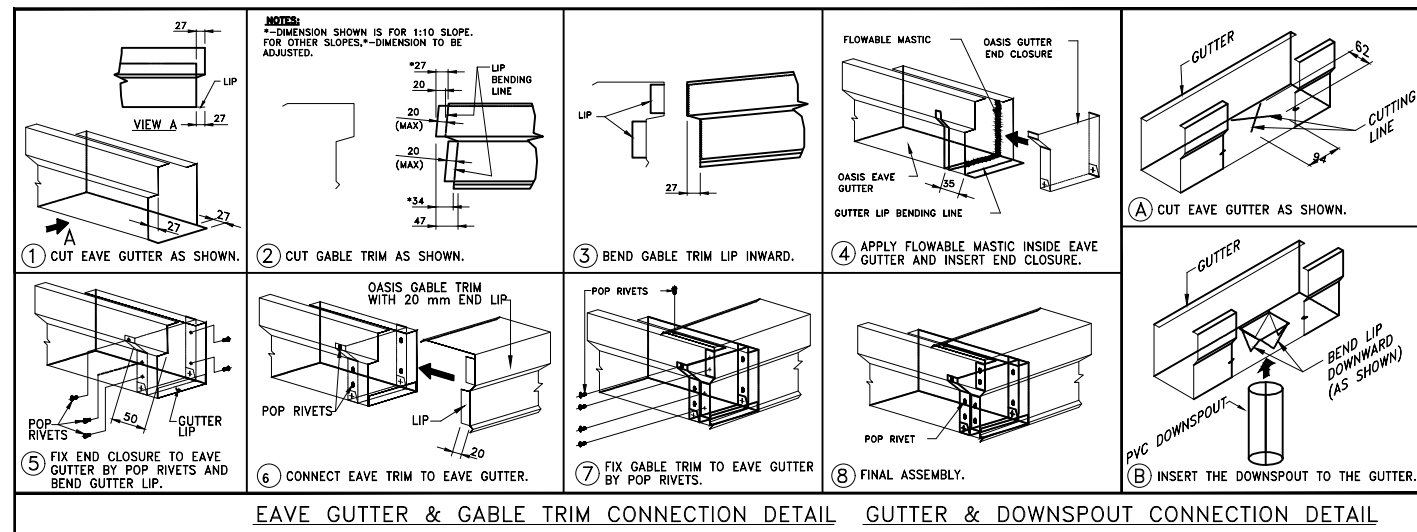

MAIMAAR STEEL Pvt.Ltd
 238, Raiwind Road, Thokar Niaz Baig ,LAHORE, Pakistan
 E-mail: nasir.abbas@maimaargroup.com
 E-mail: maimaar.steel@gmail.com
 Website: www.maimaargroup.com
 E-mail: nasir.abbas@maimaargroup.com
 Mob-1 : +(92-300) 807 4017 , +(92-333) 807 1115

JOB NO./QUOTE NO.	MSPL-027	BLDG #.	01
PROJECT NAME	BARN STITCHING - HALL # 02		
CUSTOMER	AWAN SPORTS		
JOBSITE LOCATION	SIALKOT		

SIDE WALL FRAMING & SHEETING @ GRID - A

DWG. NO.

09