


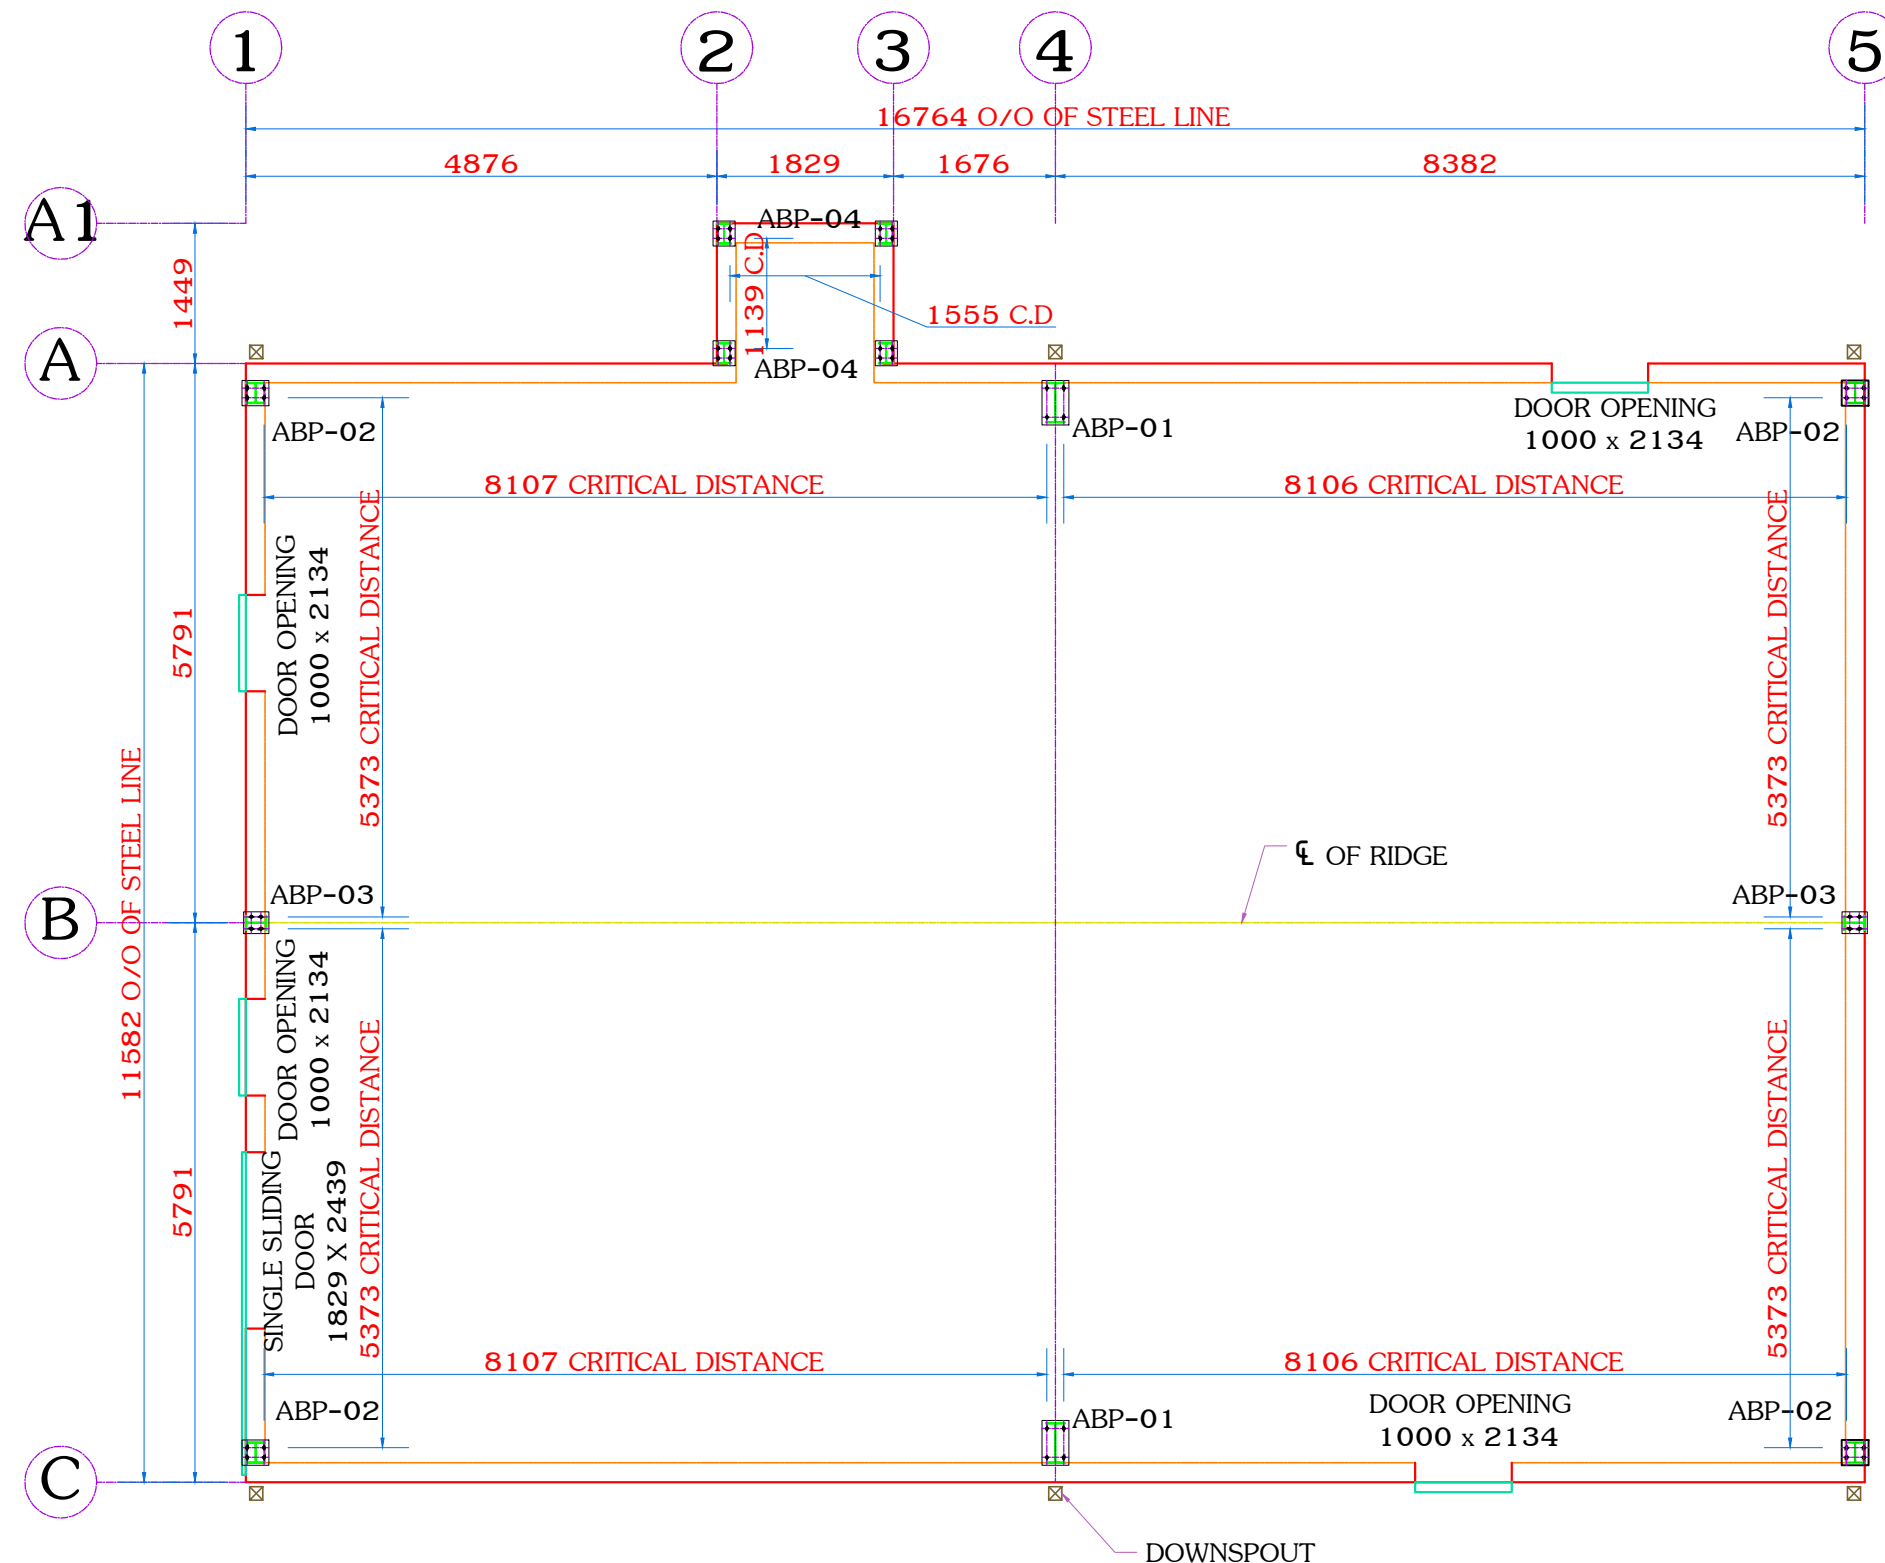

COLUMN LAYOUT PLAN

NOT FOR CONSTRUCTION

FOR APPROVAL :
IN ORDER TO SCHEDULE THIS PROJECT
IN AN EFFICIENT MANNER , KINDLY
RETURN THESE DRAWINGS WITH YOUR
ANY CHANGES MADE AFTER THE
COMMENTS MARKED IN RED
APPROVAL OF THESE DRAWINGS MAY
DELAY THE FABRICATION SCHEDULE AND
SUBSEQUENTLY THE DELIVERY OF THE
BUILDING.
PLEASE TICK MARK ONLY ONE OF THE FOLLOWING

Table with 6 columns: REV., DATE, DESCRIPTION, DRWN BY, CHK BY, APR BY. It contains revision history for the drawing.



MAIMAAR STEEL BUILDING Pvt.Ltd
105, Raiwind Road, Thokar Niaz Baig ,Lahore, Pakistan
E-mail: nasir.abbas@maimaargroup.com
E-mail: maimaar.steel@gmail.com
Website: www.maimaargroup.com
E-mail: nasir.abbas@maimaargroup.com
Mob-1 : +(92-300) 807 4017 ,+(92-333) 807 1115

Table with project details including Job No./Quote No. (MSPL-004), Project Name (BOILER SHED), Customer, Jobsite Location (LAHORE), and Drawing No. (01).