



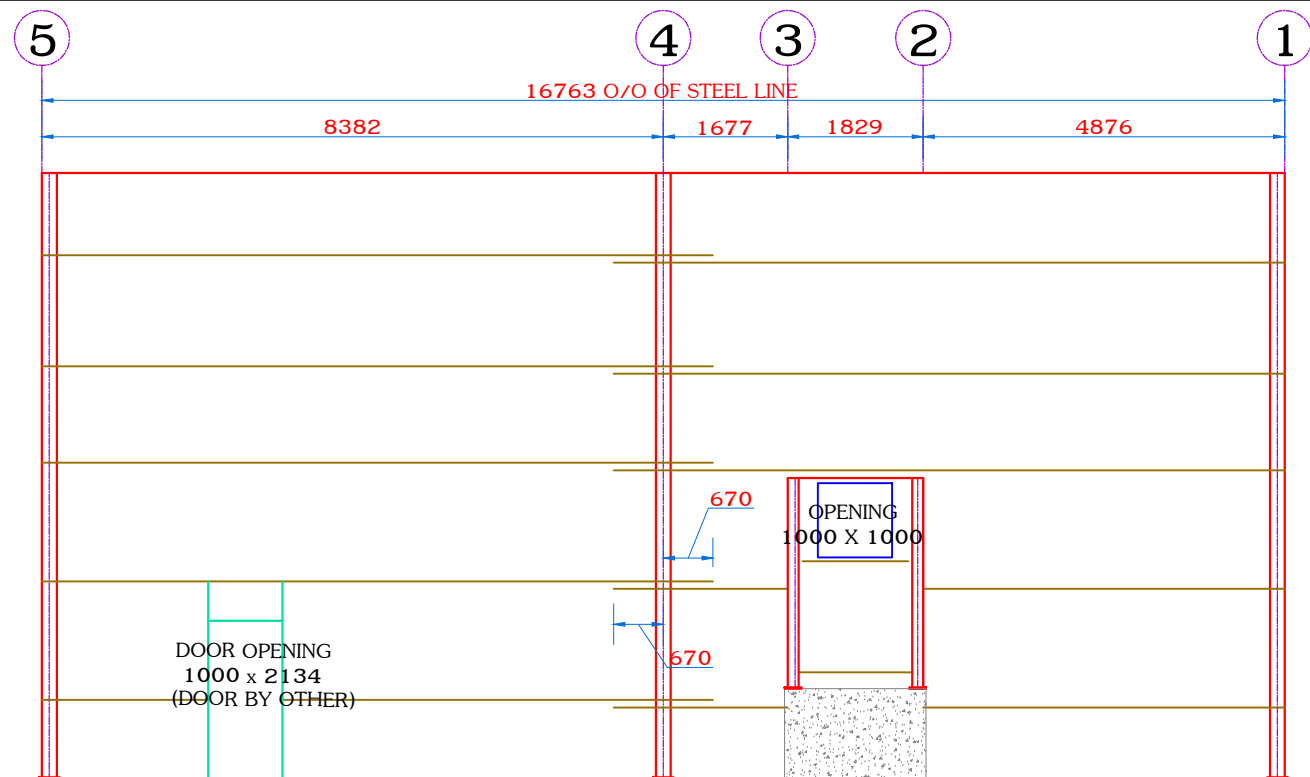

**SIDE WALL FRAMING @ GRID-A**

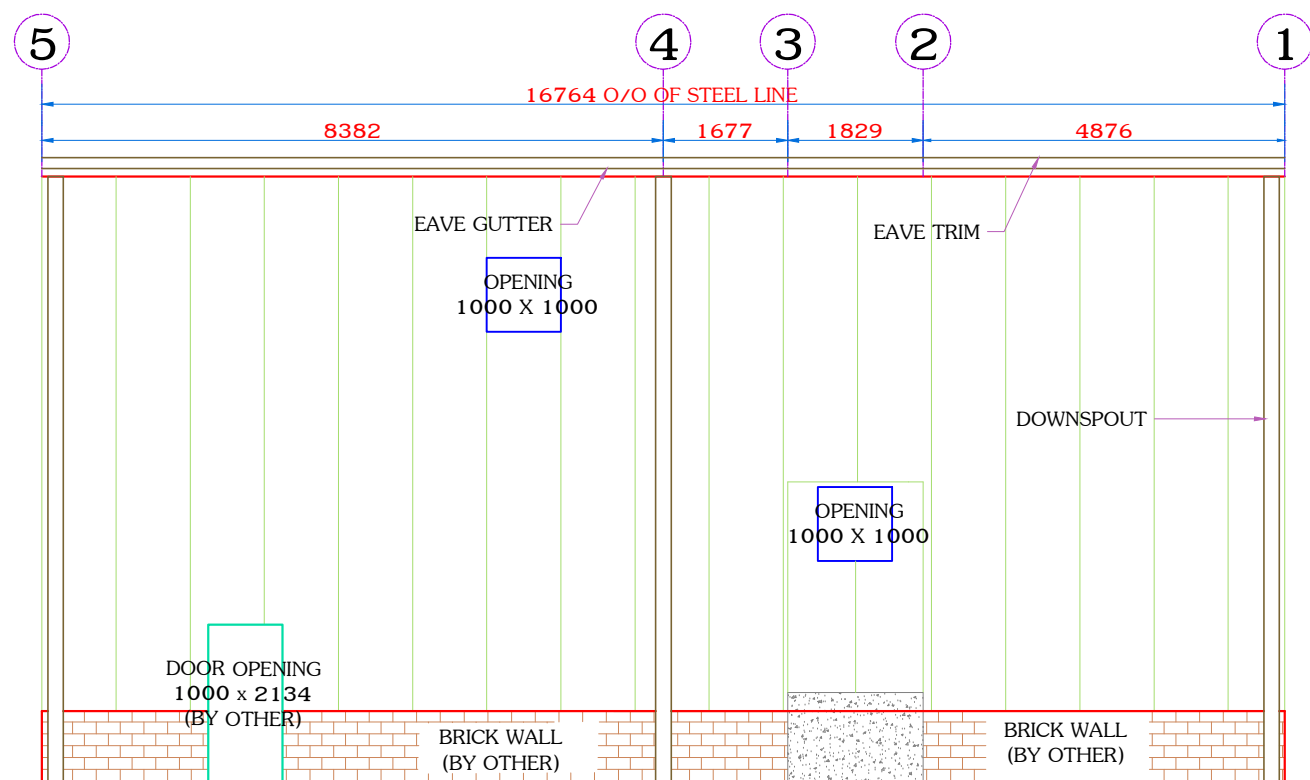

**SIDE WALL SHEETING @ GRID-A**

**NOT FOR CONSTRUCTION**

**FOR APPROVAL :**  
IN ORDER TO SCHEDULE THIS PROJECT IN AN EFFICIENT MANNER , KINDLY RETURN THESE DRAWINGS WITH YOUR COMMENTS MARKED IN RED  
APPROVAL OF THESE DRAWINGS MAY DELAY THE FABRICATION SCHEDULE AND SUBSEQUENTLY THE DELIVERY OF THE BUILDING.  
PLEASE TICK MARK ONLY ONE OF THE FOLLOWING

☐ " APPROVED AS IS "  
☐ " APPROVED AS NOTED"  
☐ " RESUBMIT AS NOTED "

APPROVE : \_\_\_\_\_  
SIGNATURE: \_\_\_\_\_  
DATE : \_\_\_\_\_

|      |         |                     |         |        |        |
|------|---------|---------------------|---------|--------|--------|
| C    |         |                     |         |        |        |
| B    |         |                     |         |        |        |
| A    | 9.03-19 | ISSUED FOR APPROVAL | AQB     | UBD    | UBD    |
| REV. | DATE    | DESCRIPTION         | DRWN BY | CHK BY | APR BY |



**MAIMAAR STEEL BUILDING Pvt.Ltd**  
105, Raiwind Road, Thokar Niaz Baig ,Lahore, Pakistan  
E-mail: nasir.abbas@maimaargroup.com  
E-mail: maimaar.steel@gmail.com  
Website: www.maimaargroup.com  
E-mail: nasir.abbas@maimaargroup.com  
Mob-1 : +(92-300) 807 4017 ,+(92-333) 807 1115

|                                       |             |         |                |
|---------------------------------------|-------------|---------|----------------|
| JOB NO./QUOTE NO.                     | MSPL-004    | BLDG #. | 01             |
| PROJECT NAME                          | BOILER SHED |         |                |
| CUSTOMER                              |             |         |                |
| JOB SITE LOCATION                     | LAHORE      |         |                |
| SIDE WALL FRAMING & SHEETING @ GRID-A |             |         | DWG. NO.<br>11 |