


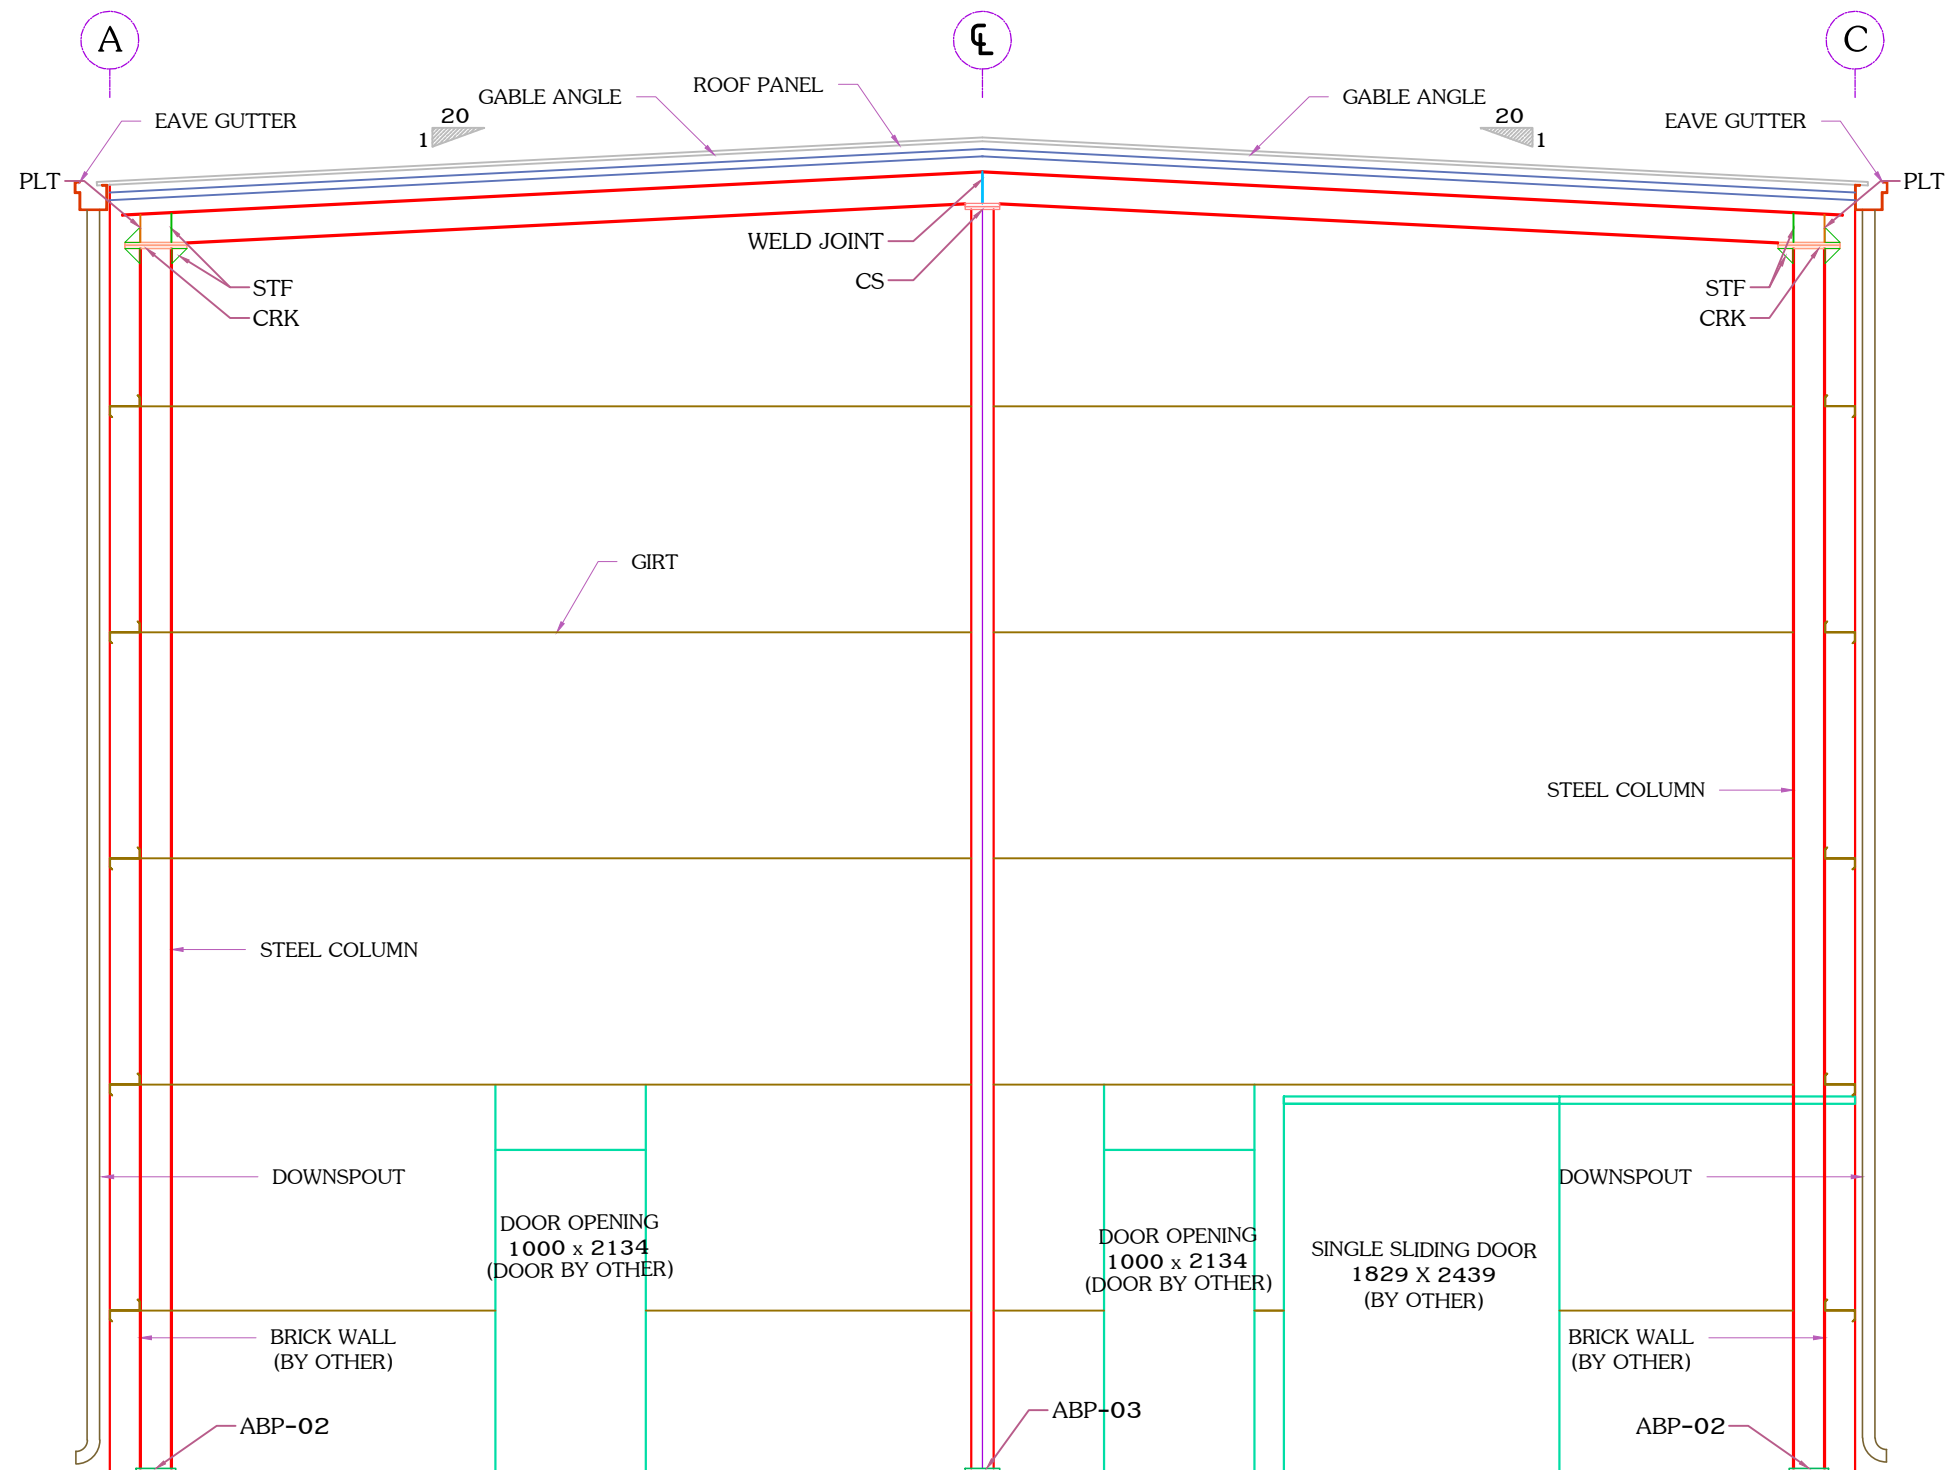

END WALL FRAMING @ GRID-1

NOT FOR CONSTRUCTION

FOR APPROVAL :
IN ORDER TO SCHEDULE THIS PROJECT IN AN EFFICIENT MANNER , KINDLY RETURN THESE DRAWINGS WITH YOUR ANY CHANGES MADE AFTER THE COMMENTS MARKED IN RED
APPROVAL OF THESE DRAWINGS MAY DELAY THE FABRICATION SCHEDULE AND SUBSEQUENTLY THE DELIVERY OF THE BUILDING.
PLEASE TICK MARK ONLY ONE OF THE FOLLOWING

C					
B					
A	9.03-19	ISSUED FOR APPROVAL	AQB	UBD	UBD
REV.	DATE	DESCRIPTION	DRWN BY	CHK BY	APR BY



MAIMAAR STEEL BUILDING Pvt.Ltd
105, Raiwind Road, Thokar Niaz Baig ,Lahore, Pakistan
E-mail: nasir.abbas@maimaargroup.com
E-mail: maimaar.steel@gmail.com
Website: www.maimaargroup.com
E-mail: nasir.abbas@maimaargroup.com
Mob-1 : +(92-300) 807 4017 ,+(92-333) 807 1115

JOB NO./QUOTE NO.	MSPL-004	BLDG #.	01
PROJECT NAME	BOILER SHED		
CUSTOMER			
JOBSITE LOCATION	LAHORE		
END WALL FRAMING @ GRID-1			DWG. NO.
			13