


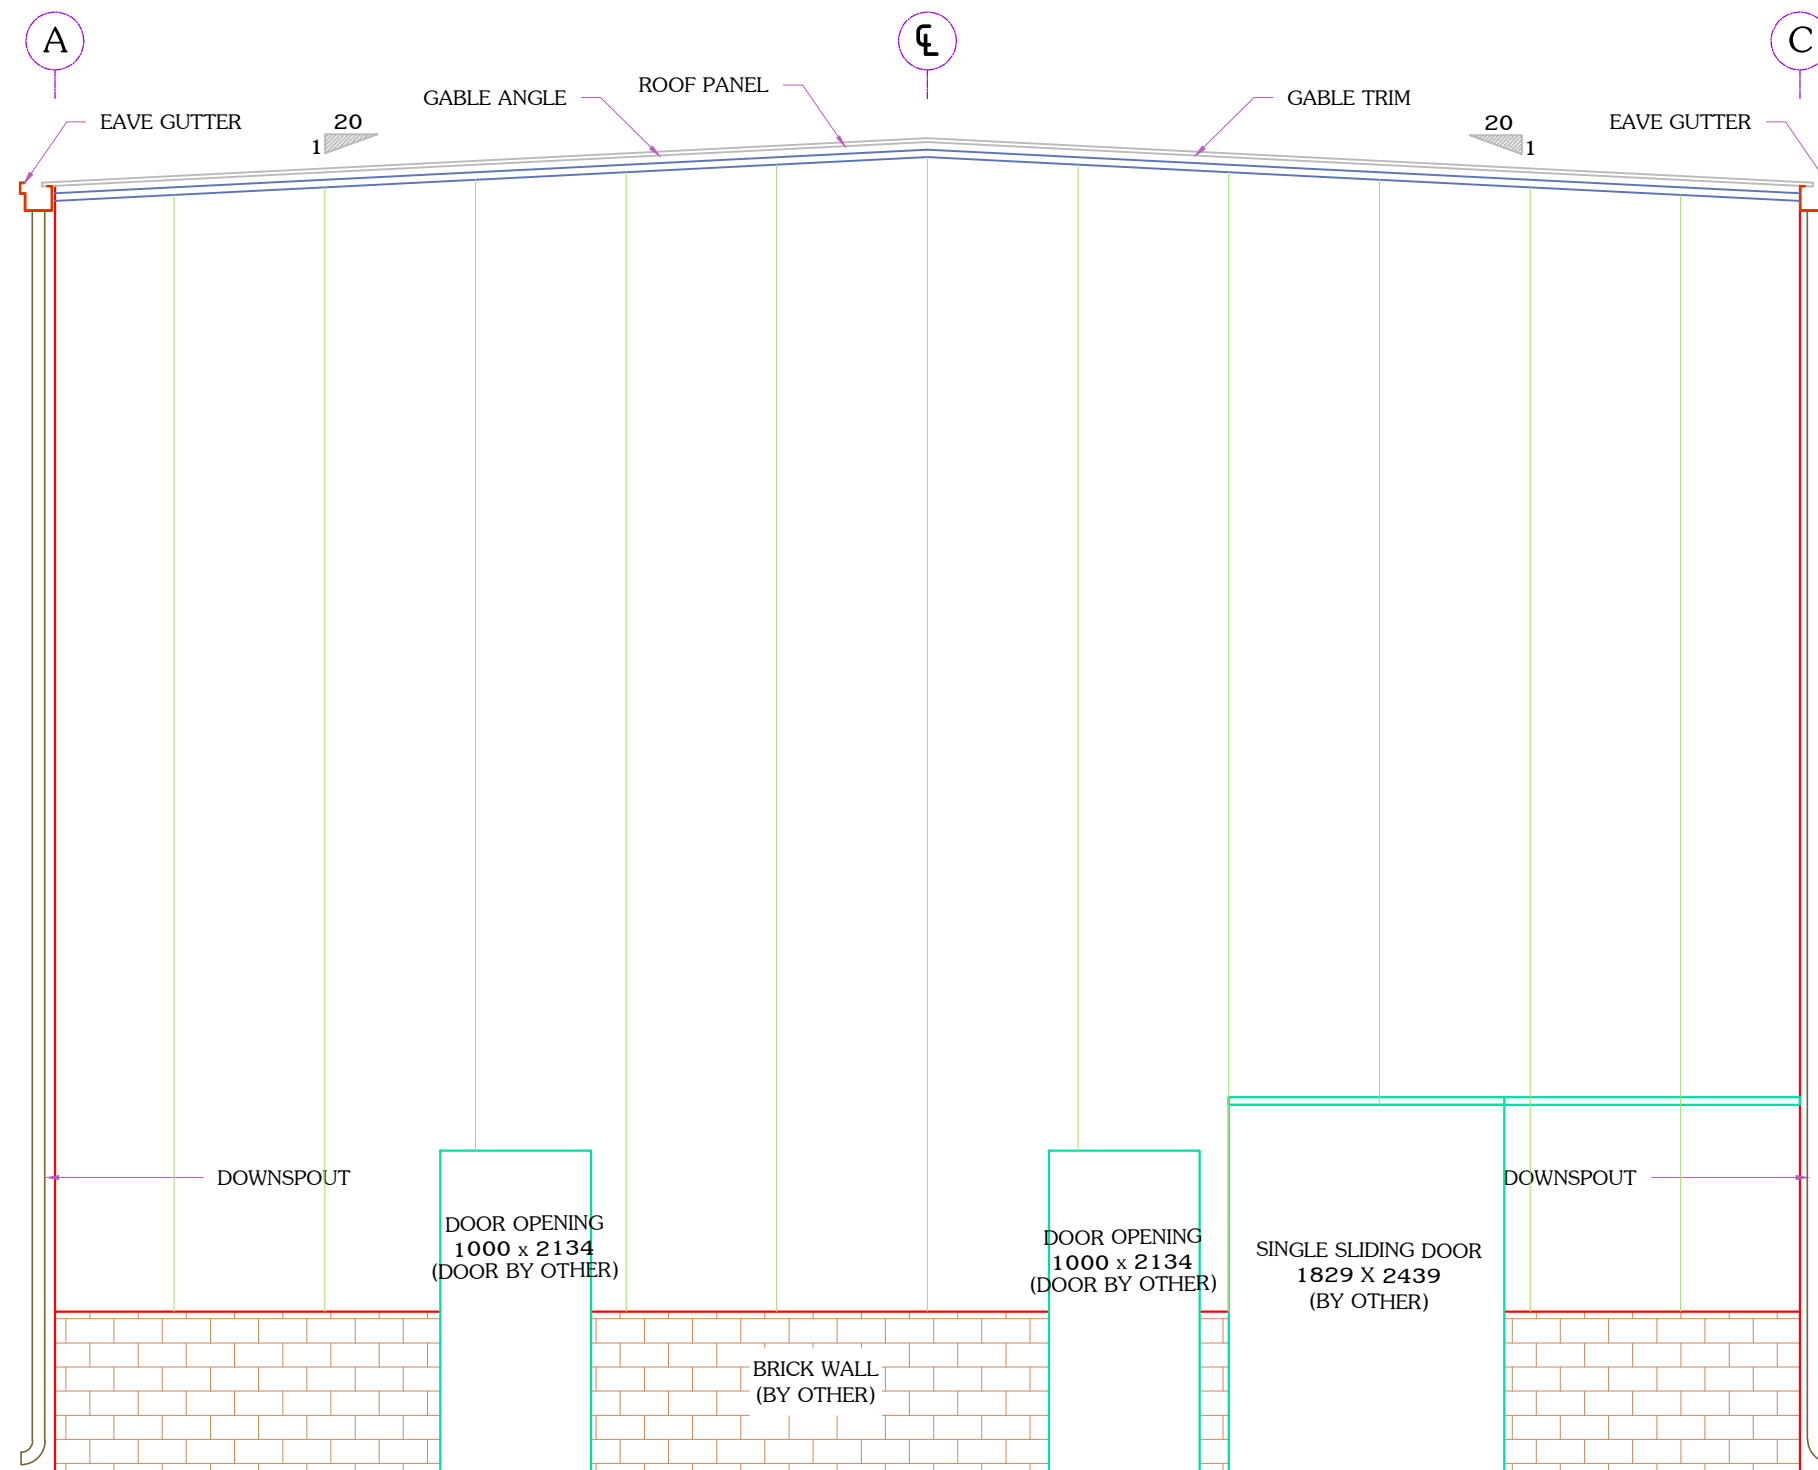

END WALL SHEETING @ GRID-1

NOT FOR CONSTRUCTION

FOR APPROVAL :
IN ORDER TO SCHEDULE THIS PROJECT IN AN EFFICIENT MANNER , KINDLY RETURN THESE DRAWINGS WITH YOUR ANY CHANGES MADE AFTER THE COMMENTS MARKED IN RED

☐ " APPROVED AS IS "
☐ " APPROVED AS NOTED"
☐ " RESUBMIT AS NOTED "

APPROVAL OF THESE DRAWINGS MAY DELAY THE FABRICATION SCHEDULE AND SUBSEQUENTLY THE DELIVERY OF THE BUILDING.

APPROVE : _____
SIGNATURE: _____
DATE : _____

PLEASE TICK MARK ONLY ONE OF THE FOLLOWING

C					
B					
A	9.03-19	ISSUED FOR APPROVAL	AQB	UBD	UBD
REV.	DATE	DESCRIPTION	DRWN BY	CHK BY	APR BY



MAIMAAR STEEL BUILDING Pvt.Ltd
105, Raiwind Road, Thokar Niaz Baig ,Lahore, Pakistan
E-mail: nasir.abbas@maimaargroup.com
E-mail: maimaar.steel@gmail.com
Website: www.maimaargroup.com
E-mail: nasir.abbas@maimaargroup.com
Mob-1 : +(92-300) 807 4017 ,+(92-333) 807 1115

JOB NO./QUOTE NO.	MSPL-004	BLDG #.	01
PROJECT NAME	BOILER SHED		
CUSTOMER			
JOB SITE LOCATION	LAHORE		
END WALL SHEETING @ GRID-1			DWG. NO.
			14