



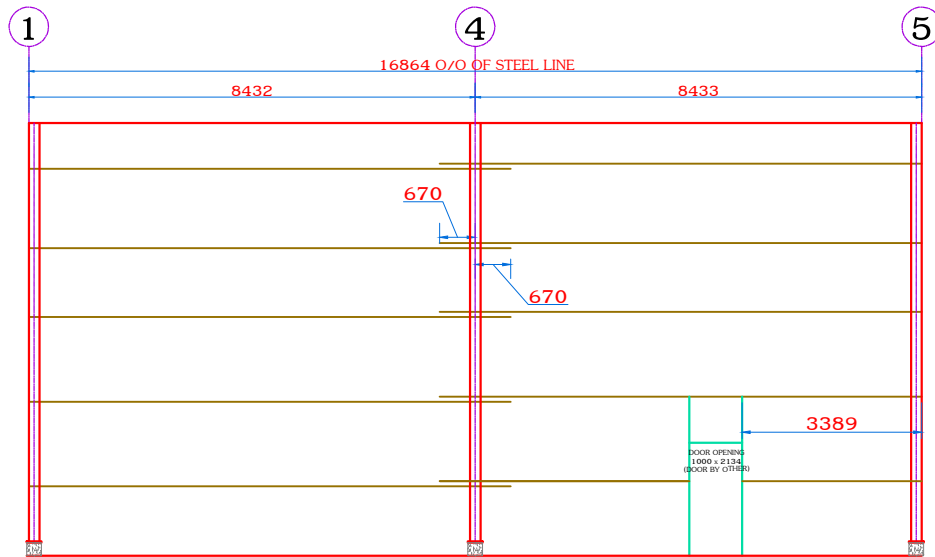

SIDE WALL FRAMING @ GRID-C

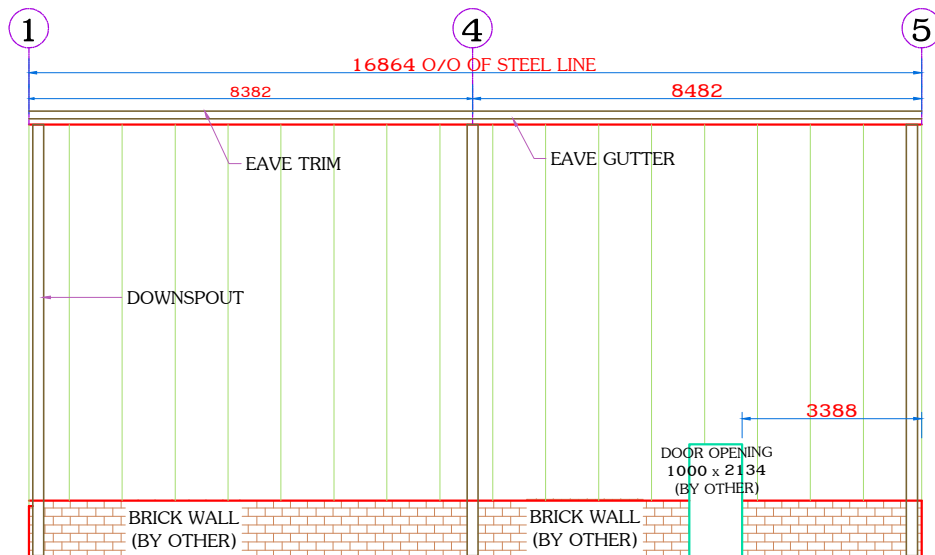

SIDE WALL SHEETING @ GRID-C

NOT FOR CONSTRUCTION

FOR APPROVAL :

IN ORDER TO SCHEDULE THIS PROJECT IN AN EFFICIENT MANNER, KINDLY RETURN THESE DRAWINGS WITH YOUR COMMENTS MARKED IN RED. APPROVAL OF THESE DRAWINGS MAY DELAY THE FABRICATION SCHEDULE AND SUBSEQUENTLY THE DELIVERY OF THE BUILDING.

☐ " APPROVED AS IS "
☐ " APPROVED AS NOTED "
☐ " RESUBMIT AS NOTED "

PLEASE TICK MARK ONLY ONE OF THE FOLLOWING

REV.	DATE	DESCRIPTION	DRWN BY	CHK BY	APR BY
C					
B	18.03-19	ISSUED FOR APPROVAL	AQB	UBD	UBD
A	9.03-19	ISSUED FOR APPROVAL	AQB	UBD	UBD



MAIMAAR STEEL Pvt.Ltd
105, Raiwind Road, Thokar Niaz Baig, Lahore, Pakistan
E-mail: nasir.abbas@maimaargroup.com
E-mail: maimaar.steel@gmail.com
Website: www.maimaargroup.com
E-mail: nasir.abbas@maimaargroup.com
Mob-1 : +(92-300) 807 4017, +(92-333) 807 1115

JOB NO./QUOTE NO.	MSPL-004	BLDG #.	01
PROJECT NAME	BOILER SHED		
CUSTOMER			
JOB SITE LOCATION	LAHORE		
SIDE WALL FRAMING & SHEETING @ GRID-C		DWG. NO.	11