


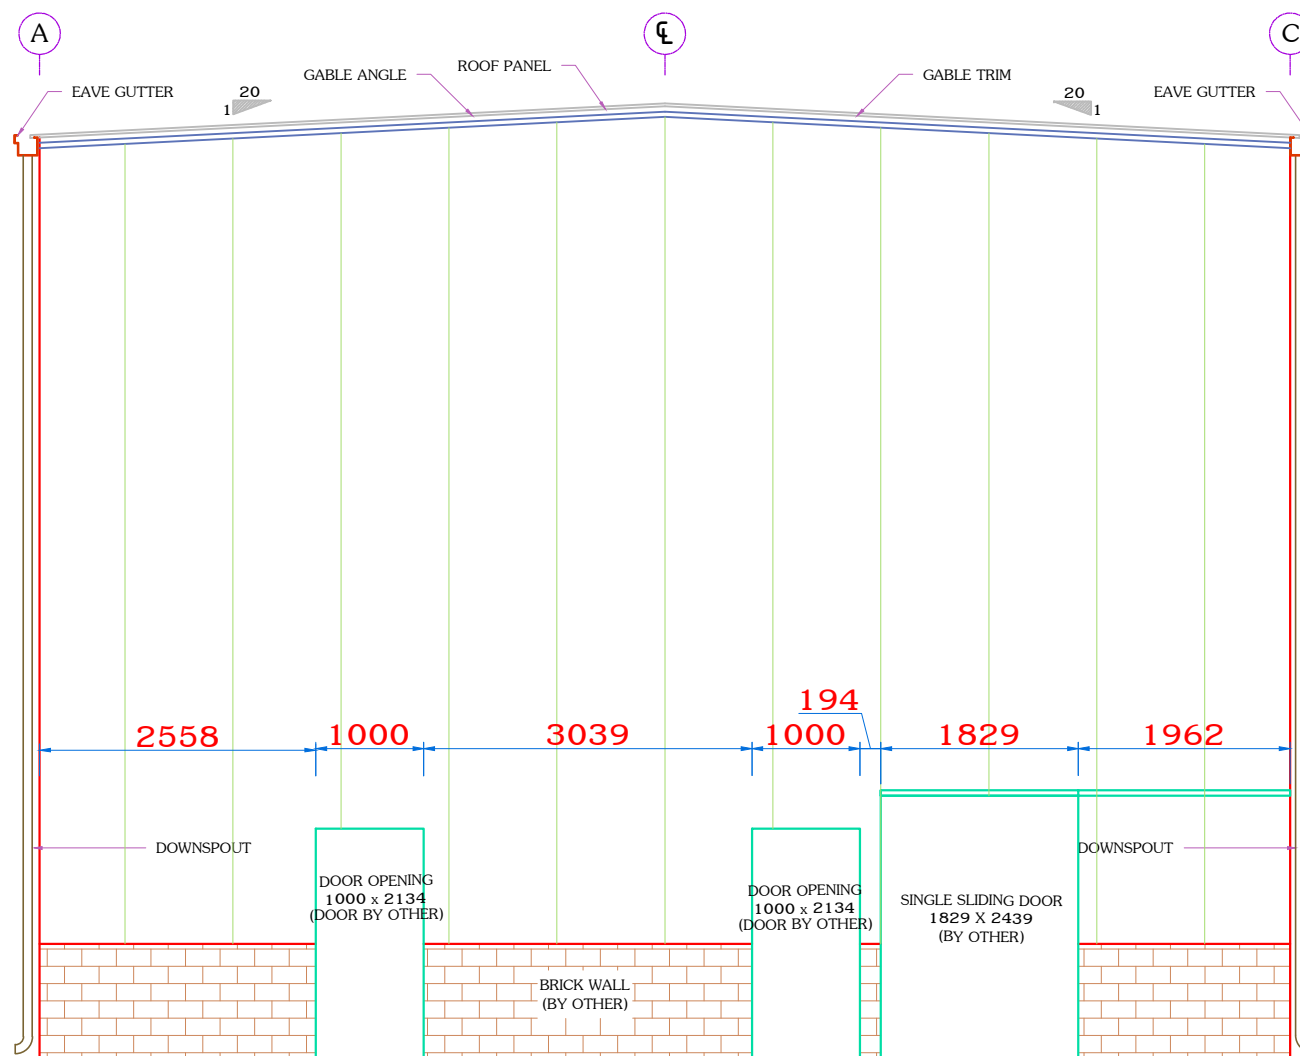

END WALL SHEETING @ GRID-1

NOT FOR CONSTRUCTION

FOR APPROVAL :

IN ORDER TO SCHEDULE THIS PROJECT IN AN EFFICIENT MANNER, KINDLY RETURN THESE DRAWINGS WITH YOUR ANY CHANGES MADE AFTER THE COMMENTS MARKED IN RED

☐ " APPROVED AS IS "
☐ " APPROVED AS NOTED "
☐ " RESUBMIT AS NOTED "

APPROVAL OF THESE DRAWINGS MAY DELAY THE FABRICATION SCHEDULE AND SUBSEQUENTLY THE DELIVERY OF THE BUILDING.

APPROVE : _____
 SIGNATURE : _____
 DATE : _____

PLEASE TICK MARK ONLY ONE OF THE FOLLOWING

C					
B	18.03-19	ISSUED FOR APPROVAL	AQB	UBD	UBD
A	9.03-19	ISSUED FOR APPROVAL	AQB	UBD	UBD
REV.	DATE	DESCRIPTION	DRWN BY	CHK BY	APR BY



MAIMAAR STEEL Pvt.Ltd
 105, Raiwind Road, Thokar Niaz Baig, Lahore, Pakistan
 E-mail: nasir.abbas@maimaargroup.com
 E-mail: maimaar.steel@gmail.com
 Website: www.maimaargroup.com
 E-mail: nasir.abbas@maimaargroup.com
 Mob-1 : +(92-300) 807 4017, +(92-333) 807 1115

JOB NO./QUOTE NO.	MSPL-004	BLDG #	01
PROJECT NAME	BOILER SHED		
CUSTOMER			
JOBSITE LOCATION	LAHORE		
END WALL SHEETING @ GRID-1			DWG. NO. 15