


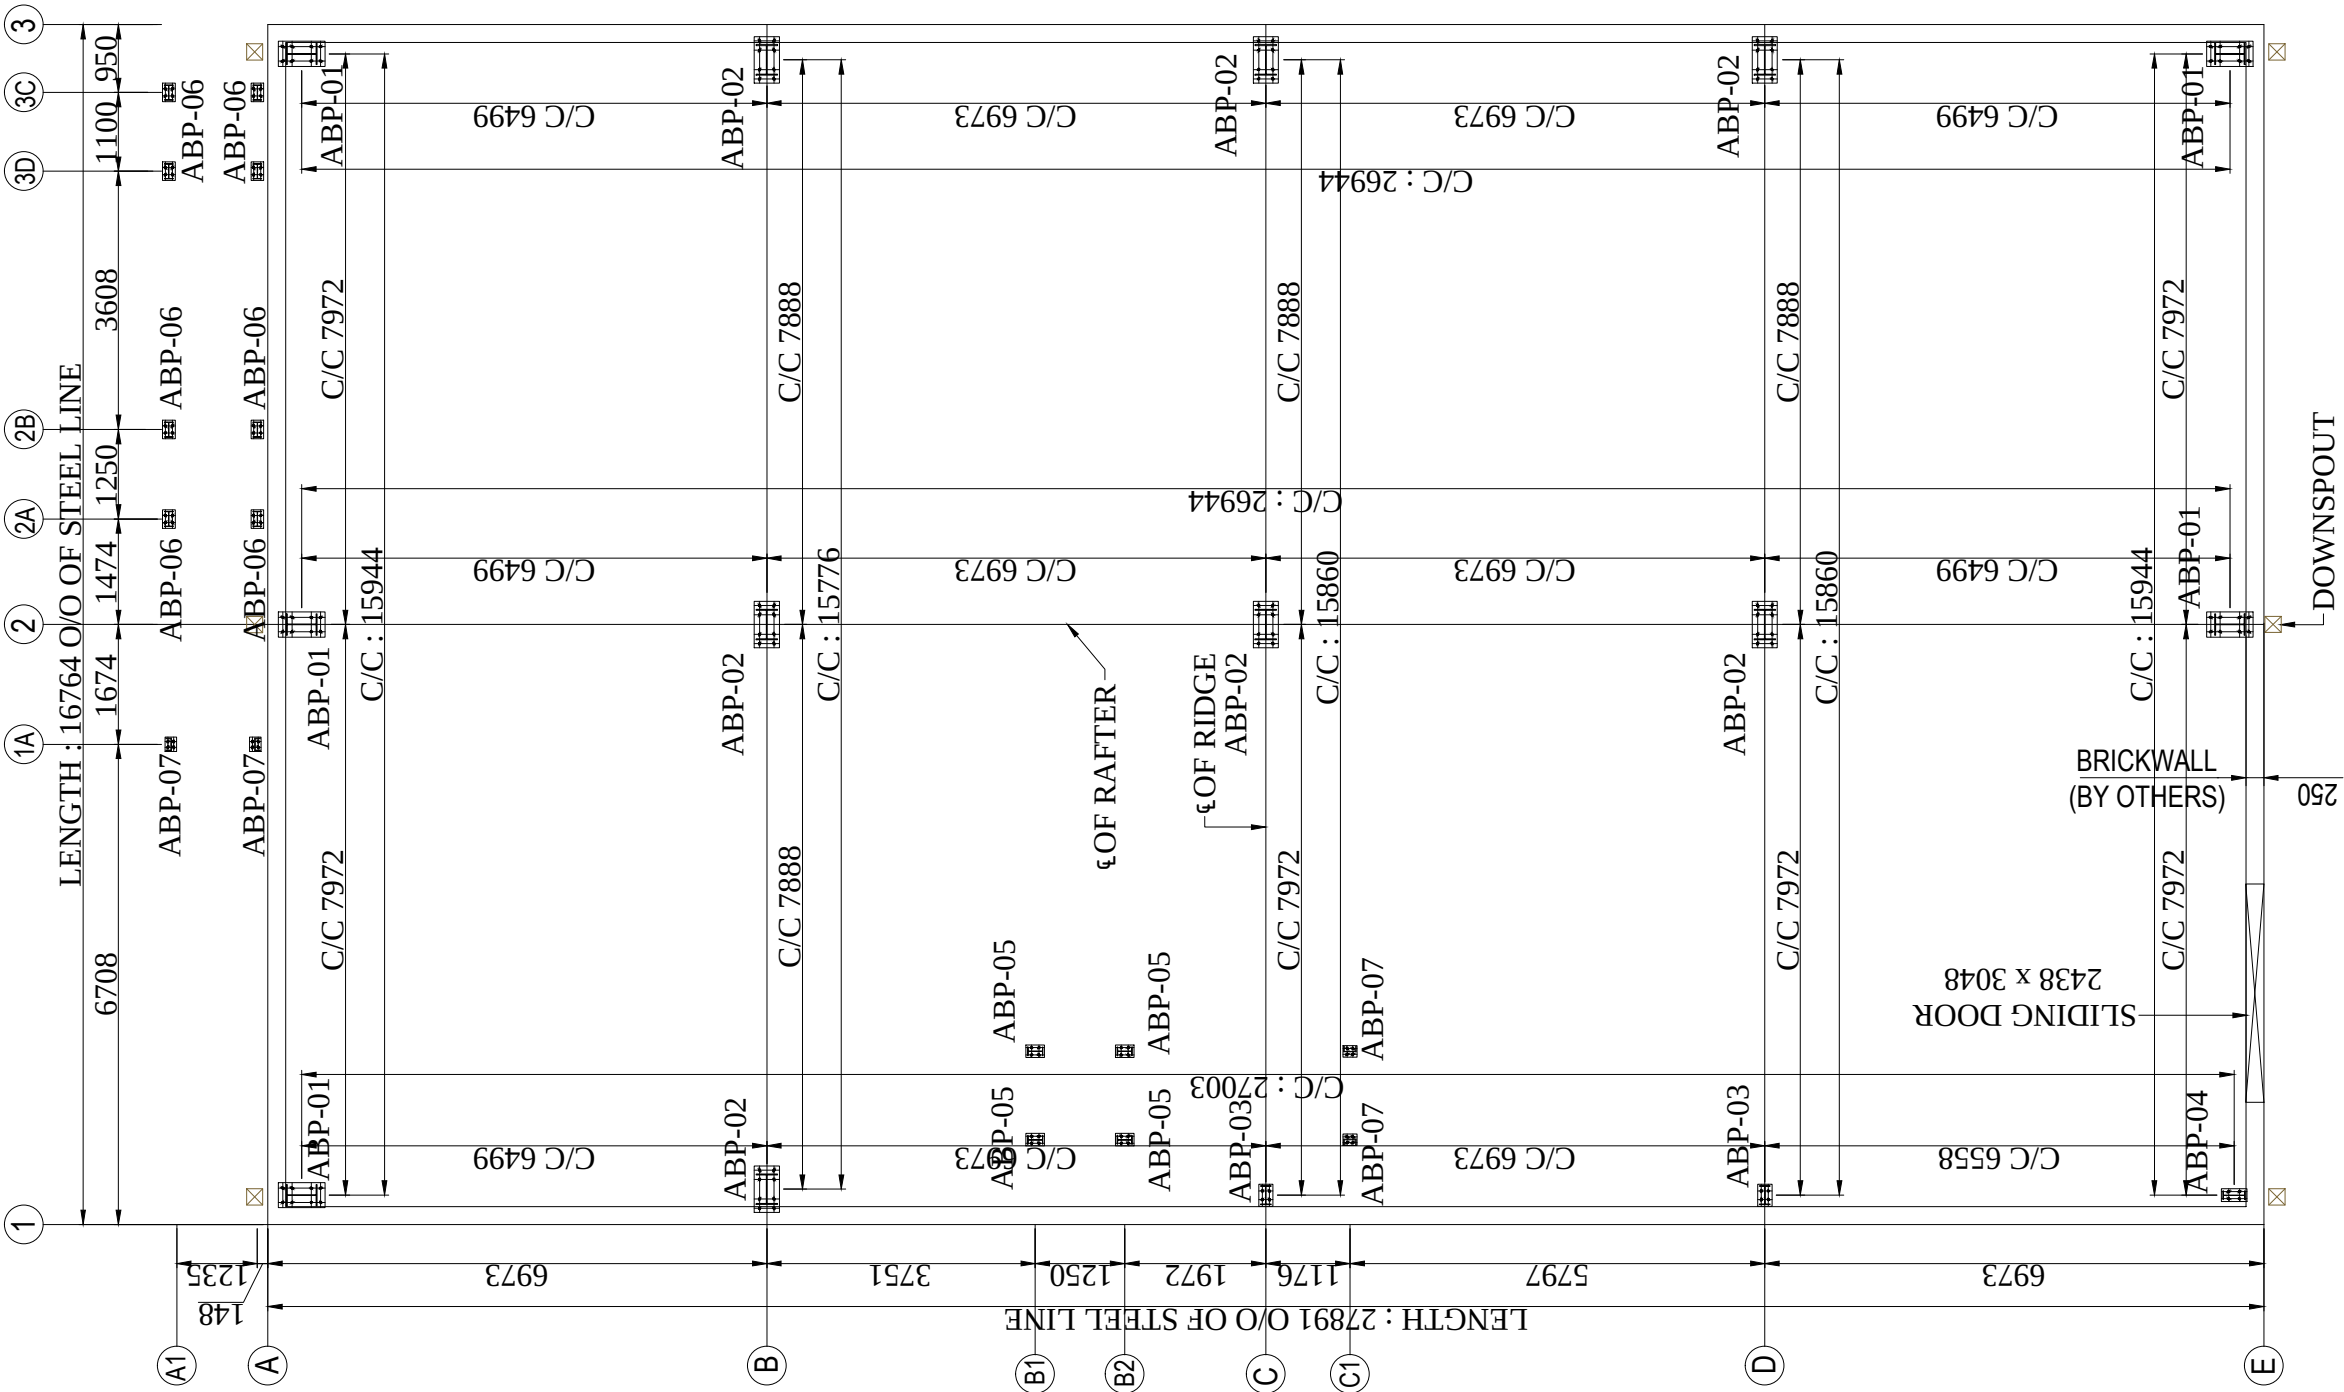

ANCHOR BOLT LAYOUT PLAN

NOTE : ALL CRITICAL DISTANCES ARE FROM ONE INNER BOLT TO OTHER INNER BOLT

FOR APPROVAL :

IN ORDER TO SCHEDULE THIS PROJECT IN AN EFFICIENT MANNER , KINDLY RETURN THESE DRAWINGS WITH YOUR ANY CHANGES MADE AFTER THE COMMENTS MARKED IN RED

APPROVAL OF THESE DRAWINGS MAY DELAY THE FABRICATION SCHEDULE AND SUBSEQUENTLY THE DELIVERY OF THE BUILDING.

PLEASE TICK MARK ONLY ONE OF THE FOLLOWINGM

☐ " APPROVED AS IS "

☐ " APPROVED AS NOTED"

☐ " RESUBMIT AS NOTED "

APPROVE : _____

SIGNATURE: _____

DATE : _____

01	19-01-22	ISSUED FOR APPROVAL	R.A	YEA	YEA
00	11-11-21	ISSUED FOR APPROVAL	R.A	YEA	YEA
REV.	DATE	DESCRIPTION	DRWN BY	CHK BY	APR BY
MAIMAAR MAIMAAR STEEL Pvt.Ltd 238, Raiwind Road, Thokar Niaz Baig ,LAHORE, Pakistan E-mail: nasir.abbas@maimaargroup.com E-mail: maimaar.steel@gmail.com Website: www.maimaargroup.com E-mail: nasir.abbas@maimaargroup.com Mob-1 : +(92-300) 807 4017 , +(92-333) 807 1115					
JOB NO./QUOTE NO.			MSPL-030		
PROJECT NAME			BLDG #. 01		
INITIAL PADDLE SANDING HALL					
CUSTOMER			AWAN SPORTS		
JOBSITE LOCATION			SIALKOT		
ANCHOR BOLT LAYOUT PLAN					DWG. NO.
					01