



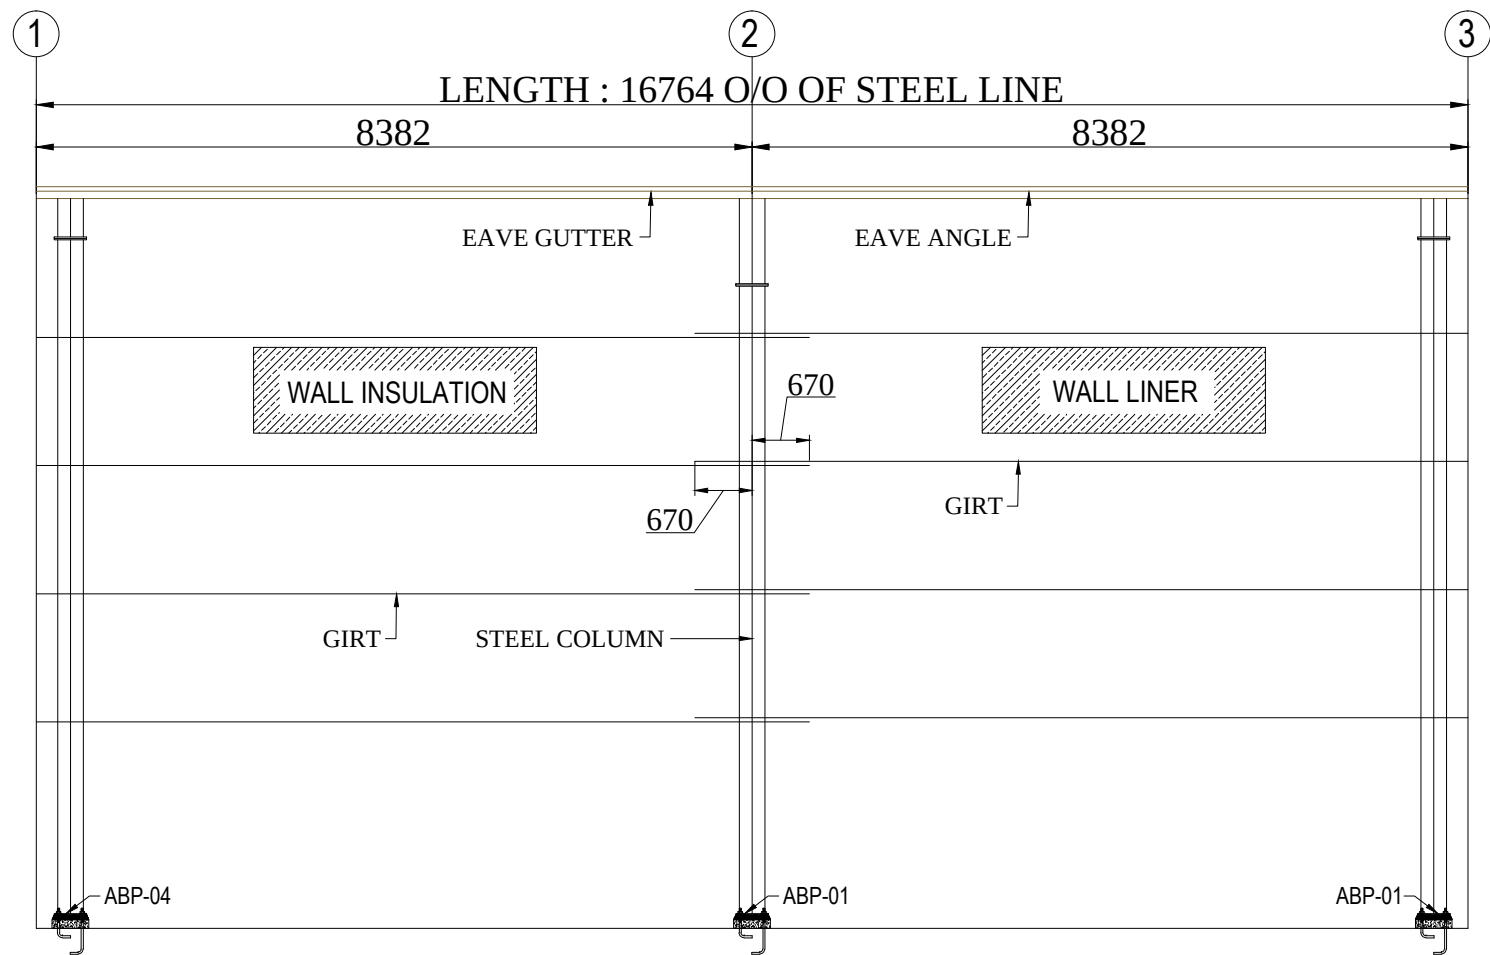

SIDE WALL FRAMING

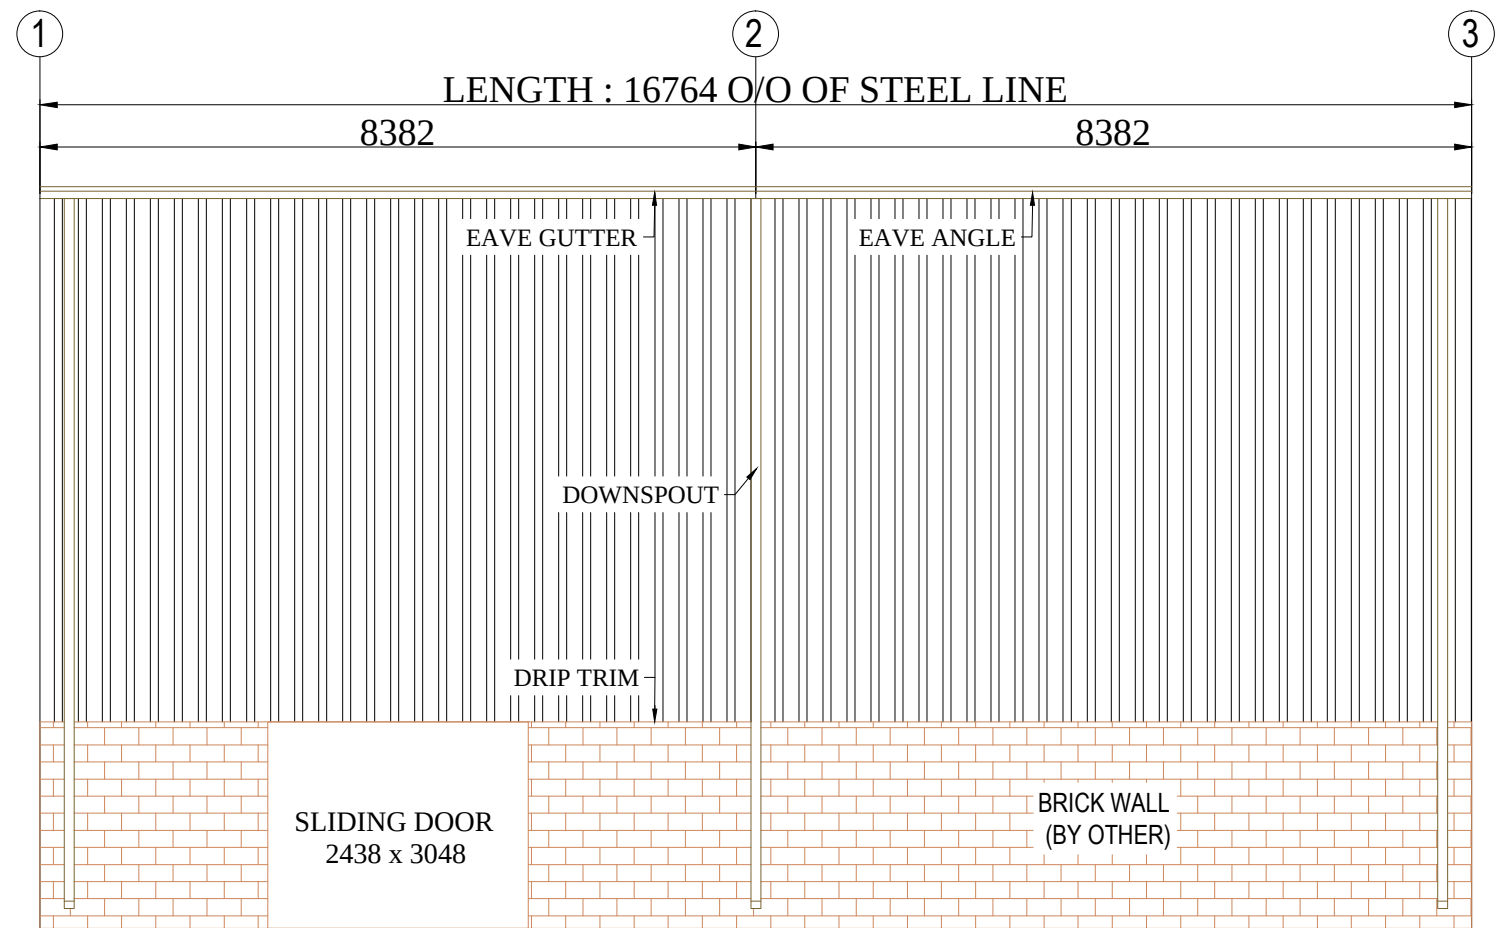

SIDE WALL SHEETING

FOR APPROVAL :

IN ORDER TO SCHEDULE THIS PROJECT
IN AN EFFICIENT MANNER , KINDLY
RETURN THESE DRAWINGS WITH YOUR
ANY CHANGES MADE AFTER THE
COMMENTS MARKED IN RED
APPROVAL OF THESE DRAWINGS MAY
DELAY THE FABRICATION SCHEDULE AND
SUBSEQUENTLY THE DELIVERY OF THE
BUILDING.
PLEASE TICK MARK ONLY ONE OF THE FOLLOWING

☐ " APPROVED AS IS "

☐ " APPROVED AS NOTED"

☐ " RESUBMIT AS NOTED "

APPROVE : _____

SIGNATURE: _____

DATE : _____

SIDE WALL @ GRID-E

01	19-01-22	ISSUED FOR APPROVAL	R.A	YEA	YEA
00	11-11-21	ISSUED FOR APPROVAL	R.A	YEA	YEA
REV.	DATE	DESCRIPTION	DRWN BY	CHK BY	APR BY
MAIMAAR MAIMAAR STEEL Pvt.Ltd 238, Raiwind Road, Thokar Niaz Baig ,LAHORE, Pakistan E-mail: nasir.abbas@maimaargroup.com E-mail: maimaar.steel@gmail.com Website: www.maimaargroup.com E-mail: nasir.abbas@maimaargroup.com Mob-1 : +(92-300) 807 4017 , +(92-333) 807 1115					
JOB NO./QUOTE NO.		MSPL-030		BLDG #. 01	
PROJECT NAME		INITIAL PADDLE SANDING HALL			
CUSTOMER		AWAN SPORTS			
JOBSITE LOCATION		SIALKOT			
SIDE WALL @ GRID E					DWG. NO. 11