




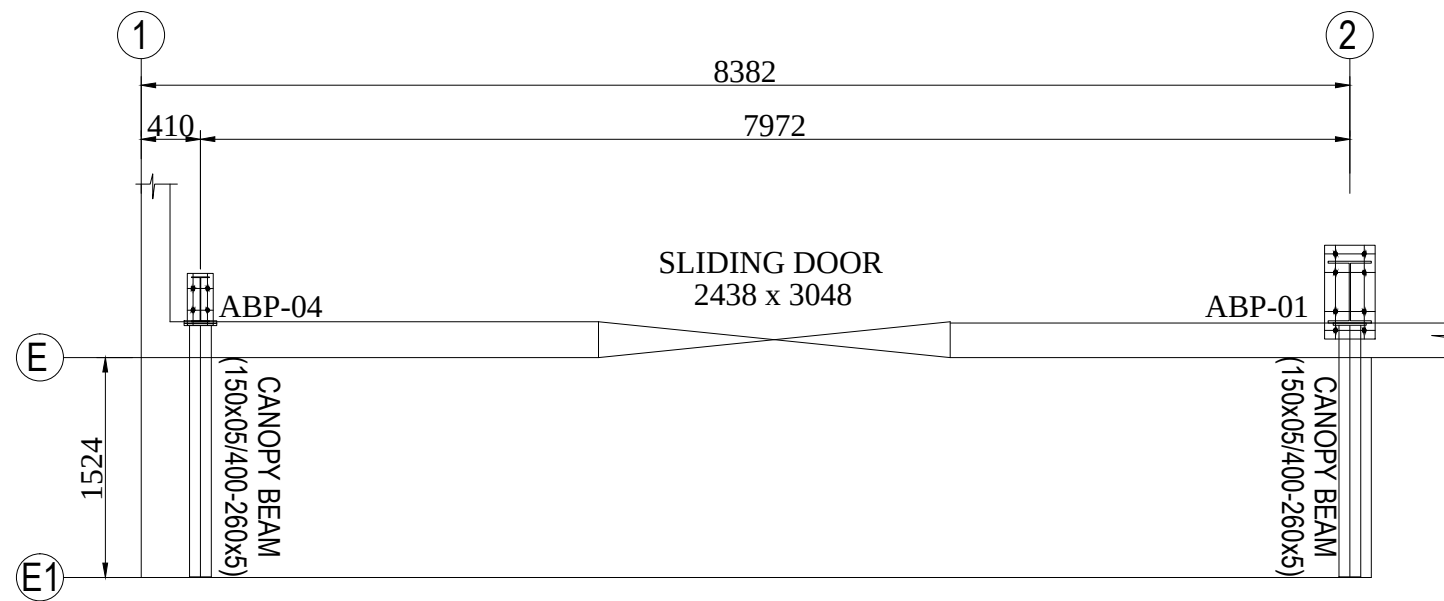

CANOPY LAYOUT PLAN

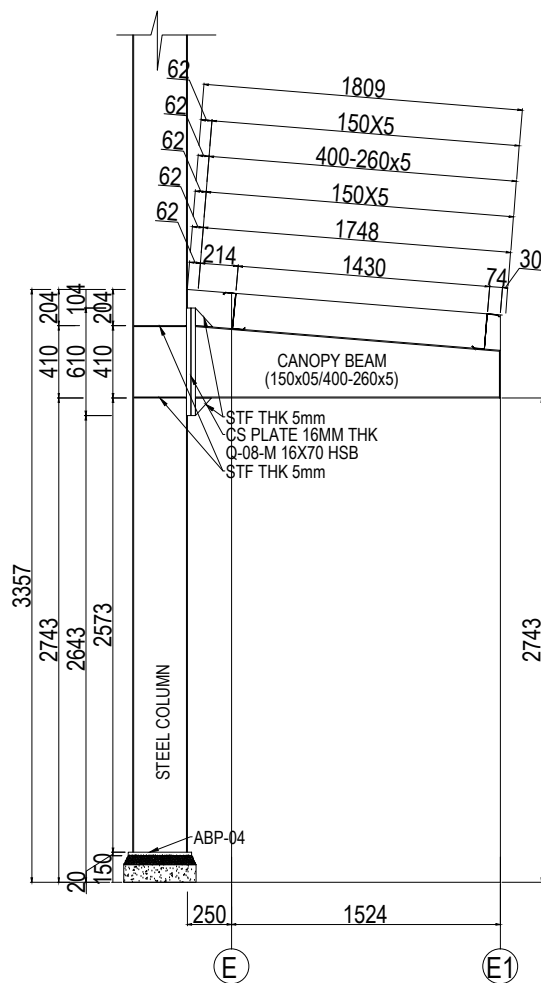

CANOPY CROSS SECTION @ 01
DETAIL (A-A)

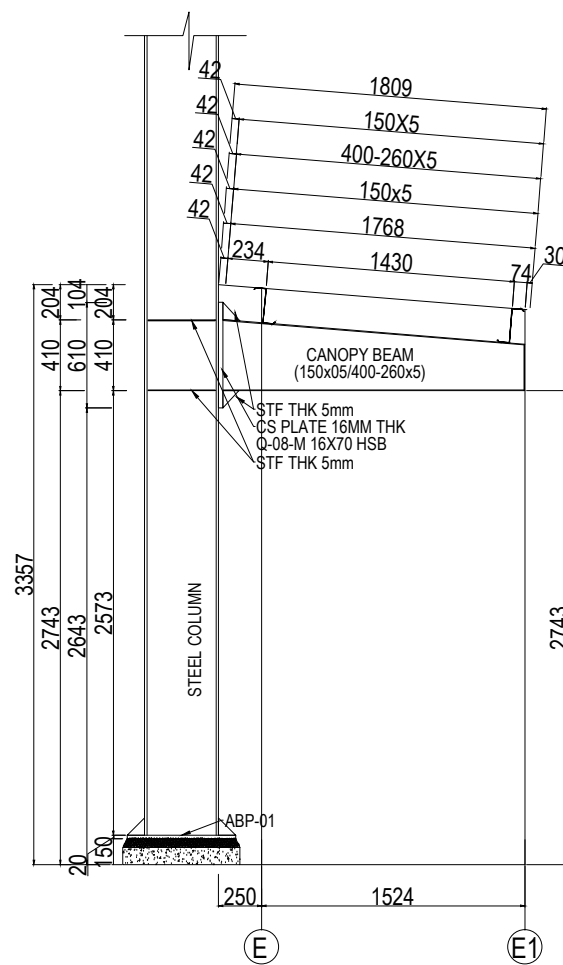

CANOPY CROSS SECTION @ 02
DETAIL (B-B)

STAIR CROSS SECTION

01	19-01-22	ISSUED FOR APPROVAL	R.A	YEA	YEA
00	11-11-21	ISSUED FOR APPROVAL	R.A	YEA	YEA
REV.	DATE	DESCRIPTION	DRWN BY	CHK BY	APR BY



MAIMAAR STEEL Pvt.Ltd
238, Raiwind Road, Thokar Niaz Baig ,LAHORE, Pakistan
E-mail: nasir.abbas@maimaargroup.com
E-mail: maimaar.steel@gmail.com
Website: www.maimaargroup.com
E-mail: nasir.abbas@maimaargroup.com
Mob-1 : +(92-300) 807 4017 , +(92-333) 807 1115

JOB NO./QUOTE NO.	MSPL-030	BLDG #.	01
PROJECT NAME	INITIAL PADDLE SANDING HALL		
CUSTOMER	AWAN SPORTS		
JOBSITE LOCATION	SIALKOT		
STAIR 02 PLAN AND SECTION			DWG. NO. 18

FOR APPROVAL :

IN ORDER TO SCHEDULE THIS PROJECT
IN AN EFFICIENT MANNER , KINDLY
RETURN THESE DRAWINGS WITH YOUR
ANY CHANGES MADE AFTER THE
COMMENTS MARKED IN RED

- ☐ " APPROVED AS IS "
☐ " APPROVED AS NOTED"
☐ " RESUBMIT AS NOTED "

APPROVAL OF THESE DRAWINGS MAY
DELAY THE FABRICATION SCHEDULE AND
SUBSEQUENTLY THE DELIVERY OF THE
BUILDING.

APPROVE : _____

SIGNATURE: _____

DATE : _____

PLEASE TICK MARK ONLY ONE OF THE FOLLOWING