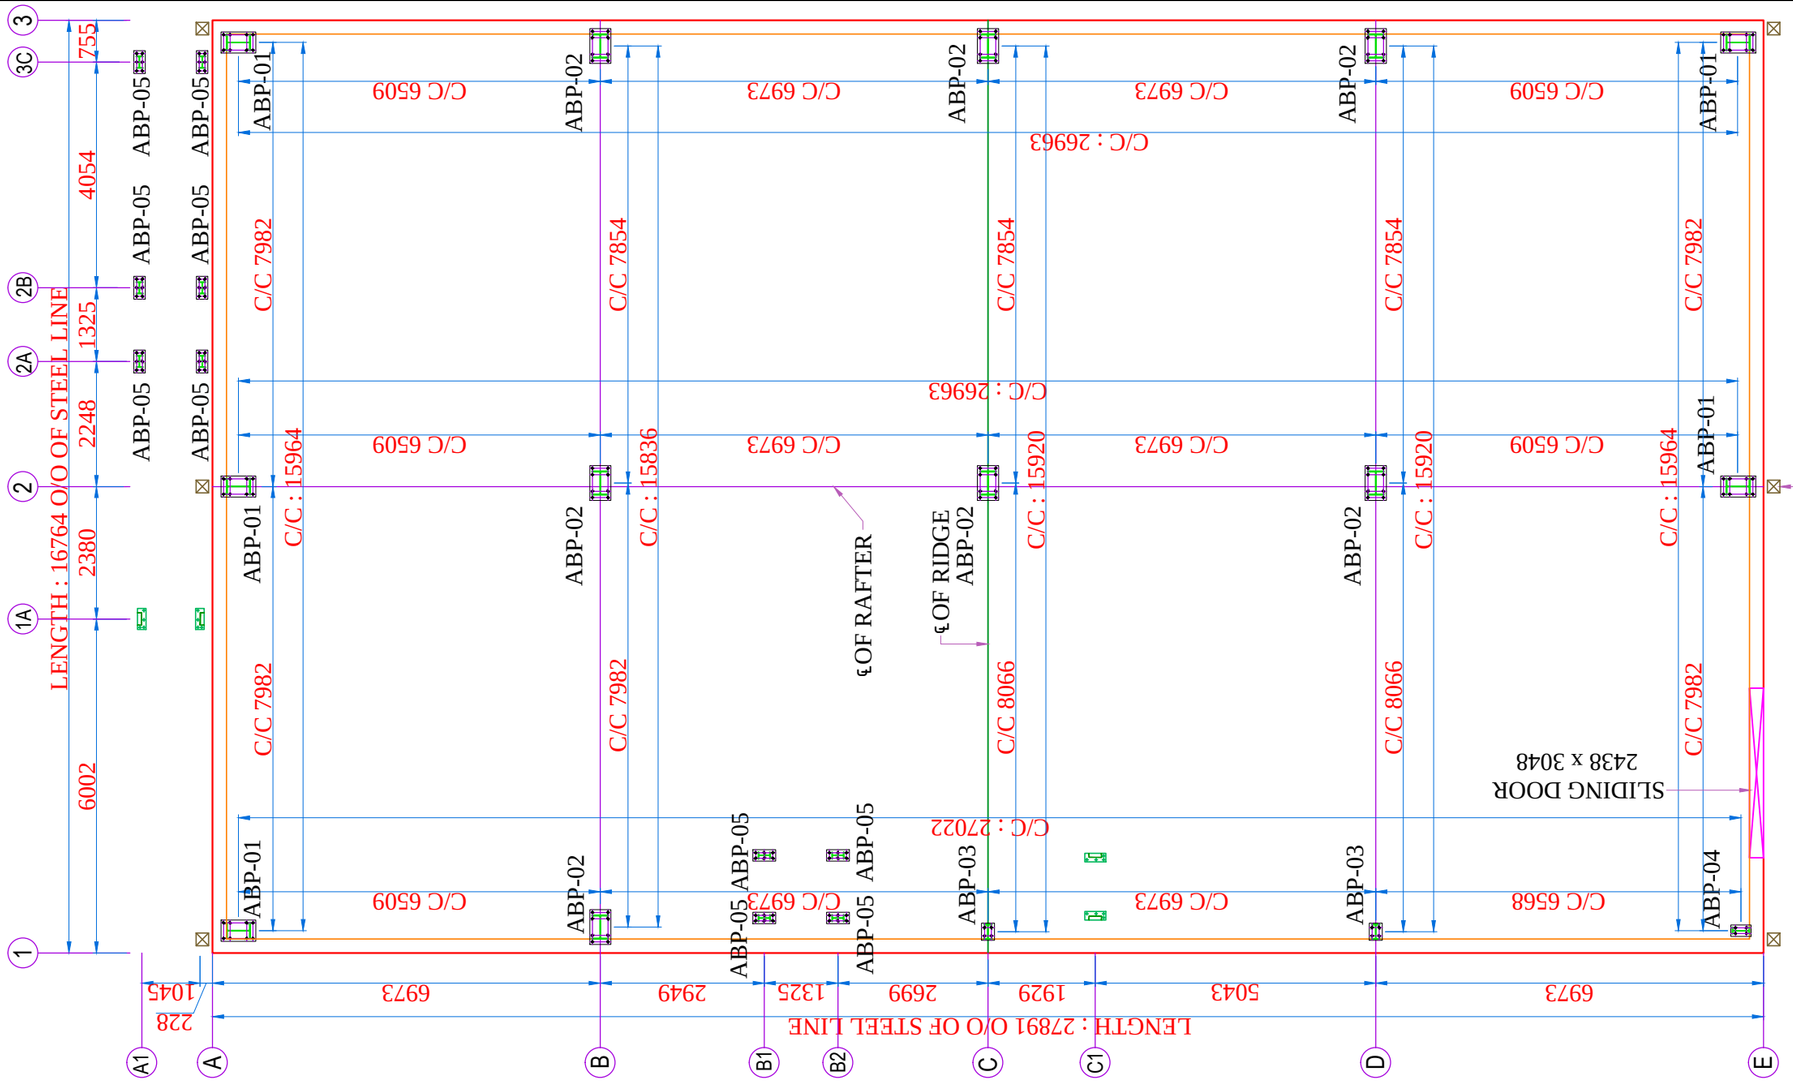

ANCHOR BOLT LAYOUT PLAN

NOTE : ALL CRITICAL DISTANCES ARE FROM ONE INNER BOLT TO OTHER INNER BOLT

REV.	DATE	DESCRIPTION	DRWN BY	CHK BY	APR BY
00	11-11-21	ISSUED FOR APPROVAL	R.A	YEA	YEA

MAIMAAR STEEL Pvt.Ltd
238, Raiwind Road, Thokar Niaz Baig ,LAHORE, Pakistan
E-mail: nasir.abbas@maimaargroup.com
E-mail: maimaar.steel@gmail.com
Website: www.maimaargroup.com
E-mail: nasir.abbas@maimaargroup.com
Mob-1 : +(92-300) 807 4017 ,+(92-333) 807 1115

JOB NO./QUOTE NO.	MSPL-030	BLDG #.	01
PROJECT NAME	INITIAL PADDLE SANDING HALL		
CUSTOMER	AWAN SPORTS		
JOBSITE LOCATION	SIALKOT		
ANCHOR BOLT LAYOUT PLAN		DWG. NO.	01

FOR APPROVAL :

IN ORDER TO SCHEDULE THIS PROJECT IN AN EFFICIENT MANNER , KINDLY RETURN THESE DRAWINGS WITH YOUR ANY CHANGES MADE AFTER THE COMMENTS MARKED IN RED
APPROVAL OF THESE DRAWINGS MAY DELAY THE FABRICATION SCHEDULE AND SUBSEQUENTLY THE DELIVERY OF THE BUILDING.
PLEASE TICK MARK ONLY ONE OF THE FOLLOWIMG

☐ " APPROVED AS IS "
☐ " APPROVED AS NOTED"
☐ " RESUBMIT AS NOTED "

APPROVE : _____
SIGNATURE: _____
DATE : _____