



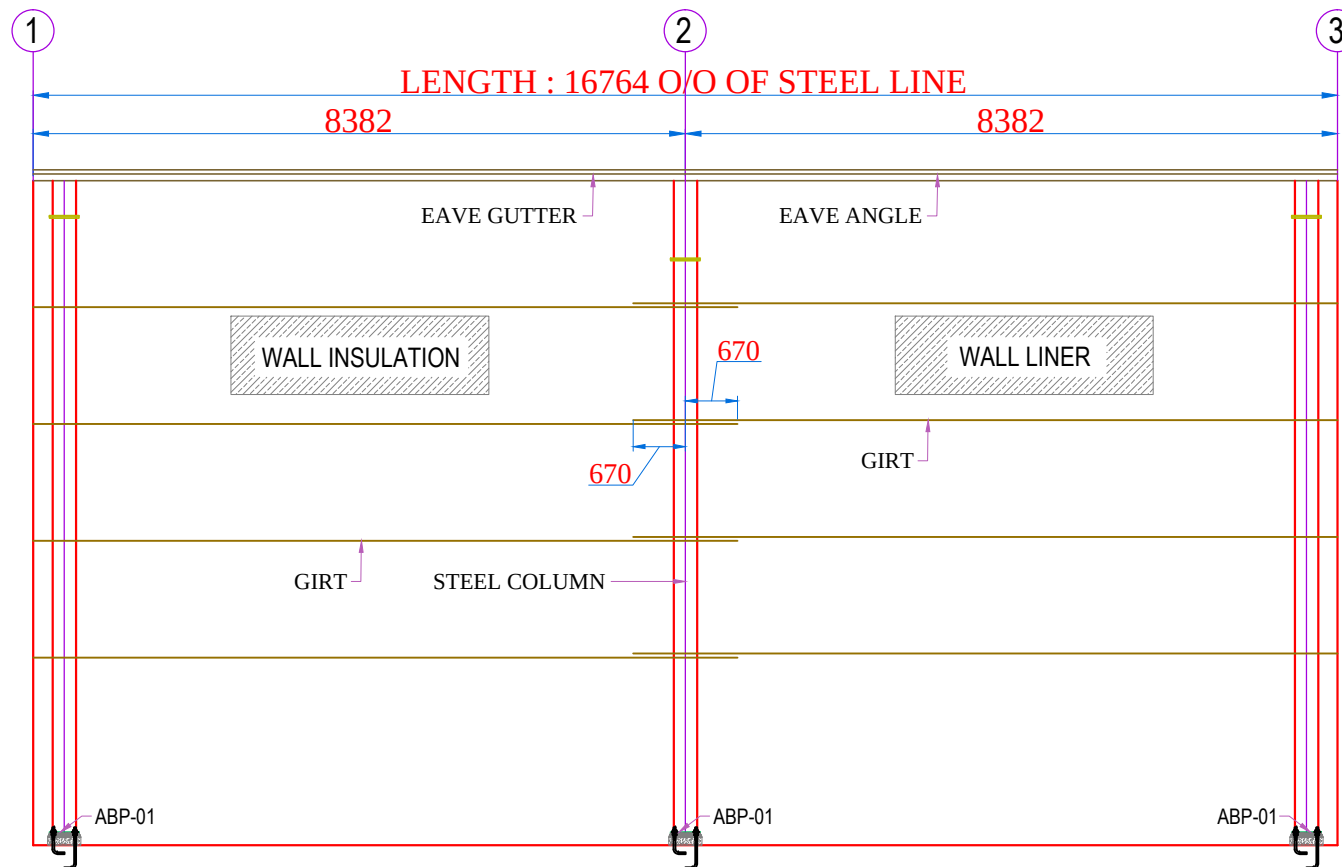

SIDE WALL FRAMING

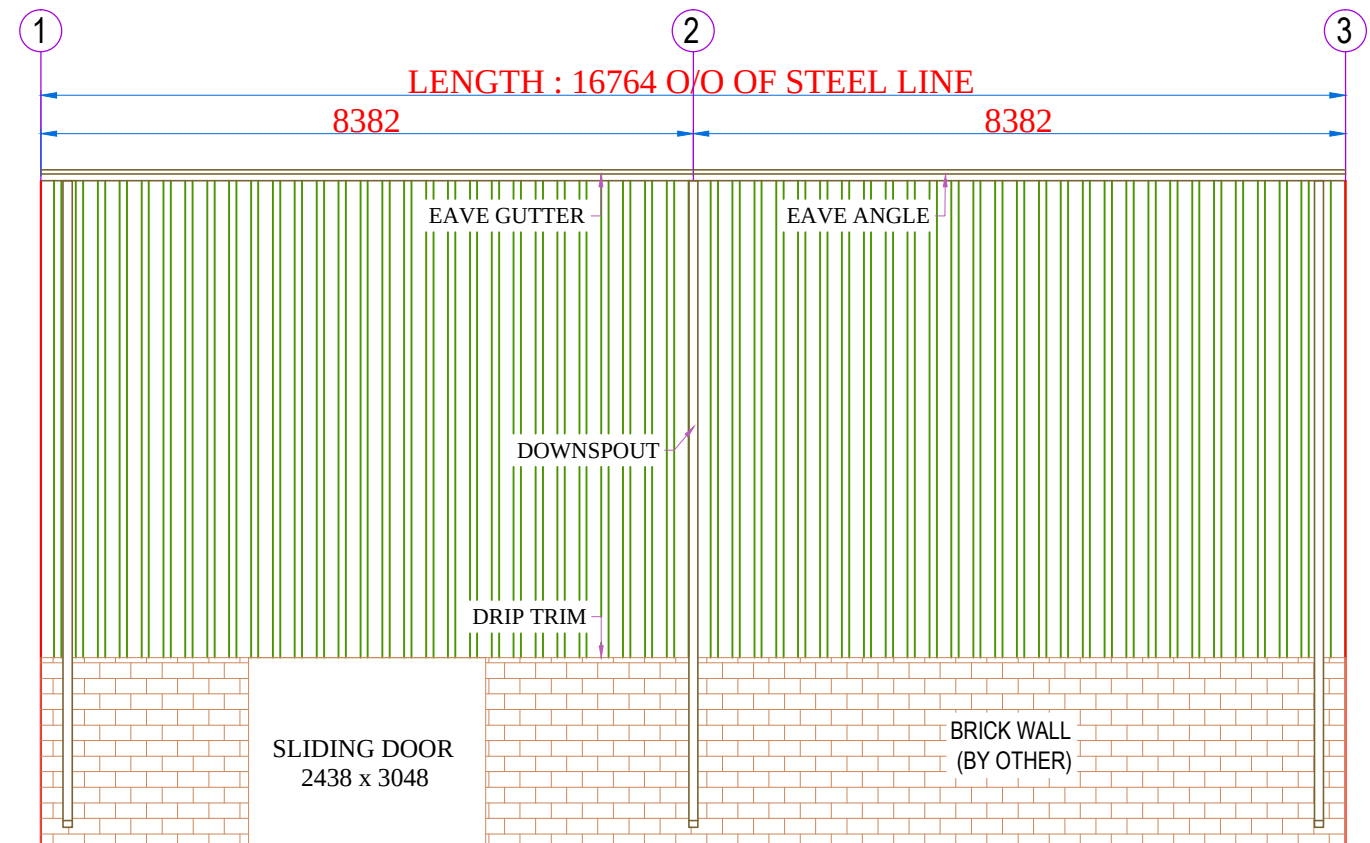

SIDE WALL SHEETING

SIDE WALL @ GRID-E

00	11-11-21	ISSUED FOR APPROVAL	R.A	YEA	YEA
REV.	DATE	DESCRIPTION	DRWN BY	CHK BY	APR BY
MAIMAAR STEEL Pvt.Ltd 238, Raiwind Road, Thokar Niaz Baig ,LAHORE, Pakistan E-mail: nasir.abbas@maimaargroup.com E-mail: maimaar.steel@gmail.com Website: www.maimaargroup.com E-mail: nasir.abbas@maimaargroup.com Mob-1 : +(92-300) 807 4017 ,+(92-333) 807 1115					
JOB NO./QUOTE NO.		MSPL-030		BLDG #.	01
PROJECT NAME		INITIAL PADDLE SANDING HALL			
CUSTOMER		AWAN SPORTS			
JOBSITE LOCATION		SIALKOT			
SIDE WALL @ GRID E					DWG. NO.
					11

FOR APPROVAL :

IN ORDER TO SCHEDULE THIS PROJECT IN AN EFFICIENT MANNER , KINDLY RETURN THESE DRAWINGS WITH YOUR ANY CHANGES MADE AFTER THE COMMENTS MARKED IN RED

- ☐ " APPROVED AS IS "
☐ " APPROVED AS NOTED"
☐ " RESUBMIT AS NOTED "

APPROVAL OF THESE DRAWINGS MAY DELAY THE FABRICATION SCHEDULE AND SUBSEQUENTLY THE DELIVERY OF THE BUILDING.

APPROVE : _____
SIGNATURE: _____
DATE : _____

PLEASE TICK MARK ONLY ONE OF THE FOLLOWING