



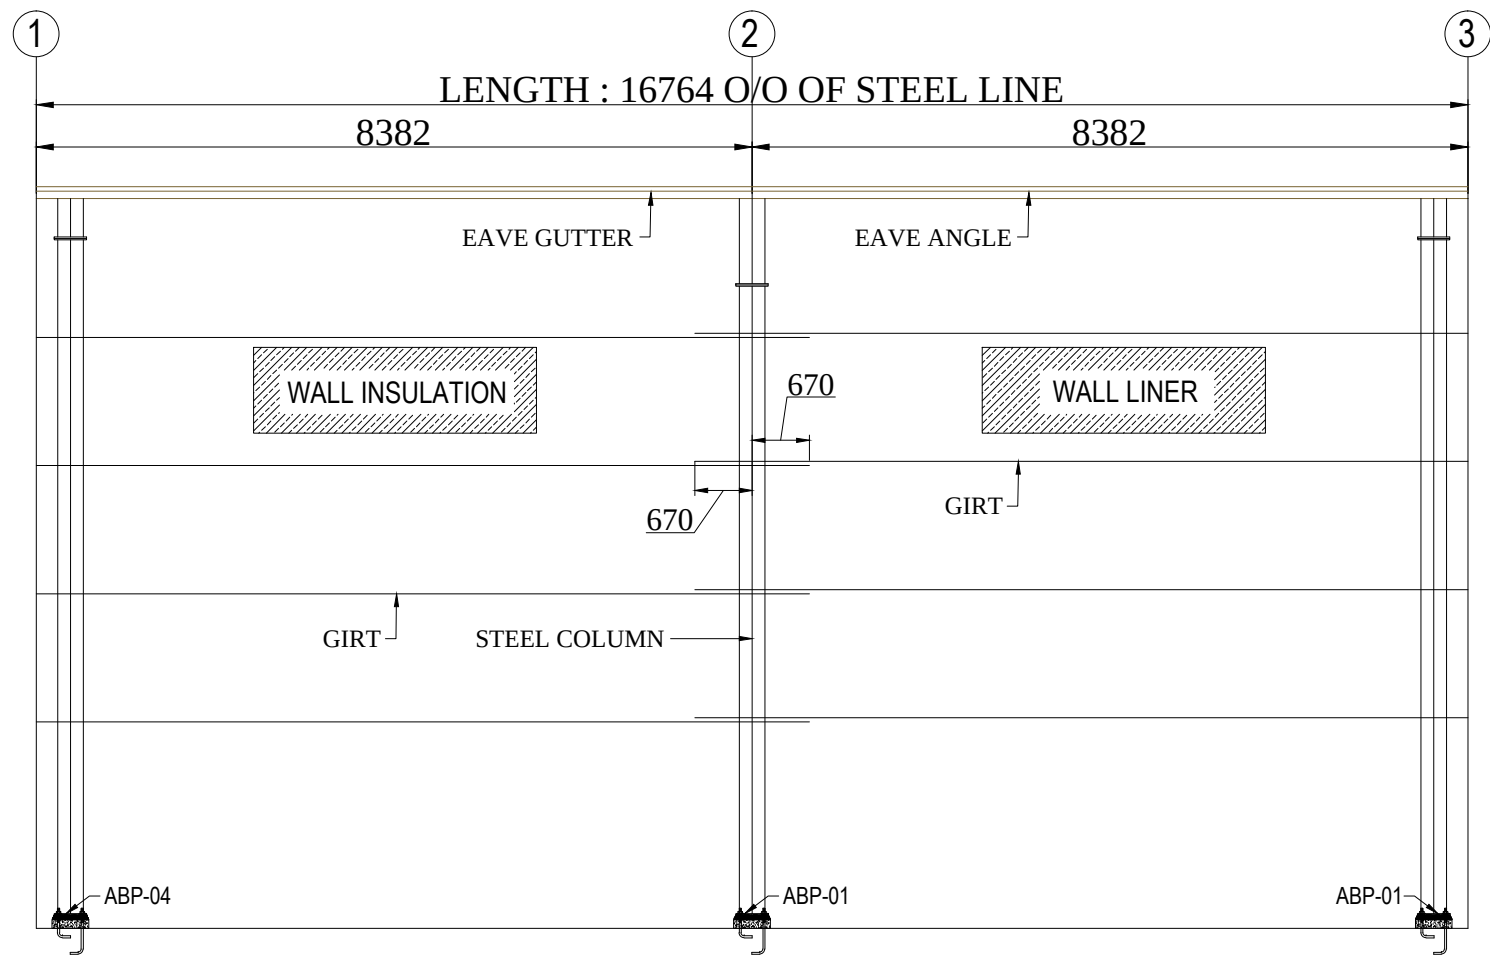

SIDE WALL FRAMING

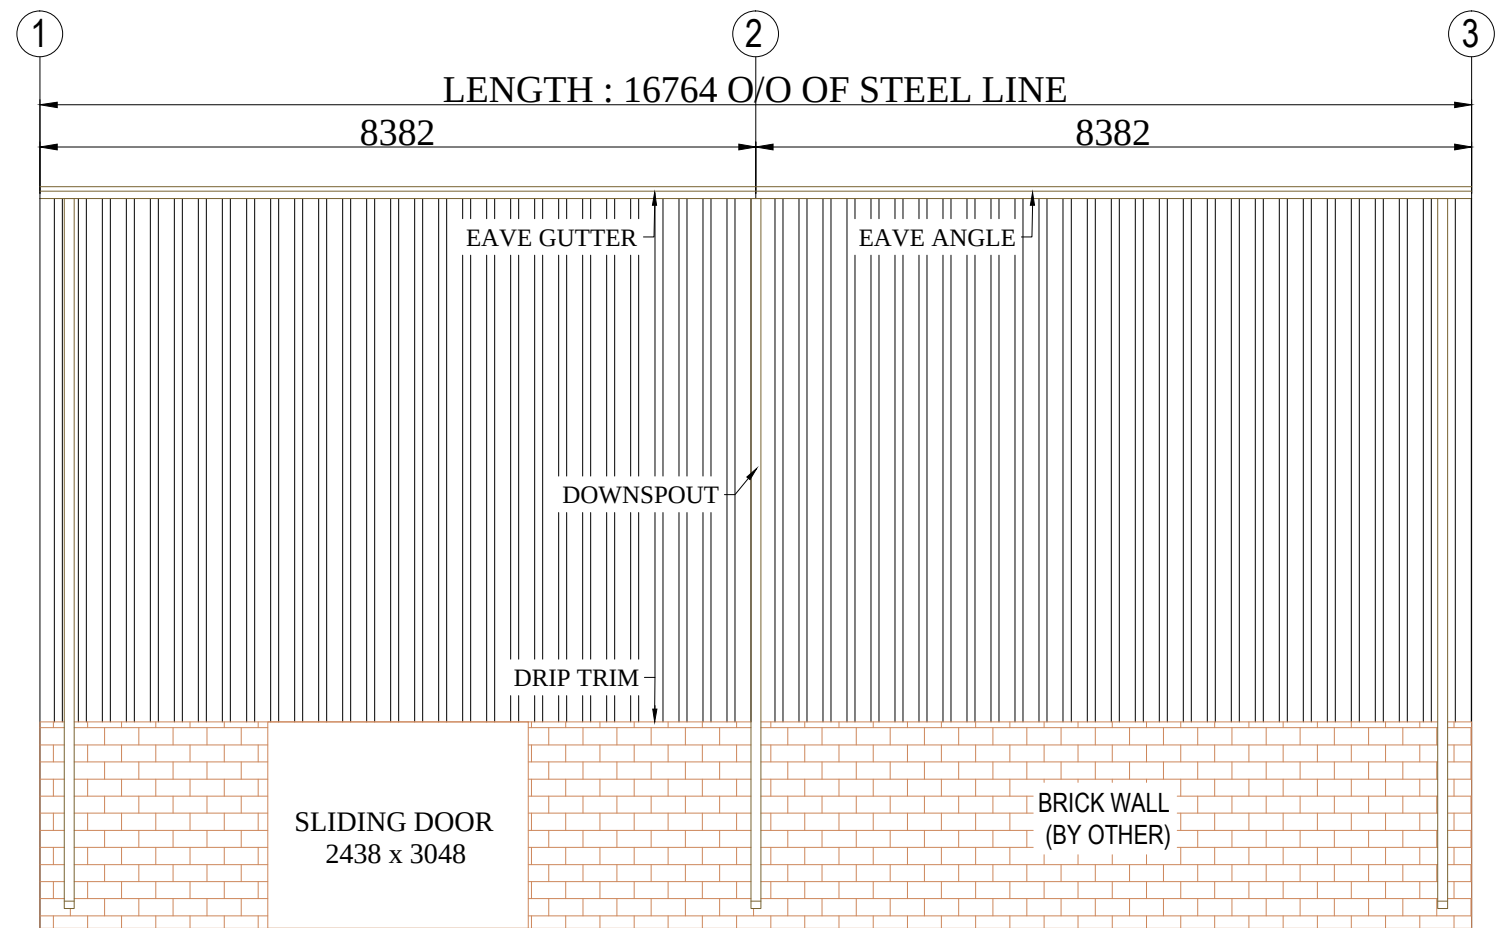

SIDE WALL SHEETING

SIDE WALL @ GRID-E

|      |          |                     |         |        |        |
|------|----------|---------------------|---------|--------|--------|
| 01   | 19-01-22 | ISSUED FOR APPROVAL | R.A     | YEA    | YEA    |
| 00   | 11-11-21 | ISSUED FOR APPROVAL | R.A     | YEA    | YEA    |
| REV. | DATE     | DESCRIPTION         | DRWN BY | CHK BY | APR BY |



MAIMAAR STEEL Pvt.Ltd  
238, Raiwind Road, Thokar Niaz Baig ,LAHORE, Pakistan  
E-mail: nasir.abbas@maimaargroup.com  
E-mail: maimaar.steel@gmail.com  
Website: www.maimaargroup.com  
E-mail: nasir.abbas@maimaargroup.com  
Mob-1 : +(92-300) 807 4017 , +(92-333) 807 1115

|                   |                             |         |    |
|-------------------|-----------------------------|---------|----|
| JOB NO./QUOTE NO. | MSPL-030                    | BLDG #. | 01 |
| PROJECT NAME      | INITIAL PADDLE SANDING HALL |         |    |
| CUSTOMER          | AWAN SPORTS                 |         |    |
| JOBSITE LOCATION  | SIALKOT                     |         |    |

|                    |  |  |          |
|--------------------|--|--|----------|
| SIDE WALL @ GRID E |  |  | DWG. NO. |
|                    |  |  | 11       |

**FOR APPROVAL :**  
IN ORDER TO SCHEDULE THIS PROJECT  
IN AN EFFICIENT MANNER , KINDLY  
RETURN THESE DRAWINGS WITH YOUR  
ANY CHANGES MADE AFTER THE  
COMMENTS MARKED IN RED  
APPROVAL OF THESE DRAWINGS MAY  
DELAY THE FABRICATION SCHEDULE AND  
SUBSEQUENTLY THE DELIVERY OF THE  
BUILDING.  
PLEASE TICK MARK ONLY ONE OF THE FOLLOWING

☐ " APPROVED AS IS "  
☐ " APPROVED AS NOTED"  
☐ " RESUBMIT AS NOTED "

APPROVE : \_\_\_\_\_  
SIGNATURE: \_\_\_\_\_  
DATE : \_\_\_\_\_