


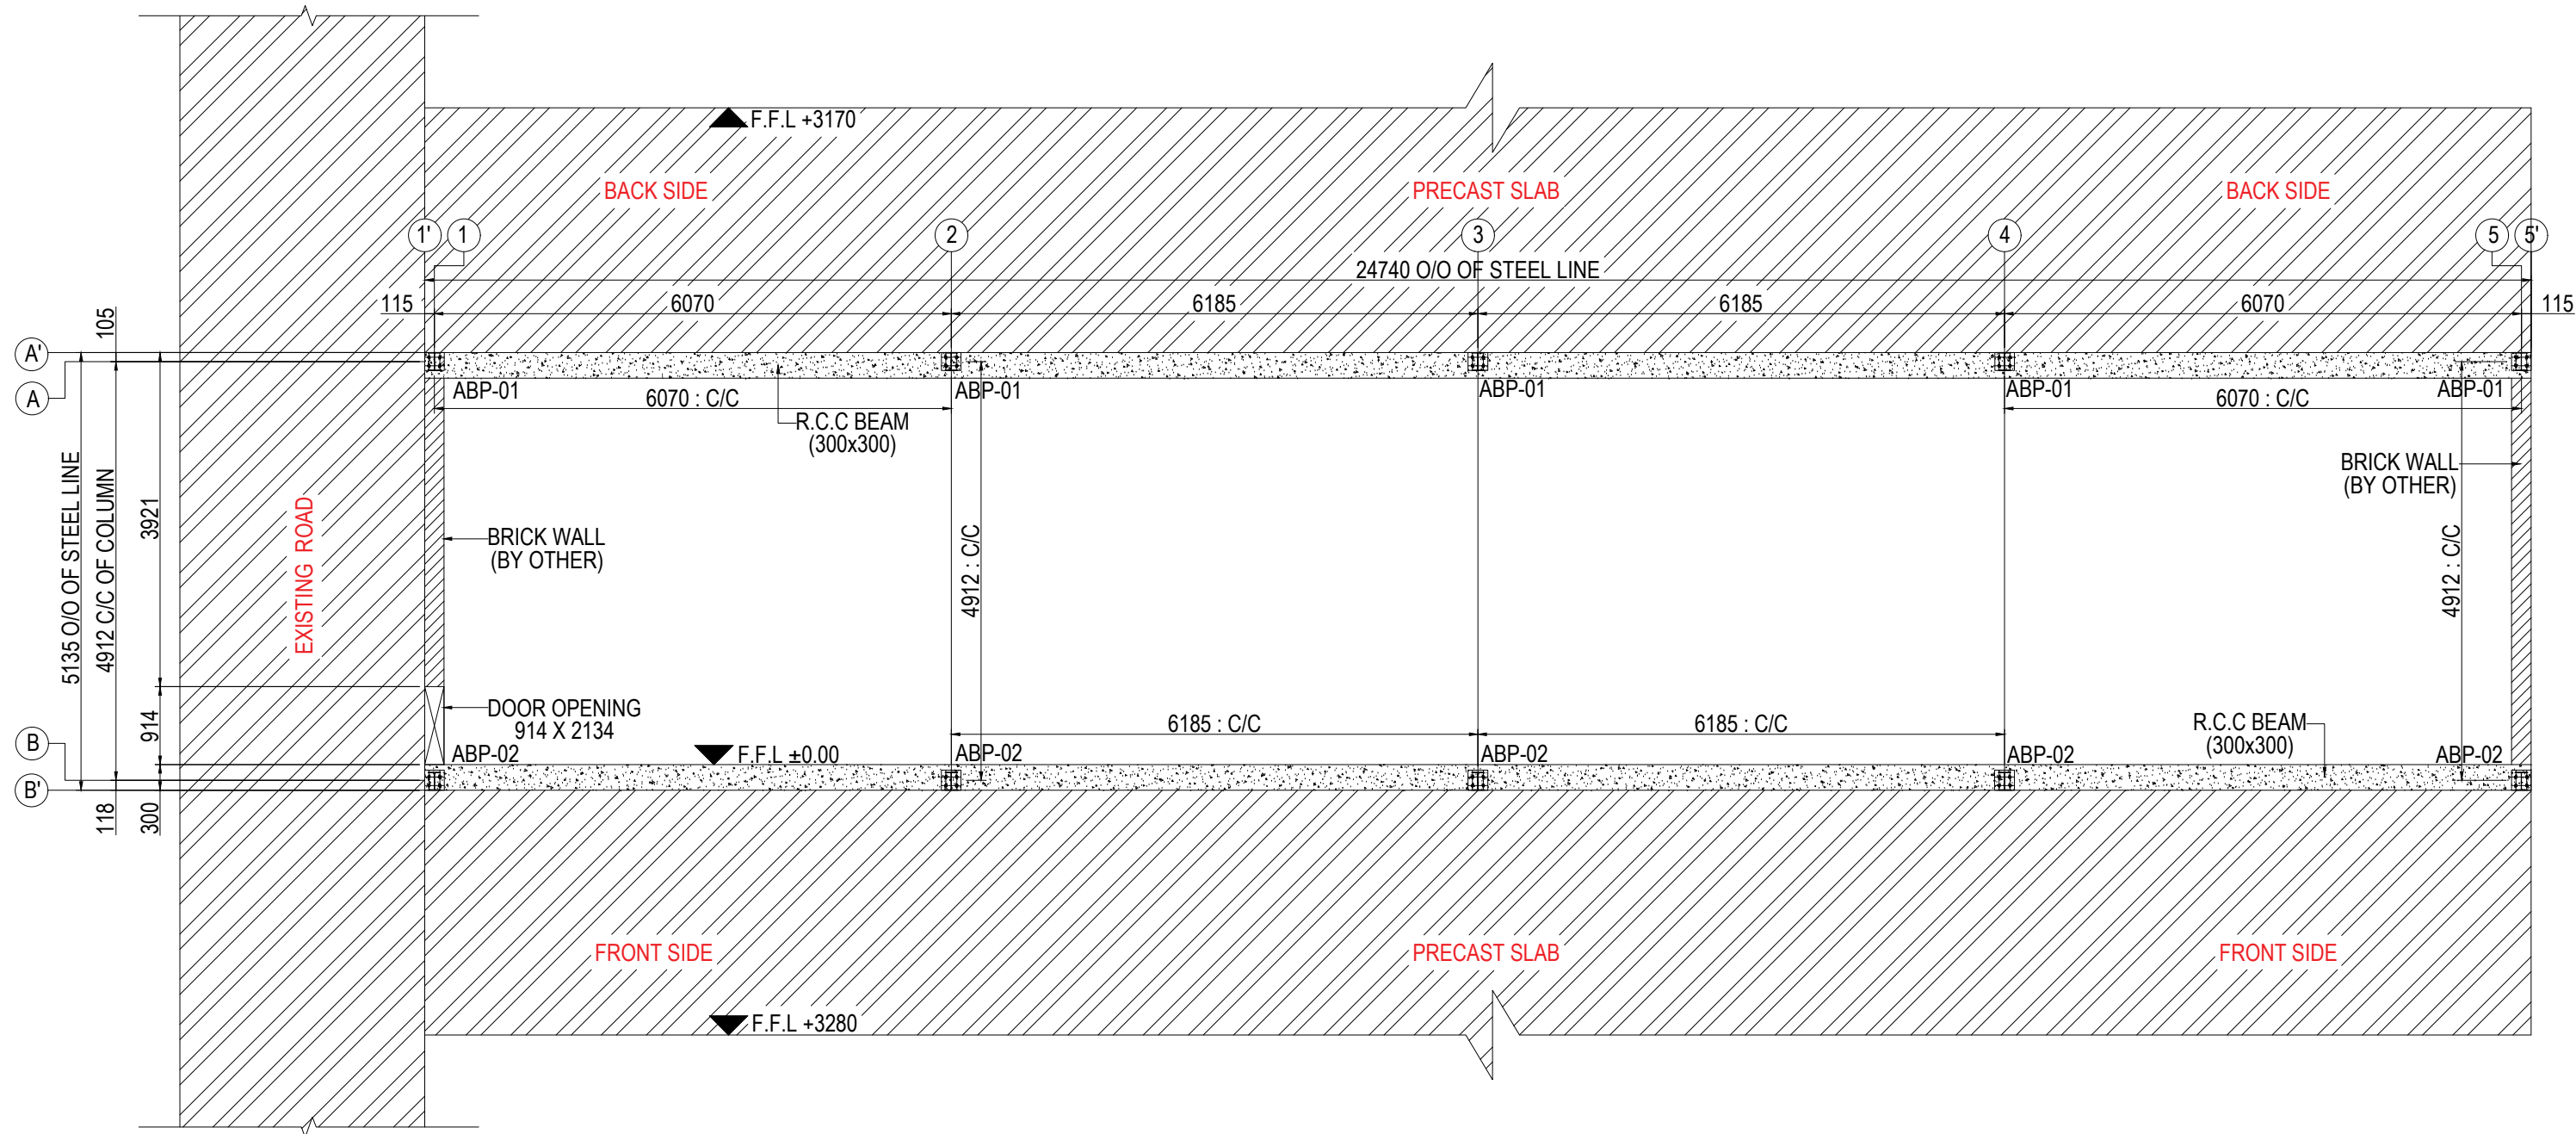

COLUMN LAYOUT PLAN

FOR APPROVAL :

IN ORDER TO SCHEDULE THIS PROJECT IN AN EFFICIENT MANNER , KINDLY RETURN THESE DRAWINGS WITH YOUR ANY CHANGES MADE AFTER THE COMMENTS MARKED IN RED

APPROVAL OF THESE DRAWINGS MAY DELAY THE FABRICATION SCHEDULE AND SUBSEQUENTLY THE DELIVERY OF THE BUILDING.

PLEASE TICK MARK ONLY ONE OF THE FOLLOWING

☐ " APPROVED AS IS "

☐ " APPROVED AS NOTED"

☐ " RESUBMIT AS NOTED "

APPROVE : _____

SIGNATURE: _____

DATE : _____

B	11-03-22	ISSUED FOR APPROVAL	R.A	YEH	YEH
A	24-02-22	ISSUED FOR APPROVAL	MTN	UBD	UBD
REV.	DATE	DESCRIPTION	DRWN BY	CHK BY	APR BY

MAIMAAR



MAIMAAR STEEL Pvt.Ltd

105, Raiwind Road, Thokar Niaz Baig ,Lahore, Pakistan

E-mail: nasir.abbas@maimaargroup.com

E-mail: maimaar.steel@gmail.com

Website: www.maimaargroup.com

E-mail: nasir.abbas@maimaargroup.com

Mob-1 : +(92-300) 807 4017 ,+(92-333) 807 1115

JOB NO./QUOTE NO.	MSPL-034-22	BLDG #.	01
PROJECT NAME	LABORATORY BUILDING		
CUSTOMER	BIN RASHEED GROUP		
JOBSITE LOCATION	MANGA ROAD,LAHORE.		
COLUMN LAYOUT PLAN			
DWG. NO. 02			