


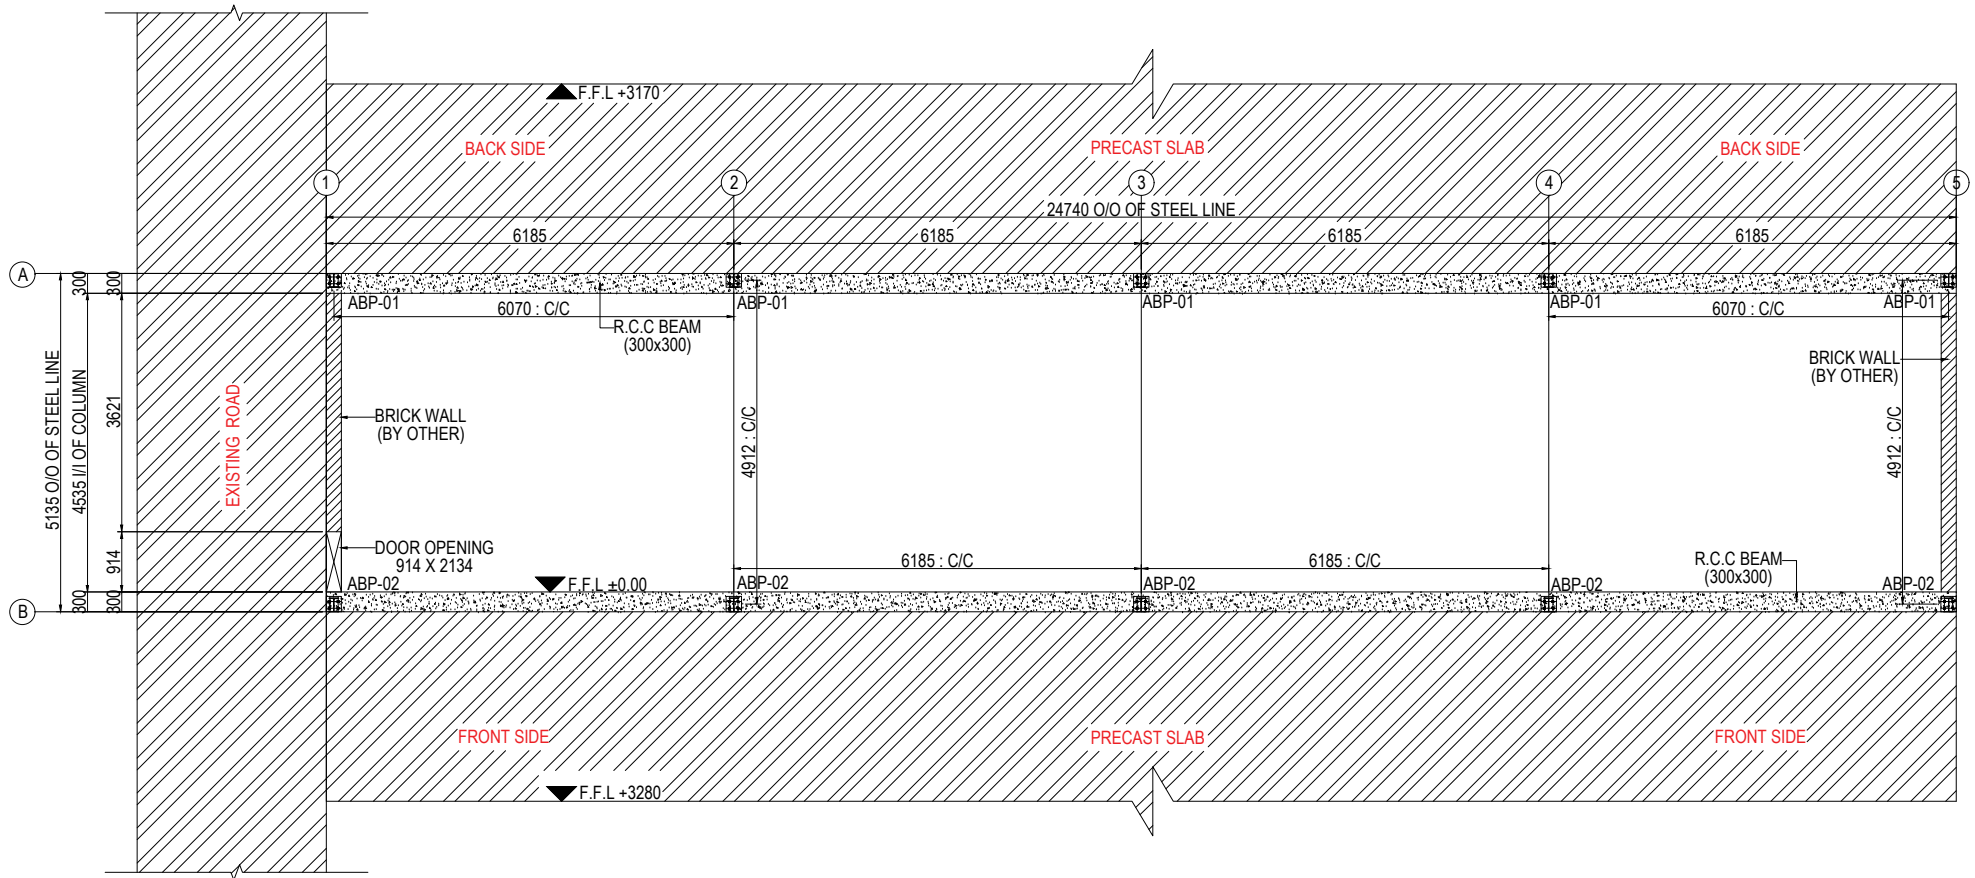

COLUMN LAYOUT PLAN

B	11-03-22	ISSUED FOR APPROVAL	R.A	YEH	YEH
A	24-02-22	ISSUED FOR APPROVAL	MTN	UBD	UBD
REV.	DATE	DESCRIPTION	DRWN BY	CHK BY	APR BY



MAIMAAR STEEL Pvt.Ltd
 105, Raiwind Road, Thokar Niaz Baig, Lahore, Pakistan
 E-mail: nasir.abbas@maimaargroup.com
 E-mail: maimaar.steel@gmail.com
 Website: www.maimaargroup.com
 E-mail: nasir.abbas@maimaargroup.com
 Mob-1 : +(92-300) 807 4017 , +(92-333) 807 1115

FOR APPROVAL :

IN ORDER TO SCHEDULE THIS PROJECT
 IN AN EFFICIENT MANNER , KINDLY
 RETURN THESE DRAWINGS WITH YOUR
 ANY CHANGES MADE AFTER THE
 COMMENTS MARKED IN RED

- ☐ " APPROVED AS IS "
- ☐ " APPROVED AS NOTED "
- ☐ " RESUBMIT AS NOTED "

APPROVAL OF THESE DRAWINGS MAY
 DELAY THE FABRICATION SCHEDULE AND
 SUBSEQUENTLY THE DELIVERY OF THE
 BUILDING.

APPROVE : _____
 SIGNATURE: _____
 DATE : _____

PLEASE TICK MARK ONLY ONE OF THE FOLLOWING

JOB NO./QUOTE NO.	MSPL-034-22	BLDG #.	01
PROJECT NAME	LABORATORY BUILDING		
CUSTOMER	BIN RASHEED GROUP		
JOB SITE LOCATION	MANGA ROAD, LAHORE.		
COLUMN LAYOUT PLAN			DWG. NO. 02