


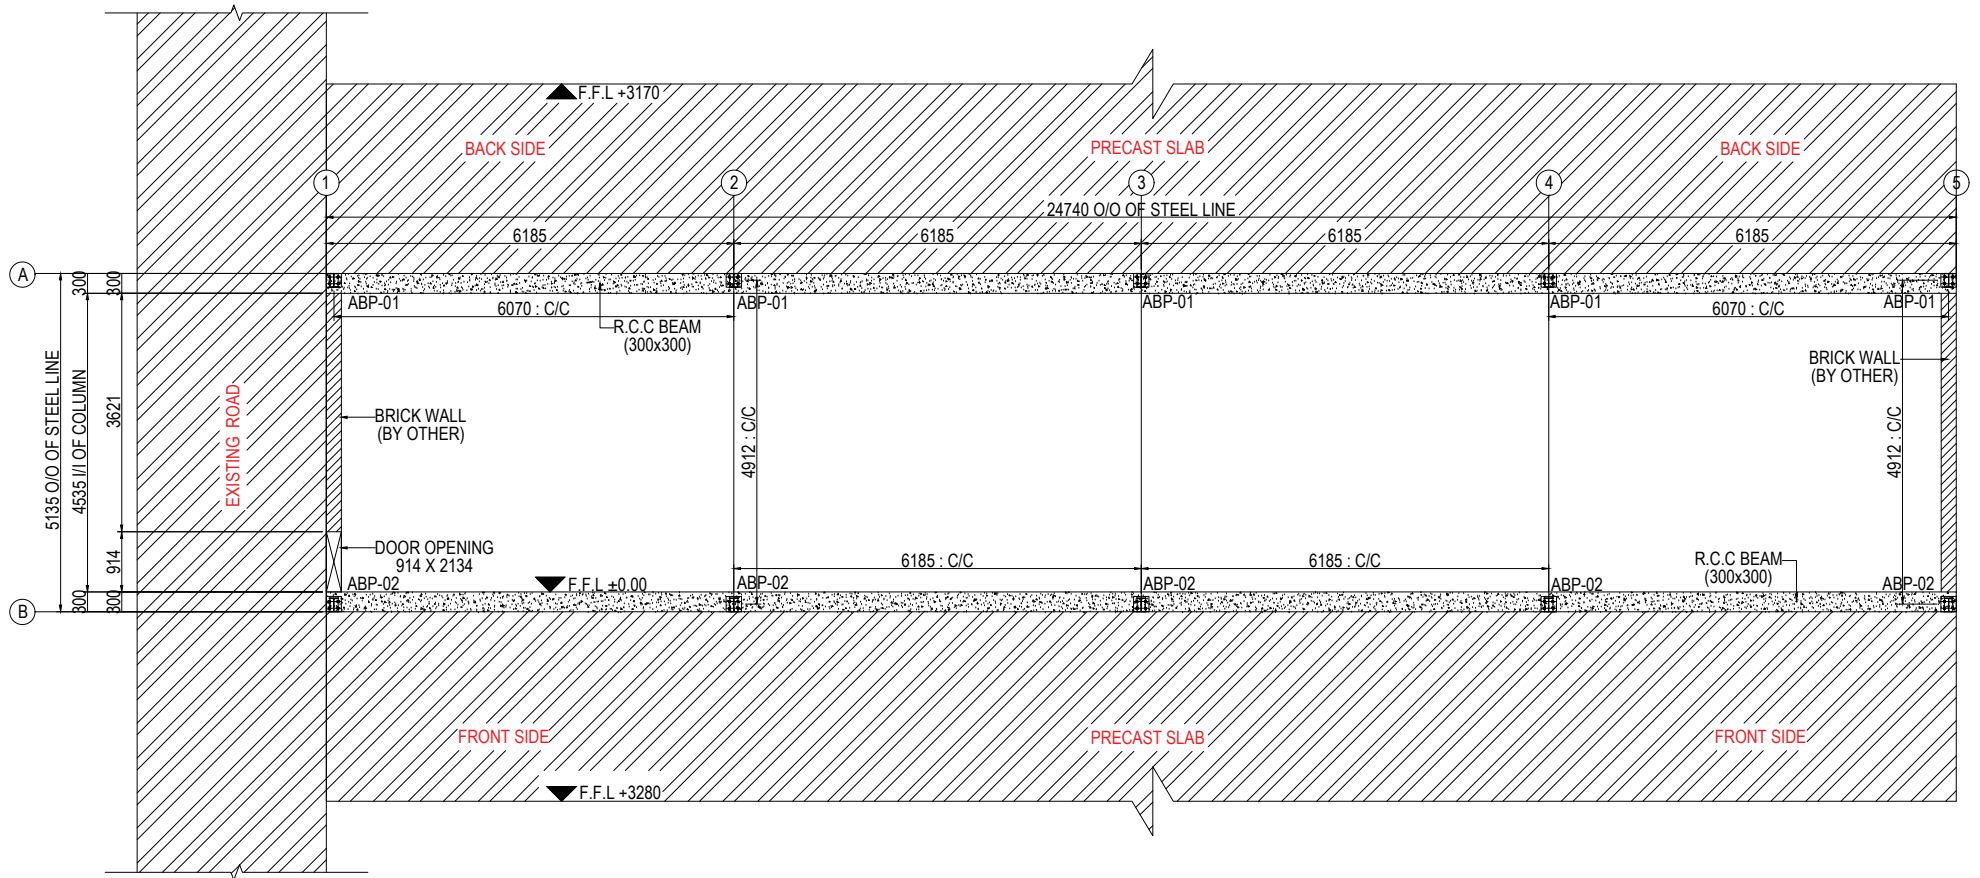

COLUMN LAYOUT PLAN

B	11-03-22	ISSUED FOR APPROVAL	R.A	YEH	YEH
A	24-02-22	ISSUED FOR APPROVAL	MTN	UBD	UBD
REV.	DATE	DESCRIPTION	DRWN BY	CHK BY	APR BY



MAIMAAR STEEL Pvt.Ltd
 105, Raiwind Road, Thokar Niaz Baig, Lahore, Pakistan
 E-mail: nasir.abbas@maimaargroup.com
 E-mail: maimaar.steel@gmail.com
 Website: www.maimaargroup.com
 E-mail: nasir.abbas@maimaargroup.com
 Mob-1 : +(92-300) 807 4017 , +(92-333) 807 1115

JOB NO./QUOTE NO.	MSPL-034-22	BLDG #.	01
PROJECT NAME	LABORATORY BUILDING		
CUSTOMER	BIN RASHEED GROUP		
JOB SITE LOCATION	MANGA ROAD, LAHORE.		

COLUMN LAYOUT PLAN

02

FOR APPROVAL :

IN ORDER TO SCHEDULE THIS PROJECT
 IN AN EFFICIENT MANNER , KINDLY
 RETURN THESE DRAWINGS WITH YOUR
 ANY CHANGES MADE AFTER THE
 COMMENTS MARKED IN RED

APPROVAL OF THESE DRAWINGS MAY
 DELAY THE FABRICATION SCHEDULE AND
 SUBSEQUENTLY THE DELIVERY OF THE
 BUILDING.

PLEASE TICK MARK ONLY ONE OF THE FOLLOWING

- ☐ " APPROVED AS IS "
☐ " APPROVED AS NOTED "
☐ " RESUBMIT AS NOTED "

APPROVE : _____

SIGNATURE: _____

DATE : _____