


FRONT SIDE

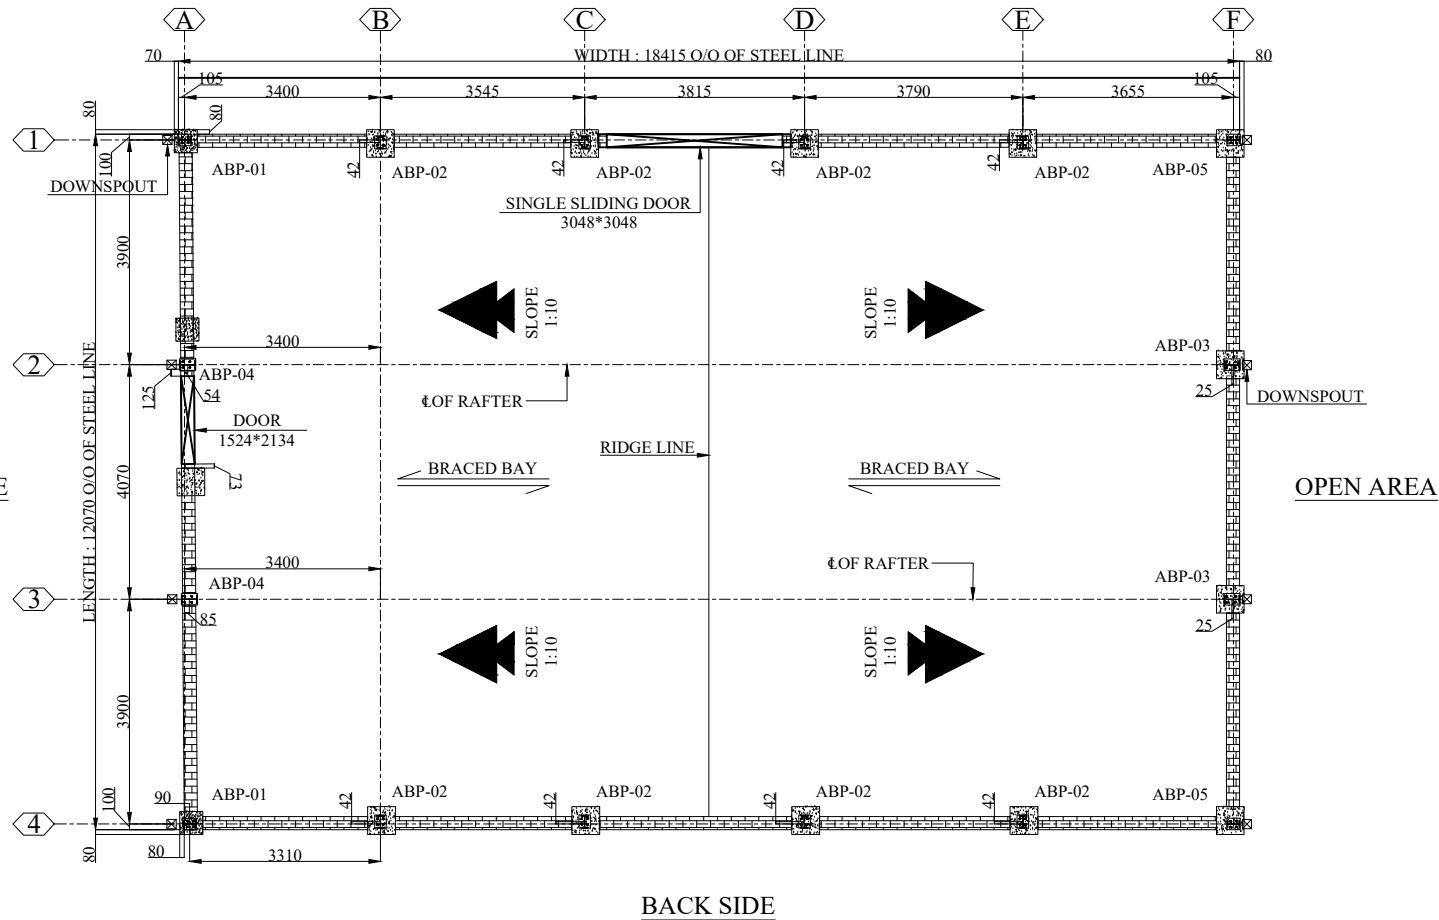

BUILDING DESIGN LOADS:

- ☐ LIVE LOAD ON ROOF = .57 KN/SQ.M
- ☐ LIVE LOAD ON FRAME = .57 KN/SQ.M
- ☐ WIND LOAD = 135 KM/HR
- ☐ EXPOSURE = B
- ☐ SEISMIC ZONE AS PER UBC 1997 = 2B
- ☐ RAINFALL INTENSITY FOR DESIGN OF GUTTERS & DOWNSPOUT = 150 MM/HR

APPROVE : _____
SIGNATURE: _____
DATE : _____

FOR APPROVAL :

IN ORDER TO SCHEDULE THIS PROJECT IN AN EFFICIENT MANNER , KINDLY RETURN THESE DRAWINGS WITH YOUR ANY CHANGES MADE AFTER THE COMMENTS MARKED IN RED APPROVAL OF THESE DRAWINGS MAY DELAY THE FABRICATION SCHEDULE AND SUBSEQUENTLY THE DELIVERY OF THE BUILDING. PLEASE TICK MARK ONLY ONE OF THE FOLLOWING

- ☐ " APPROVED AS IS "
- ☐ " APPROVED AS NOTED "
- ☐ " RESUBMIT AS NOTED "

APPROVE : _____
SIGNATURE: _____
DATE : _____

REV.	DATE	DESCRIPTION	DRWN BY	CHK BY	APR BY
00	20-08-25	ISSUED FOR APPROVAL	M.A	S.R	NAS



MAIMAAR STEEL Pvt.Ltd
238, Raiwind Road, Thokar Niaz Baig ,LAHORE, Pakistan
E-mail: nasir.abbas@maimaargroup.com
E-mail: maimaar.steel@gmail.com
Website: www.maimaargroup.com
E-mail: nasir.abbas@maimaargroup.com
Mob-1 : +(92-300) 807 4017 ,+(92-333) 807 1115

COLUMN & BRICK WALL LAYOUT PLAN

COLUMN & BRICK WALL LAYOUT PLAN

DWG. NO.

01