


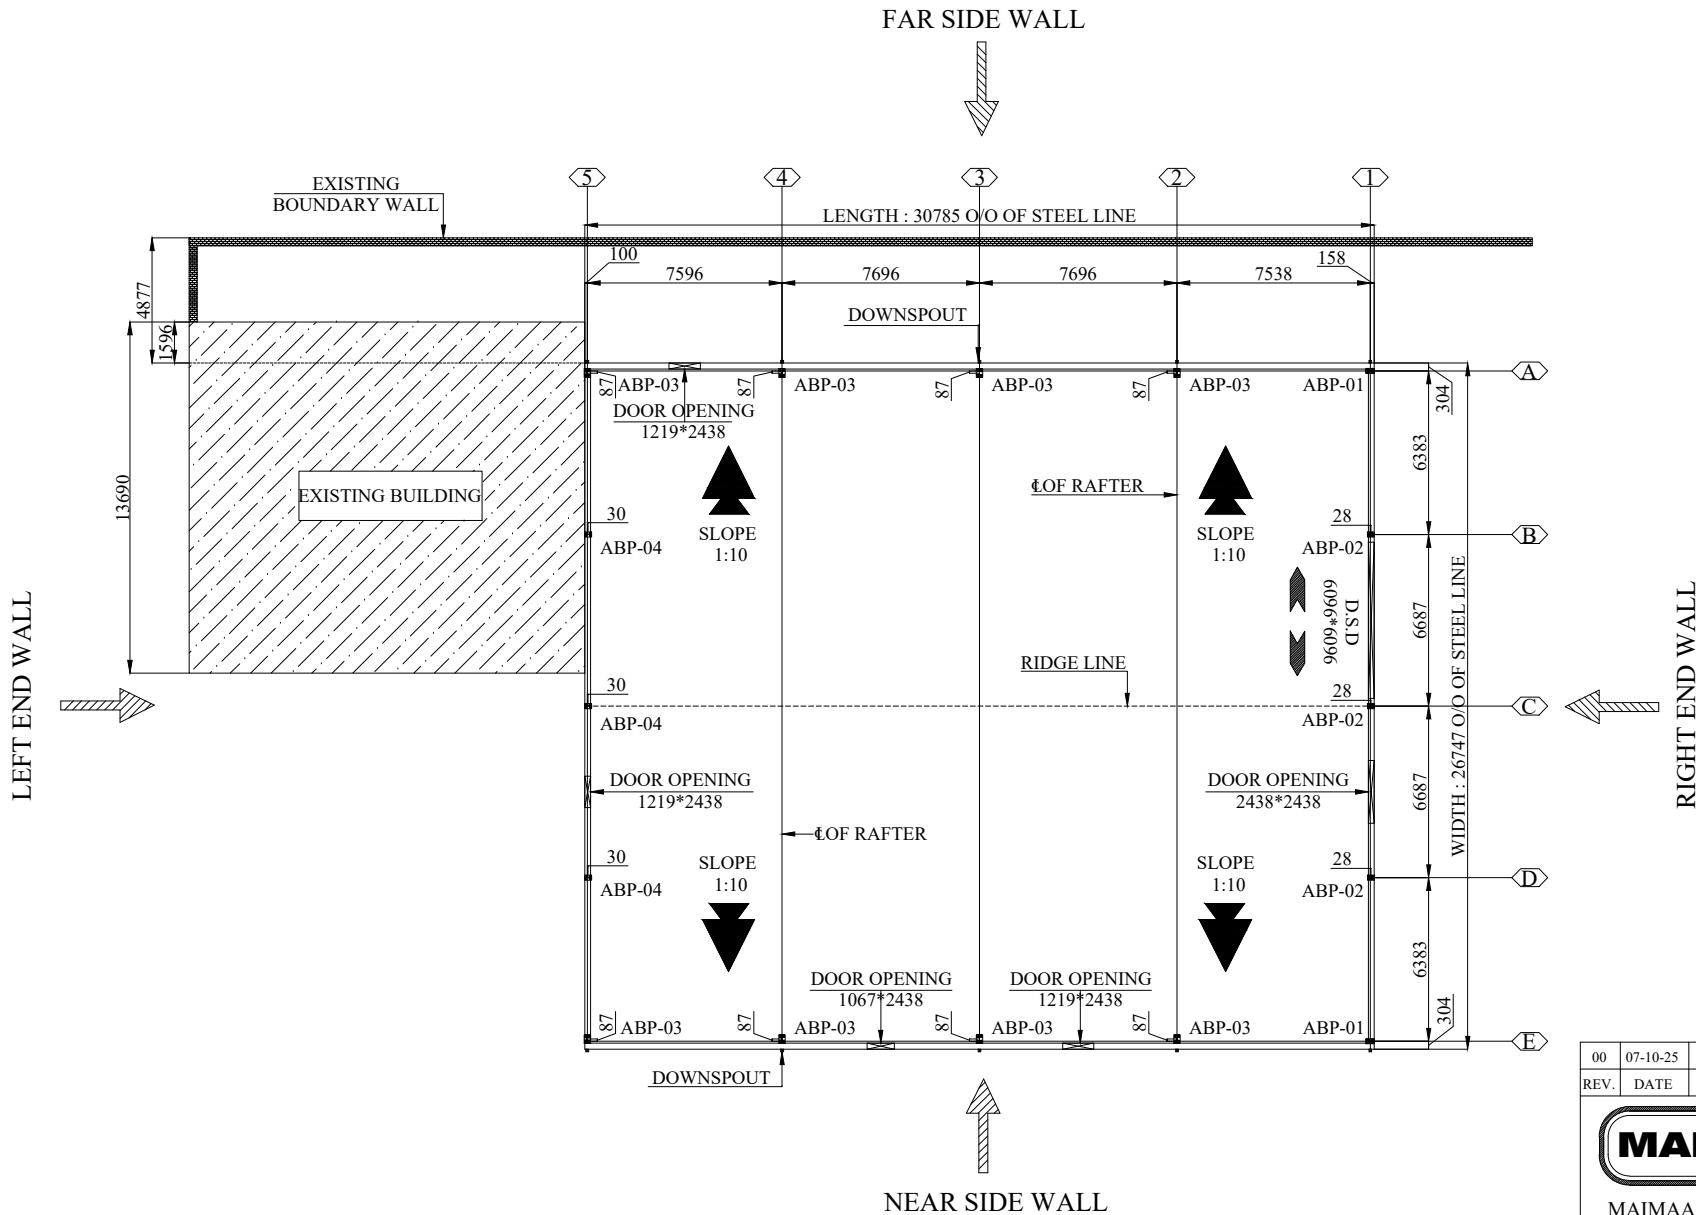

BUILDING DESIGN LOADS:

- ☐ LIVE LOAD ON ROOF = 0.57 KN/SQ.M
- ☐ LIVE LOAD ON FRAME = 0.57 KN/SQ.M
- ☐ WIND SPEED = 160 KM/HR
- ☐ EXPOSURE = B
- ☐ SEISMIC ZONE AS PER UBC 1997 = 2A
- ☐ RAINFALL INTENSITY FOR DESIGN OF GUTTERS & DOWNSPOUT = 150 MM/HR

APPROVE : _____

SIGNATURE: _____

DATE : _____

FOR APPROVAL :

IN ORDER TO SCHEDULE THIS PROJECT IN AN EFFICIENT MANNER, KINDLY RETURN THESE DRAWINGS WITH YOUR ANY CHANGES MADE AFTER THE COMMENTS MARKED IN RED APPROVAL OF THESE DRAWINGS MAY DELAY THE FABRICATION SCHEDULE AND SUBSEQUENTLY THE DELIVERY OF THE BUILDING. PLEASE TICK MARK ONLY ONE OF THE FOLLOWING

APPROVE : _____
SIGNATURE: _____
DATE : _____

☐ " APPROVED AS IS "
☐ " APPROVED AS NOTED "
☐ " RESUBMIT AS NOTED "

REV.	DATE	DESCRIPTION	DRWN BY	CHK BY	APR BY
00	07-10-25	ISSUED FOR APPROVAL	I.U	M.B	NAS



MAIMAAR STEEL Pvt.Ltd
238, Raiwind Road, Thokar Niaz Baig ,LAHORE, Pakistan
E-mail: nasir.abbas@maimaargroup.com
E-mail: maimaar.steel@gmail.com
Website: www.maimaargroup.com
E-mail: nasir.abbas@maimaargroup.com
Mob-1 : +(92-300) 807 4017 ,+(92-333) 807 1115

JOB NO.	MSPL-206	BUILDING #.	01
PROJECT NAME	EXTENSION OF PLANT BUILDING FOR DAIRYLAC		
CUSTOMER	--		
JOBSITE LOCATION	JARANWALA		

COLUMN LAYOUT PLAN

DWG. NO.

01