



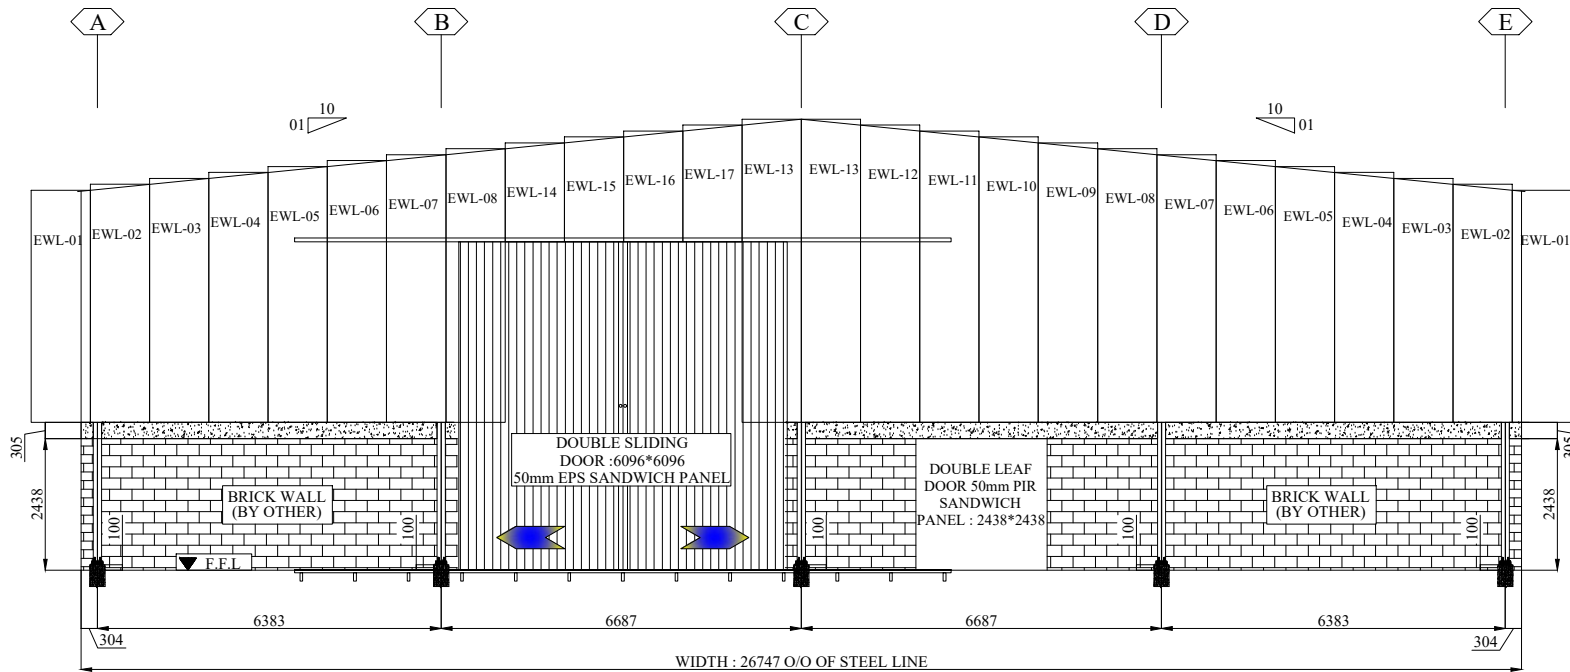

END WALL LINER @ GL- 01

DESCRIPTIONS	PART	LENGTH (MM)	WIDTH (MM)	QUANTITY
END WALL LINER	EWL-01	4,311	1,100	2
END WALL LINER	EWL-02	4,421	1,100	2
END WALL LINER	EWL-03	4,531	1,100	2
END WALL LINER	EWL-04	4,641	1,100	2
END WALL LINER	EWL-05	4,751	1,100	2
END WALL LINER	EWL-06	4,861	1,100	2
END WALL LINER	EWL-07	4,971	1,100	2
END WALL LINER	EWL-08	5,081	1,100	2
END WALL LINER	EWL-09	5,191	1,100	1
END WALL LINER	EWL-10	5,301	1,100	1
END WALL LINER	EWL-11	5,411	1,100	1
END WALL LINER	EWL-12	5,521	1,100	1
END WALL LINER	EWL-13	5,631	1,100	2
END WALL LINER	EWL-14	1,837	1,100	1
END WALL LINER	EWL-15	1,947	1,100	1
END WALL LINER	EWL-16	2,057	1,100	1
END WALL LINER	EWL-17	2,167	1,100	1

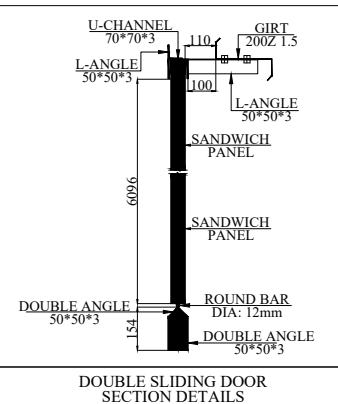

END WALL LINER @ GRID - 1

FOR APPROVAL :

IN ORDER TO SCHEDULE THIS PROJECT IN AN EFFICIENT MANNER , KINDLY RETURN THESE DRAWINGS WITH YOUR ANY CHANGES MADE AFTER THE COMMENTS MARKED IN RED APPROVAL OF THESE DRAWINGS MAY DELAY THE FABRICATION SCHEDULE AND SUBSEQUENTLY THE DELIVERY OF THE BUILDING.

APPROVE : _____
SIGNATURE: _____
DATE : _____
PLEASE TICK MARK ONLY ONE OF THE FOLLOWING

00	07-10-25	ISSUED FOR APPROVAL	I.U	M.B	NAS
REV.	DATE	DESCRIPTION	DRWN BY	CHK BY	APR BY



MAIMAAR STEEL Pvt.Ltd
238, Raiwind Road, Thokar Niaz Baig ,LAHORE, Pakistan
E-mail: nasir.abbas@maimaargroup.com
E-mail: maimaar.steel@gmail.com
Website: www.maimaargroup.com
E-mail: nasir.abbas@maimaargroup.com
Mob-1 : +(92-300) 807 4017 ,+(92-333) 807 1115

JOB NO.	MSPL-206	BUILDING #.	01
PROJECT NAME	EXTENSION OF PLANT BUILDING FOR DAIRYLAC		
CUSTOMER	--		
JOBSITE LOCATION	JARANWALA		

END WALL LINER @ GRID - 1

DWG. NO.
17