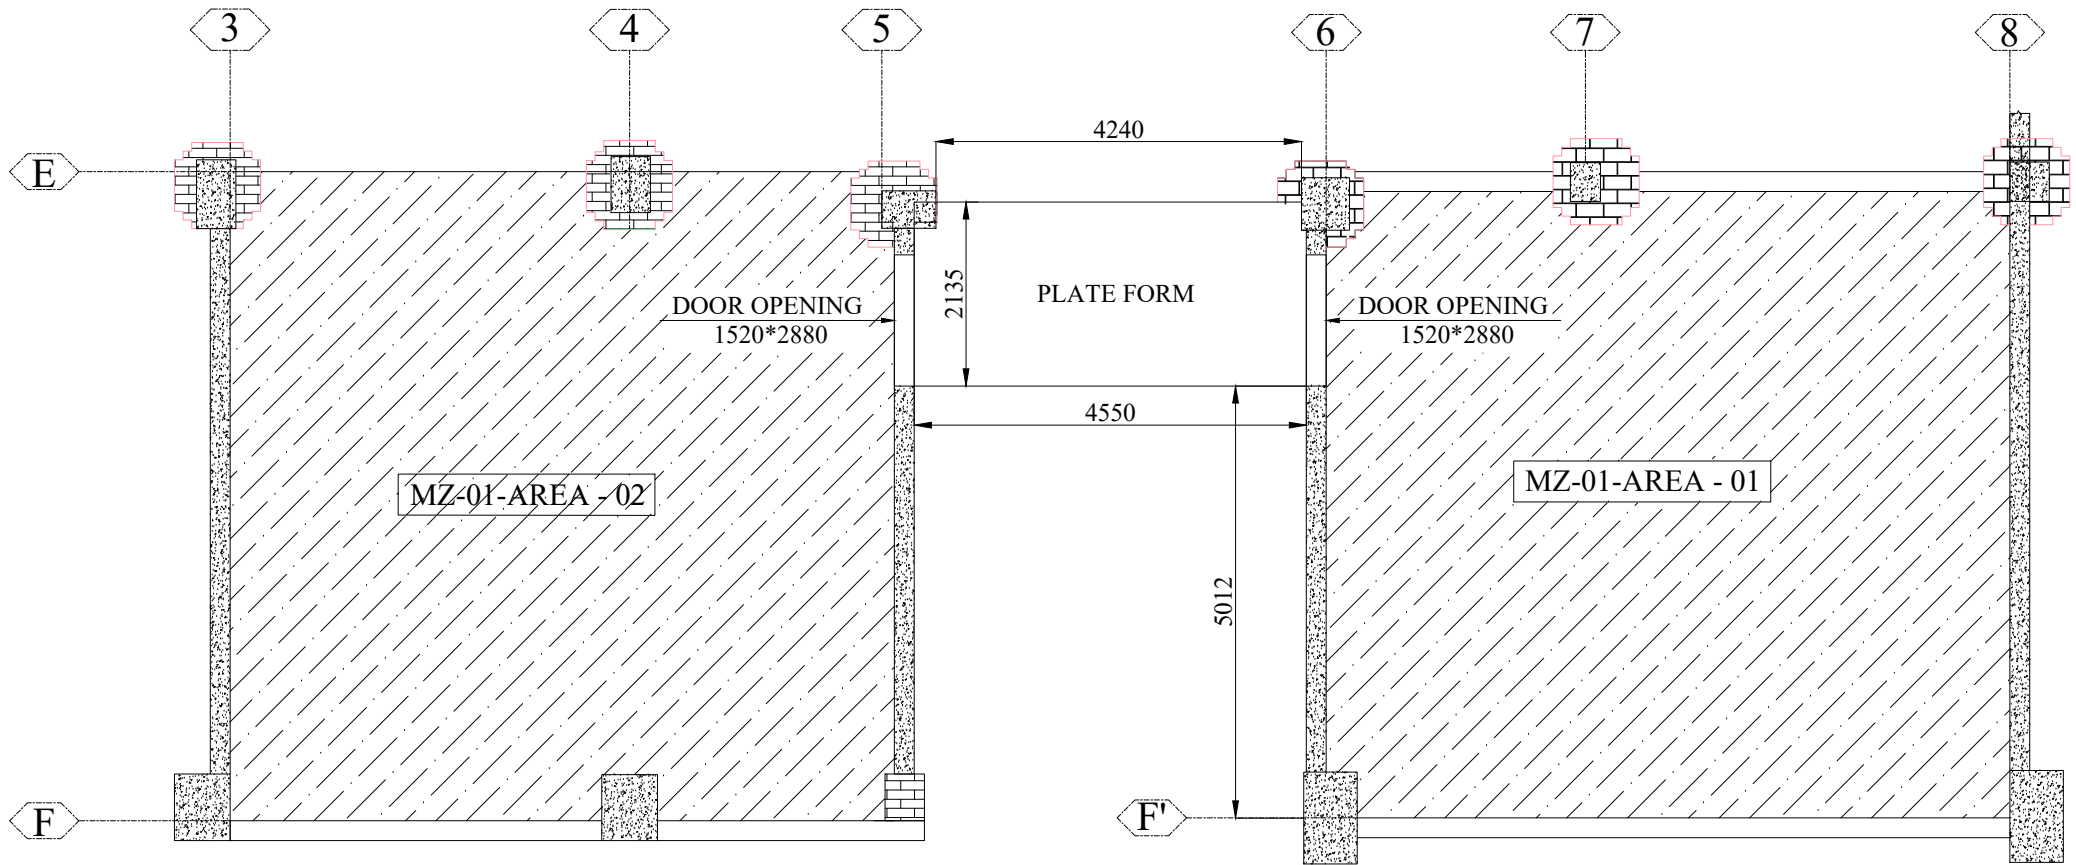




**PLATE FORM LAYOUT PLAN
OF MEZZANINE # 01**

FOR APPROVAL :

IN ORDER TO SCHEDULE THIS PROJECT IN AN EFFICIENT MANNER, KINDLY RETURN THESE DRAWINGS WITH YOUR ANY CHANGES MADE AFTER THE COMMENTS MARKED IN RED

APPROVAL OF THESE DRAWINGS MAY DELAY THE FABRICATION SCHEDULE AND SUBSEQUENTLY THE DELIVERY OF THE BUILDING.

PLEASE TICK MARK ONLY ONE OF THE FOLLOWING

☐ " APPROVED AS IS "

☐ " APPROVED AS NOTED "

☐ " RESUBMIT AS NOTED "

APPROVE : _____

SIGNATURE: _____

DATE : _____

BUILDING DESIGN LOADS:

- ☐ LIVE LOAD ON MEZZANINE = 5 KN/SQ.M
- ☐ SEISMIC ZONE AS PER UBC 1997 = 2A
- ☐ RAINFALL INTENSITY FOR DESIGN OF GUTTERS & DOWNSPOUT = 150mm/HR

APPROVE : _____

SIGNATURE: _____

DATE : _____

00	17-09-25	ISSUED FOR APPROVAL	I.U	M.B	NAS
REV.	DATE	DESCRIPTION	DRWN BY	CHK BY	APR BY



MAIMAAR STEEL Pvt.Ltd
 238, Raiwind Road, Thokar Niaz Baig ,LAHORE, Pakistan
 E-mail: nasir.abbas@maimaargroup.com
 E-mail: maimaar.steel@gmail.com
 Website: www.maimaargroup.com
 E-mail: nasir.abbas@maimaargroup.com
 Mob-1 : +(92-300) 807 4017 ,+(92-333) 807 1115

JOB NO.	MSPL-201	BUILDING #.	01
PROJECT NAME	SUPPLY & INSTALLATION OF MEZZANINE		
CUSTOMER	EAST GATE INDUSTRIES		
JOBSITE LOCATION	LAHORE		

**PLATE FORM LAYOUT PLAN
OF MEZZANINE # 01**

DWG. NO.
01