

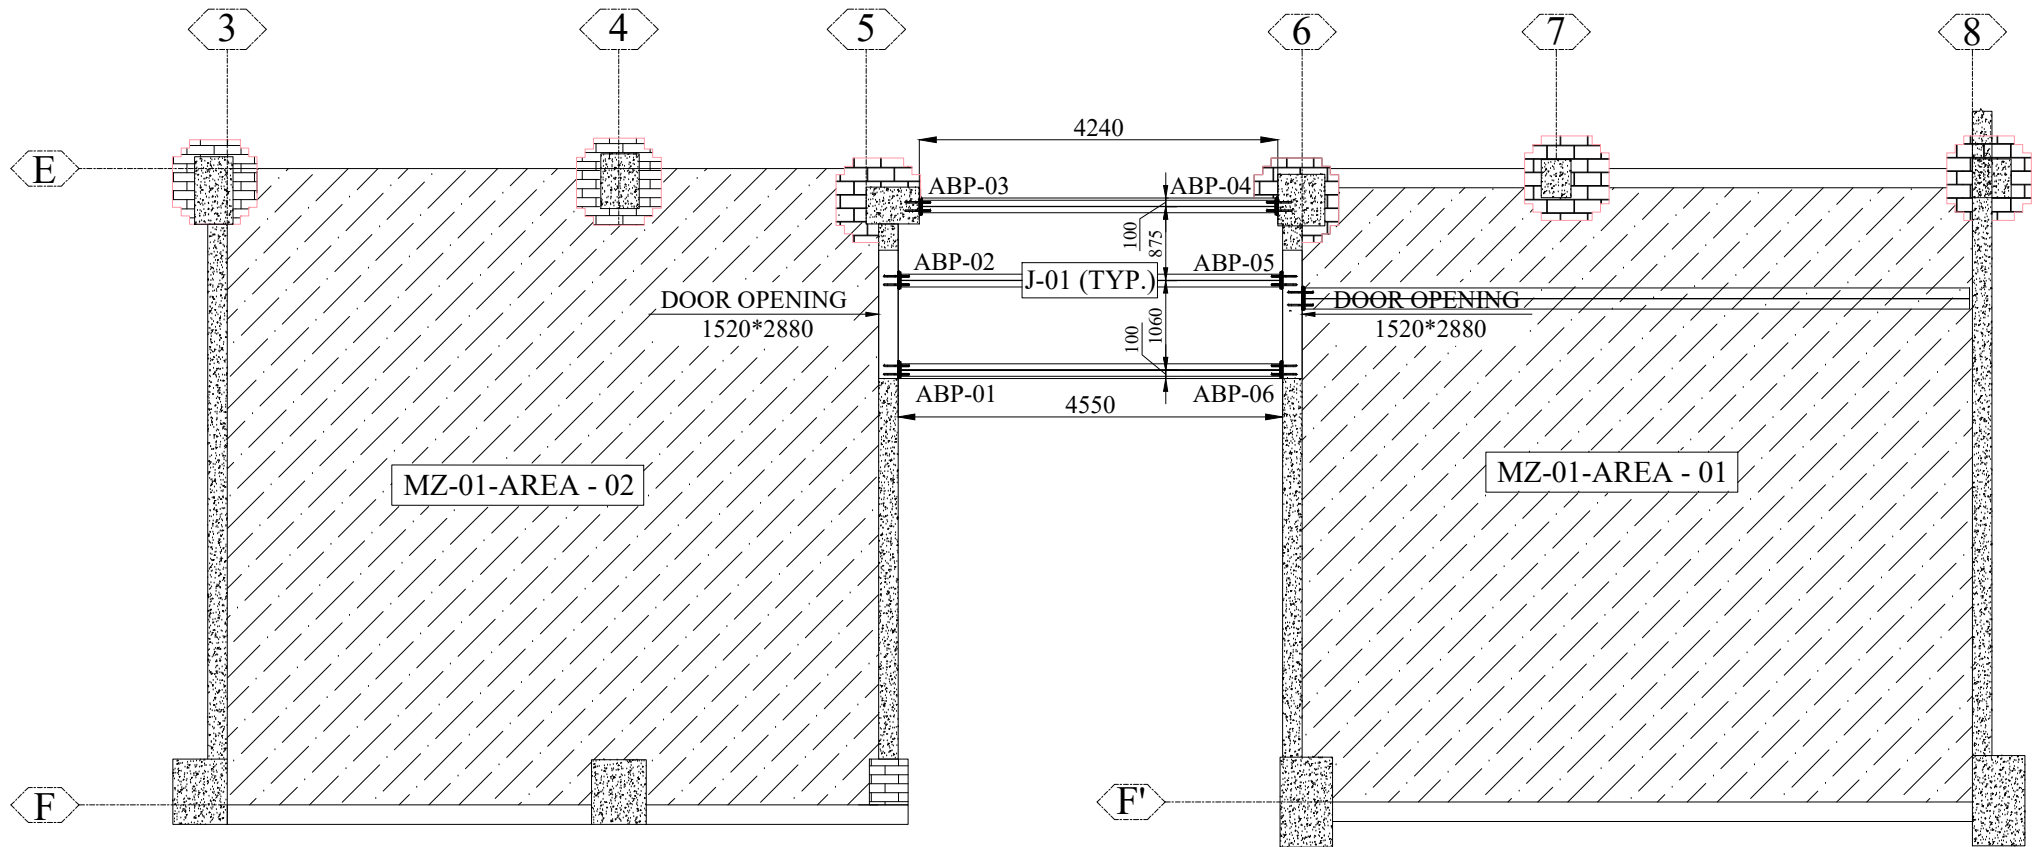


PLATE FORM MEZZANINE # 01
LAYOUT PLAN

MEMBER TABLE OF MEZZANINE # 01					
DESCRIPTION	MARK	WEB DEPTH START/END	WEB PLATE THICK	OUTSIDE FLANGE W x THK	INSIDE FLANGE W x THK
JOIST-01	J-01	300/300	05	150*06	150*06

FOR APPROVAL :

IN ORDER TO SCHEDULE THIS PROJECT
IN AN EFFICIENT MANNER , KINDLY
RETURN THESE DRAWINGS WITH YOUR
ANY CHANGES MADE AFTER THE
COMMENTS MARKED IN RED
APPROVAL OF THESE DRAWINGS MAY
DELAY THE FABRICATION SCHEDULE AND
SUBSEQUENTLY THE DELIVERY OF THE
BUILDING.
PLEASE TICK MARK ONLY ONE OF THE FOLLOWING

- ☐ " APPROVED AS IS "
- ☐ " APPROVED AS NOTED "
- ☐ " RESUBMIT AS NOTED "

APPROVE : _____

SIGNATURE: _____

DATE : _____

00	17-09-25	ISSUED FOR APPROVAL	I.U	M.B	NAS
REV.	DATE	DESCRIPTION	DRWN BY	CHK BY	APR BY



MAIMAAR STEEL Pvt.Ltd
238, Raiwind Road, Thokar Niaz Baig ,LAHORE, Pakistan
E-mail: nasir.abbas@maimaargroup.com
E-mail: maimaar.steel@gmail.com
Website: www.maimaargroup.com
E-mail: nasir.abbas@maimaargroup.com
Mob-1 : +(92-300) 807 4017 ,+(92-333) 807 1115

JOB NO.	MSPL-201	BUILDING #.	01
PROJECT NAME	SUPPLY & INSTALLATION OF MEZZANINE		
CUSTOMER	EAST GATE INDUSTRIES		
JOB SITE LOCATION	LAHORE		

PLATE FORM MEZZANINE # 01
LAYOUT PLAN

DWG. NO.
02