

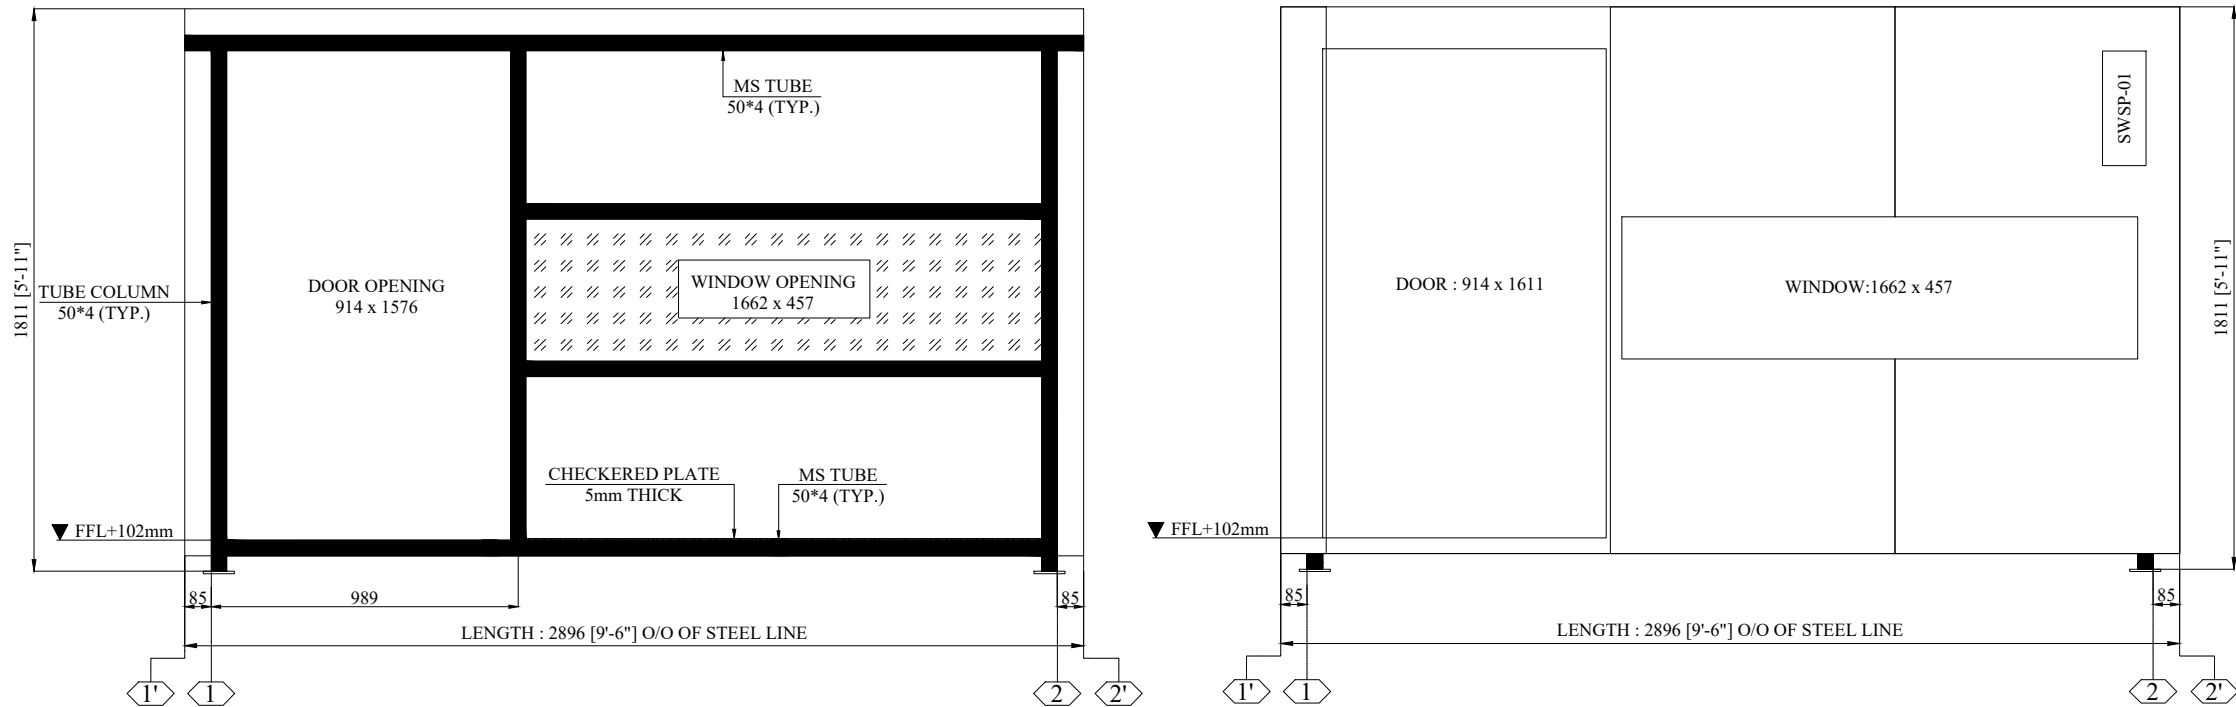


DOOR TRIMS

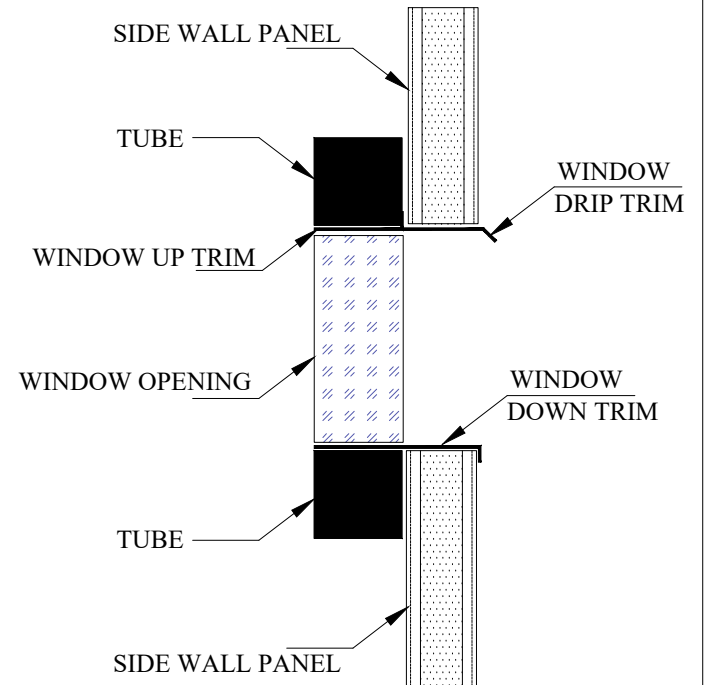

WINDOW TRIMS

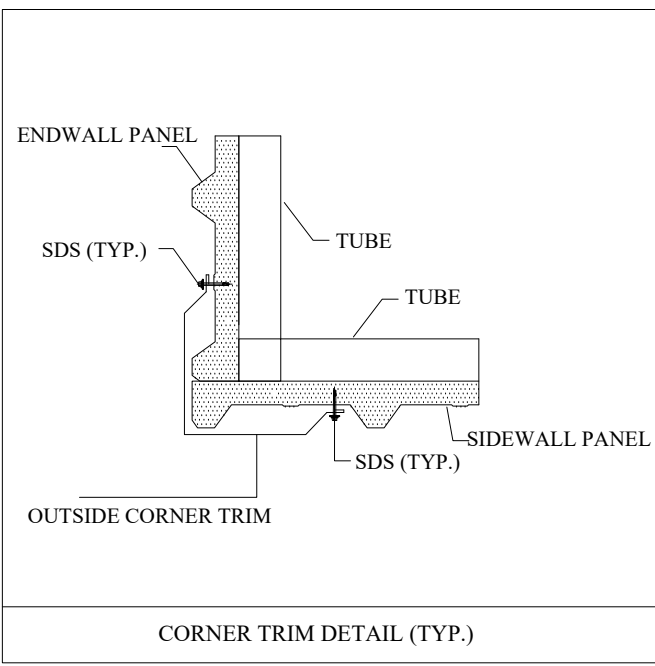

CORNER TRIM DETAIL (TYP.)

SIDE WALL PANEL 50mm PIR SANDWICH PANEL @ GL -B'				
DESCRIPTIONS	PART	LENGTH (MM)	WIDTH (MM)	QUANTITY
SIDE WALL SANDWICH PANEL	SWSP-01	1761	920	3

FOR APPROVAL :

IN ORDER TO SCHEDULE THIS PROJECT IN AN EFFICIENT MANNER , KINDLY RETURN THESE DRAWINGS WITH YOUR ANY CHANGES MADE AFTER THE COMMENTS MARKED IN RED APPROVAL OF THESE DRAWINGS MAY DELAY THE FABRICATION SCHEDULE AND SUBSEQUENTLY THE DELIVERY OF THE BUILDING.

PLEASE TICK MARK ONLY ONE OF THE FOLLOWING

☐ " APPROVED AS IS "

☐ " APPROVED AS NOTED"

☐ " RESUBMIT AS NOTED "

APPROVE : _____

SIGNATURE: _____

DATE : _____

00	27-01-26	ISSUED FOR APPROVAL	I.U	S.S	S.S
REV.	DATE	DESCRIPTION	DRWN BY	CHK BY	APR BY



MAIMAAR STEEL Pvt.Ltd
238, Raiwind Road, Thokar Niaz Baig ,LAHORE, Pakistan
E-mail: nasir.abbas@maimaargroup.com
E-mail: maimaar.steel@gmail.com
Website: www.maimaargroup.com
E-mail: nasir.abbas@maimaargroup.com
Mob-1 : +(92-300) 807 4017 ,+(92-333) 807 1115

JOB NO.	MSPL-227	BUILDING #.	01
PROJECT NAME	SUPPLY & INSTALLATION OF GUARD ROOM		
CUSTOMER	RAHAT ALI		
JOBSITE LOCATION	LAHORE		

SIDE WALL
FRAMING @ PANEL @ GL - B'

DWG. NO.
07