
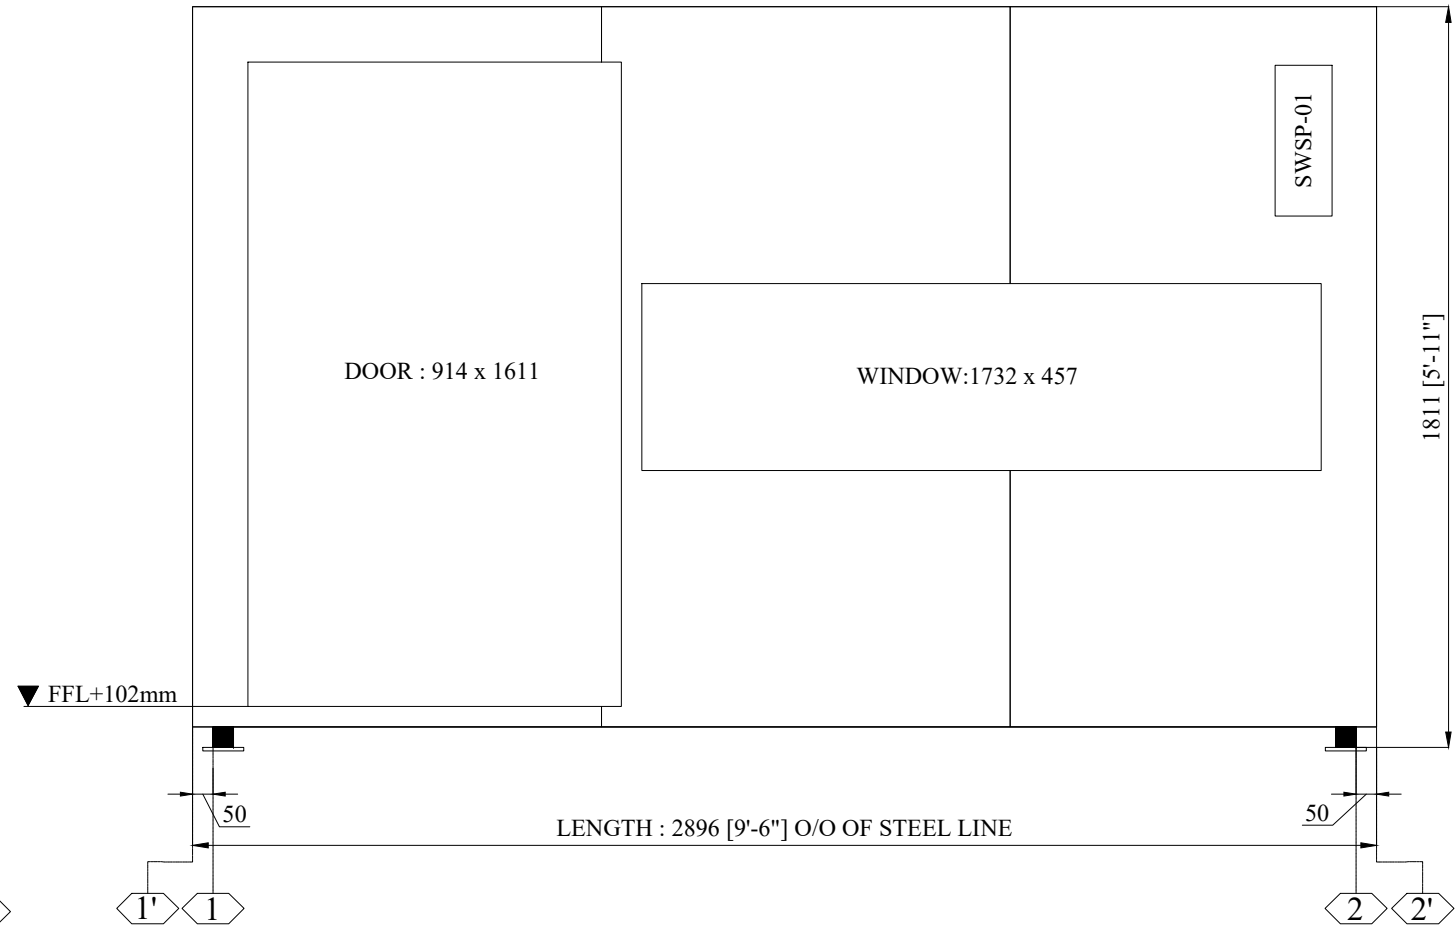


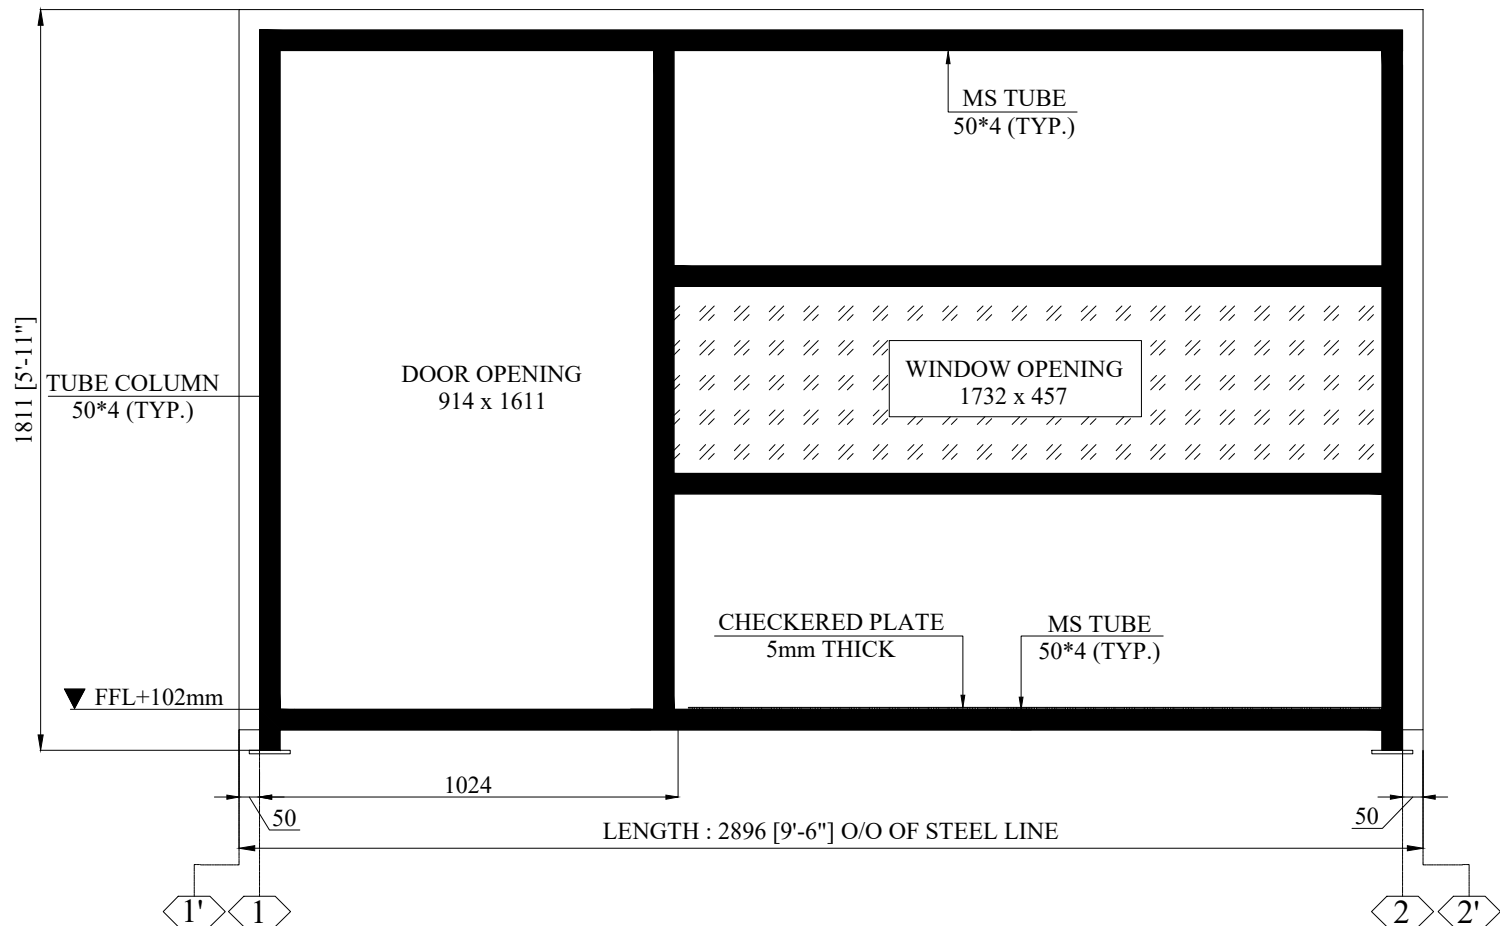

SIDE WALL PANEL
50mm MICRORIB PANEL @ GL -B'

DESCRIPTIONS	PART	LENGTH (MM)	WIDTH (MM)	QUANTITY
SIDE WALL MICRORIB PANEL	SWMP-01	1761	1000	3

FOR APPROVAL :

IN ORDER TO SCHEDULE THIS PROJECT
IN AN EFFICIENT MANNER , KINDLY
RETURN THESE DRAWINGS WITH YOUR
ANY CHANGES MADE AFTER THE
COMMENTS MARKED IN RED
APPROVAL OF THESE DRAWINGS MAY
DELAY THE FABRICATION SCHEDULE AND
SUBSEQUENTLY THE DELIVERY OF THE
BUILDING.
PLEASE TICK MARK ONLY ONE OF THE FOLLOWING

- ☐ " APPROVED AS IS "
☐ " APPROVED AS NOTED"
☐ " RESUBMIT AS NOTED "

APPROVE : _____
SIGNATURE: _____
DATE : _____

00	29-01-26	ISSUED FOR APPROVAL	I.U	S.S	S.S
REV.	DATE	DESCRIPTION	DRWN BY	CHK BY	APR BY
MAIMAAR MAIMAAR STEEL Pvt.Ltd 238, Raiwind Road, Thokar Niaz Baig ,LAHORE, Pakistan E-mail: nasir.abbas@maimaargroup.com E-mail: maimaar.steel@gmail.com Website: www.maimaargroup.com E-mail: nasir.abbas@maimaargroup.com Mob-1 : +(92-300) 807 4017 ,+(92-333) 807 1115					
JOB NO.		MSPL-227		BUILDING #.	01
PROJECT NAME		SUPPLY & INSTALLATION OF GUARD ROOM			
CUSTOMER		RAHAT ALI			
JOBSITE LOCATION		LAHORE			
SIDE WALL FRAMING @ PANEL @ GL - B'				DWG. NO.	
				08	