



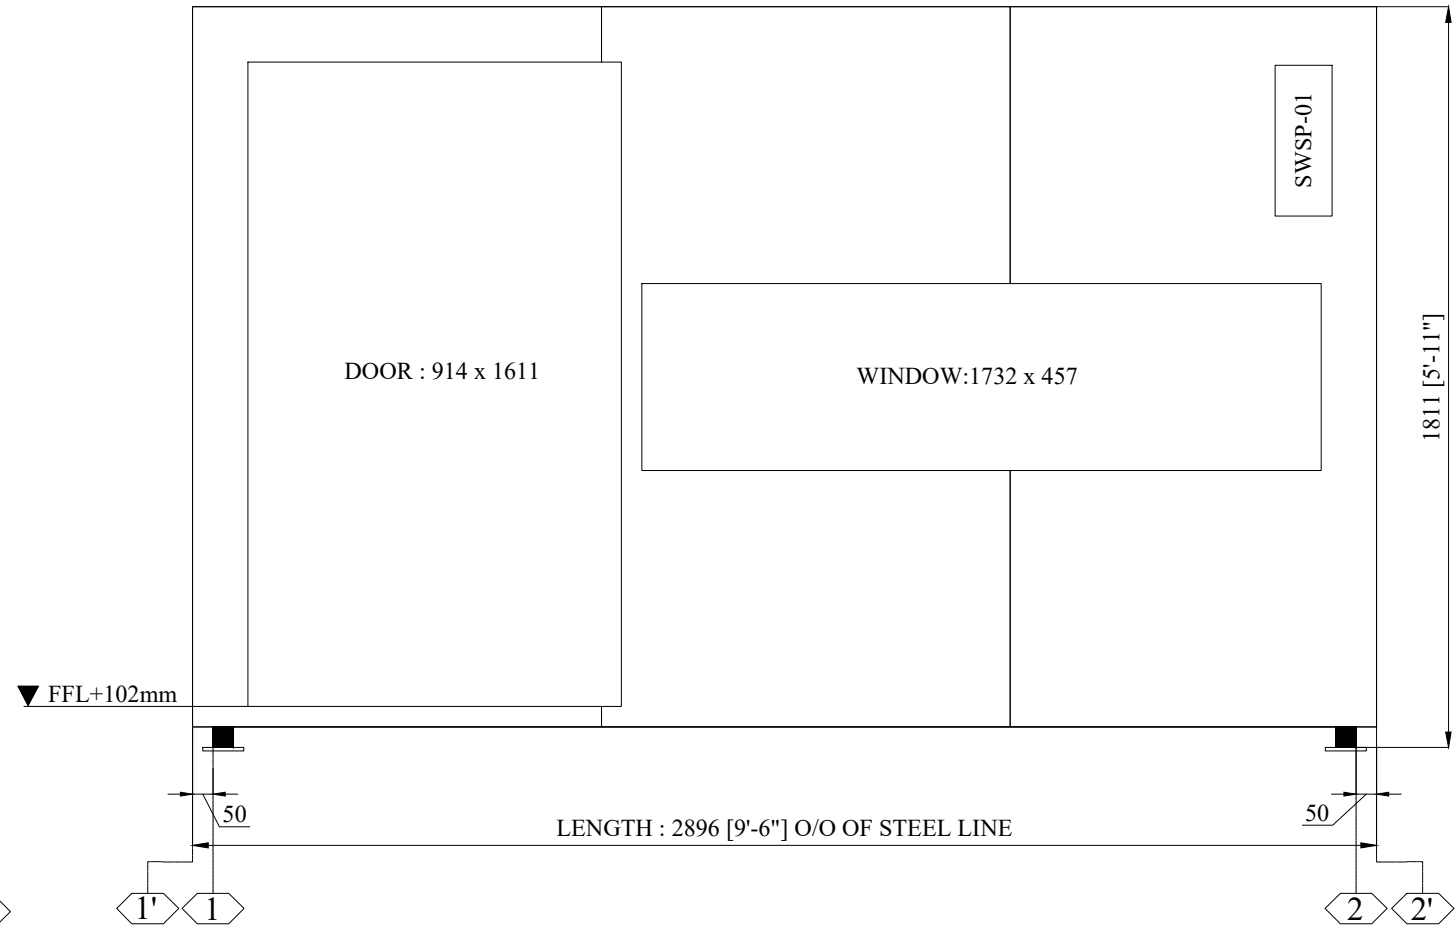

00	29-01-26	ISSUED FOR APPROVAL	I.U	S.S	S.S
REV.	DATE	DESCRIPTION	DRWN BY	CHK BY	APR BY

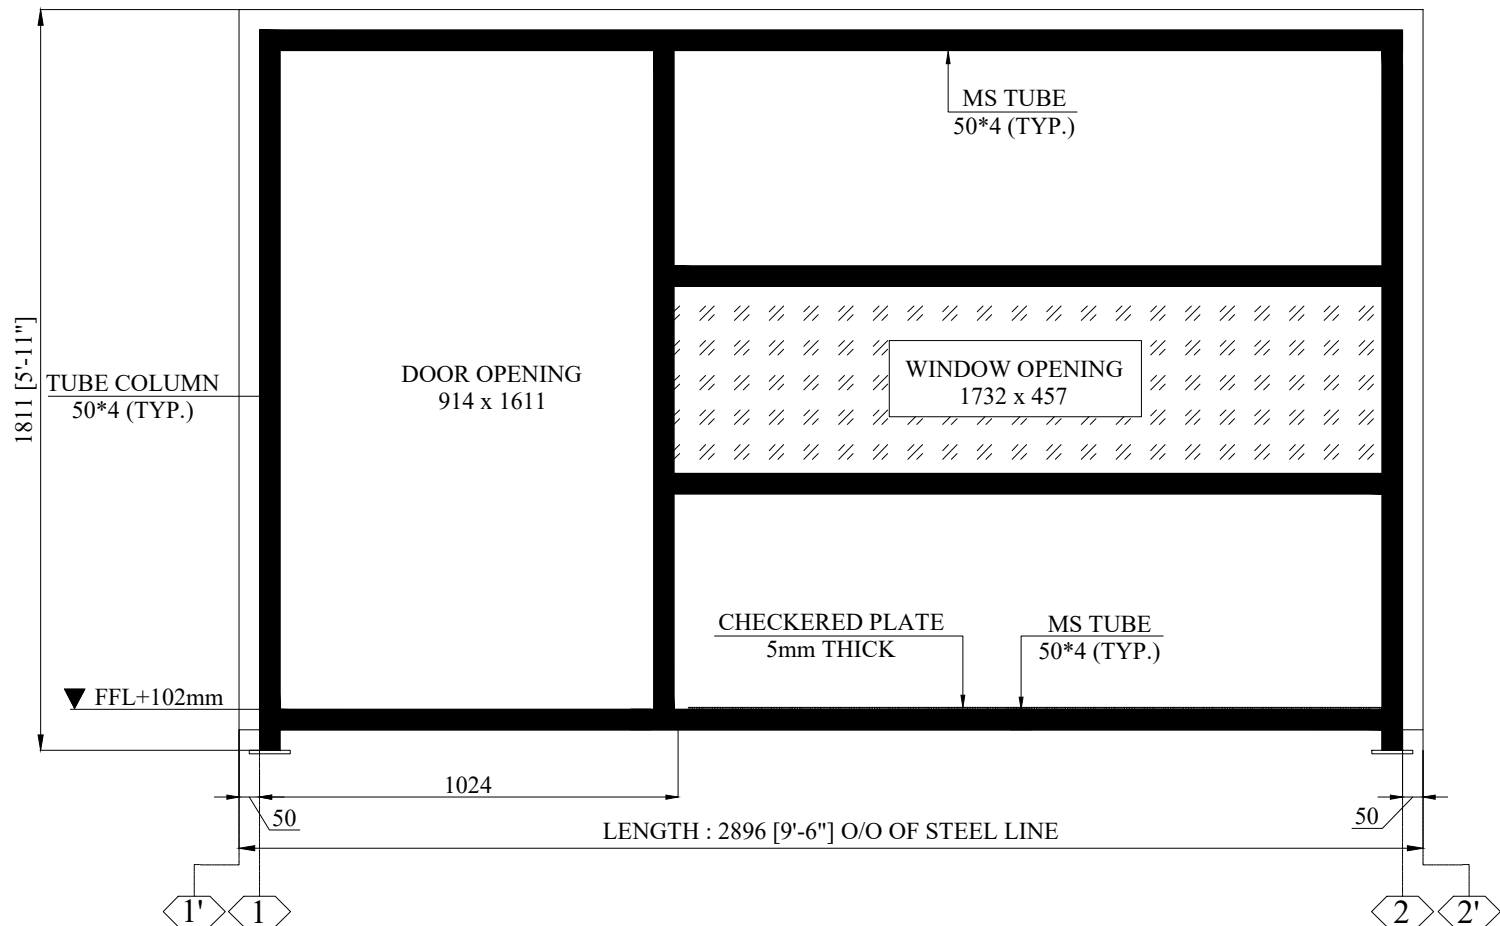

MAIMAAR STEEL Pvt.Ltd
238, Raiwind Road, Thokar Niaz Baig ,LAHORE, Pakistan
E-mail: nasir.abbas@maimaargroup.com
E-mail: maimaar.steel@gmail.com
Website: www.maimaargroup.com
E-mail: nasir.abbas@maimaargroup.com
Mob-1 : +(92-300) 807 4017 ,+(92-333) 807 1115

JOB NO.	MSPL-227	BUILDING #.	01
PROJECT NAME	SUPPLY & INSTALLATION OF GUARD ROOM		
CUSTOMER	RAHAT ALI		
JOBSITE LOCATION	LAHORE		

**SIDE WALL
FRAMING @ PANEL @ GL - B'**

DWG. NO.
08

SIDE WALL PANEL 50mm MICRORIB PANEL @ GL -B'

DESCRIPTIONS	PART	LENGTH (MM)	WIDTH (MM)	QUANTITY
SIDE WALL MICRORIB PANEL	SWMP-01	1761	1000	3

FOR APPROVAL :

IN ORDER TO SCHEDULE THIS PROJECT
IN AN EFFICIENT MANNER , KINDLY
RETURN THESE DRAWINGS WITH YOUR
ANY CHANGES MADE AFTER THE
COMMENTS MARKED IN RED
APPROVAL OF THESE DRAWINGS MAY
DELAY THE FABRICATION SCHEDULE AND
SUBSEQUENTLY THE DELIVERY OF THE
BUILDING.
PLEASE TICK MARK ONLY ONE OF THE FOLLOWING

- ☐ " APPROVED AS IS "
☐ " APPROVED AS NOTED"
☐ " RESUBMIT AS NOTED "

APPROVE : _____

SIGNATURE: _____

DATE : _____