



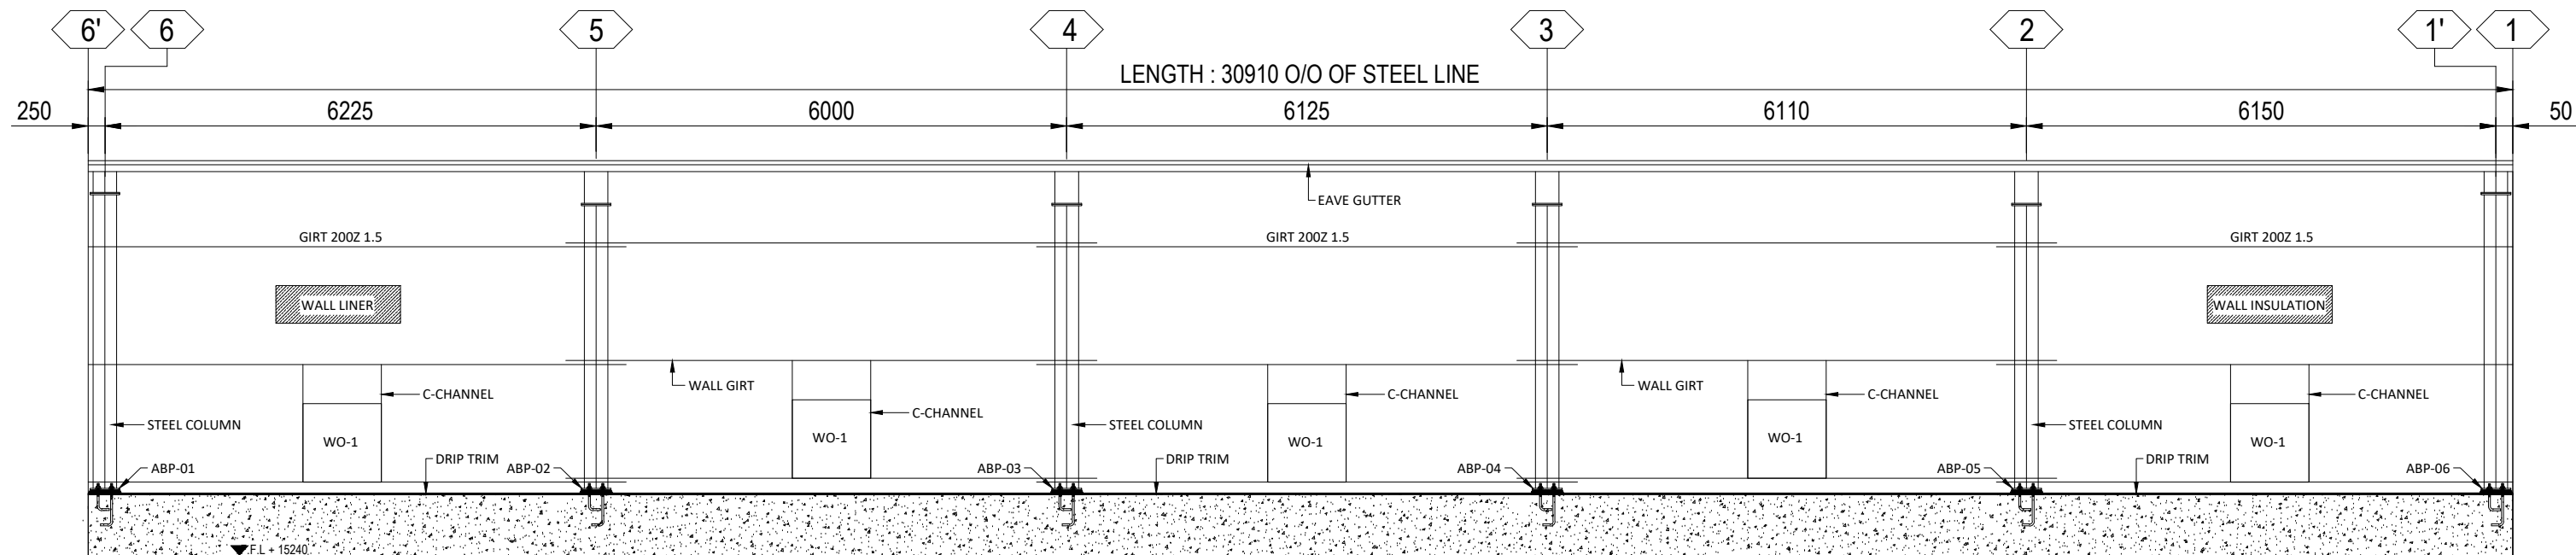

SIDE WALL FRAMING @ GRID - A

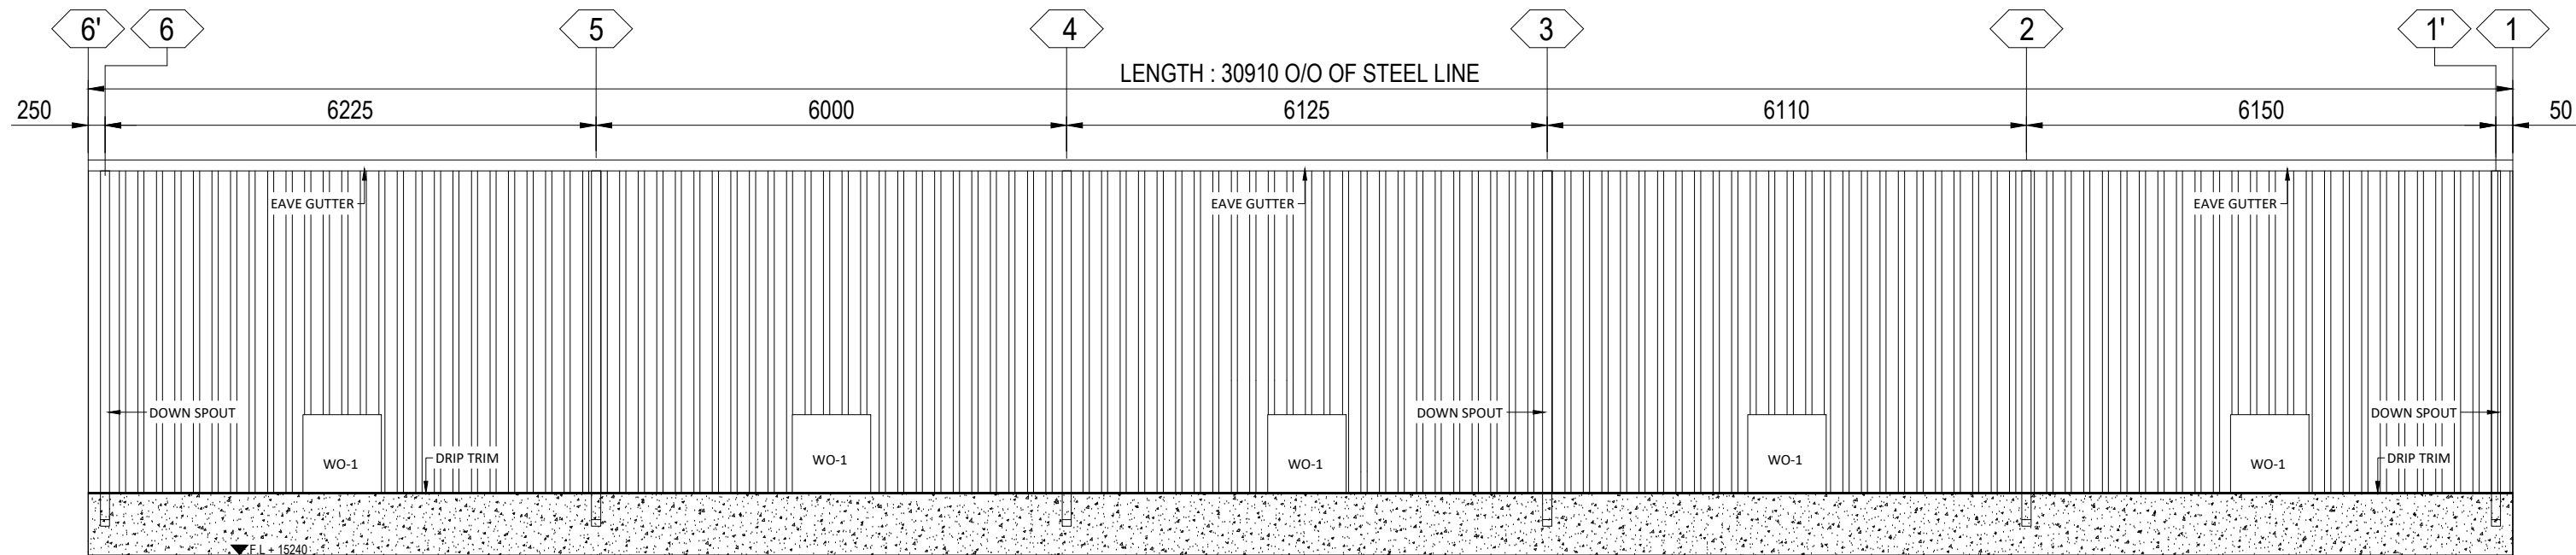

SIDE WALL SHEETING @ GRID - A

NOTE:
ALL OUTSIDE 0.55mm PPGL ROOF/WALL
PANEL (BLUE SCOPE).
0.45mm PPGI LINER PANEL (ISL).

FOR APPROVAL :

IN ORDER TO SCHEDULE THIS PROJECT
IN AN EFFICIENT MANNER , KINDLY
RETURN THESE DRAWINGS WITH YOUR
ANY CHANGES MADE AFTER THE
COMMENTS MARKED IN RED
APPROVAL OF THESE DRAWINGS MAY
DELAY THE FABRICATION SCHEDULE AND
SUBSEQUENTLY THE DELIVERY OF THE
BUILDING.
PLEASE TICK MARK ONLY ONE OF THE FOLLOWING

☐ " APPROVED AS IS "
☐ " APPROVED AS NOTED "
☐ " RESUBMIT AS NOTED "

APPROVE : _____
SIGNATURE: _____
DATE : _____

OPENINGS CHART				
PART MARK	DESCRIPTION	WIDTH	HEIGHT	QTY.
DO-1	DOOR OPENING	1524	2438	01
CO-1	COOLER OPENING	712	712	03
EO-1	EXHAUST OPENING	940	940	04
WO-1	WINDOW OPENING	1000	1000	10

00	21-03-21	ISSUED FOR APPROVAL	R.A	YEA	YEA
REV.	DATE	DESCRIPTION	DRWN BY	CHK BY	APR BY

MAIMAAR

MAIMAAR STEEL Pvt.Ltd

238, Raiwind Road, Thokar Niaz Baig ,LAHORE, Pakistan

E-mail: nasir.abbas@maimaargroup.com

E-mail: maimaar.steel@gmail.com

Website: www.maimaargroup.com

E-mail: nasir.abbas@maimaargroup.com

Mob-1 : +(92-300) 807 4017 ,+(92-333) 807 1115

JOB NO./QUOTE NO.	MSPL-035-22	BLDG #.	01
PROJECT NAME	STEEL SHED BUILDING		
CUSTOMER	GOLD PANEL		
JOBSITE LOCATION	SIALKOT		
SIDE WALL @ GRID-A			
DWG. NO. 14			