


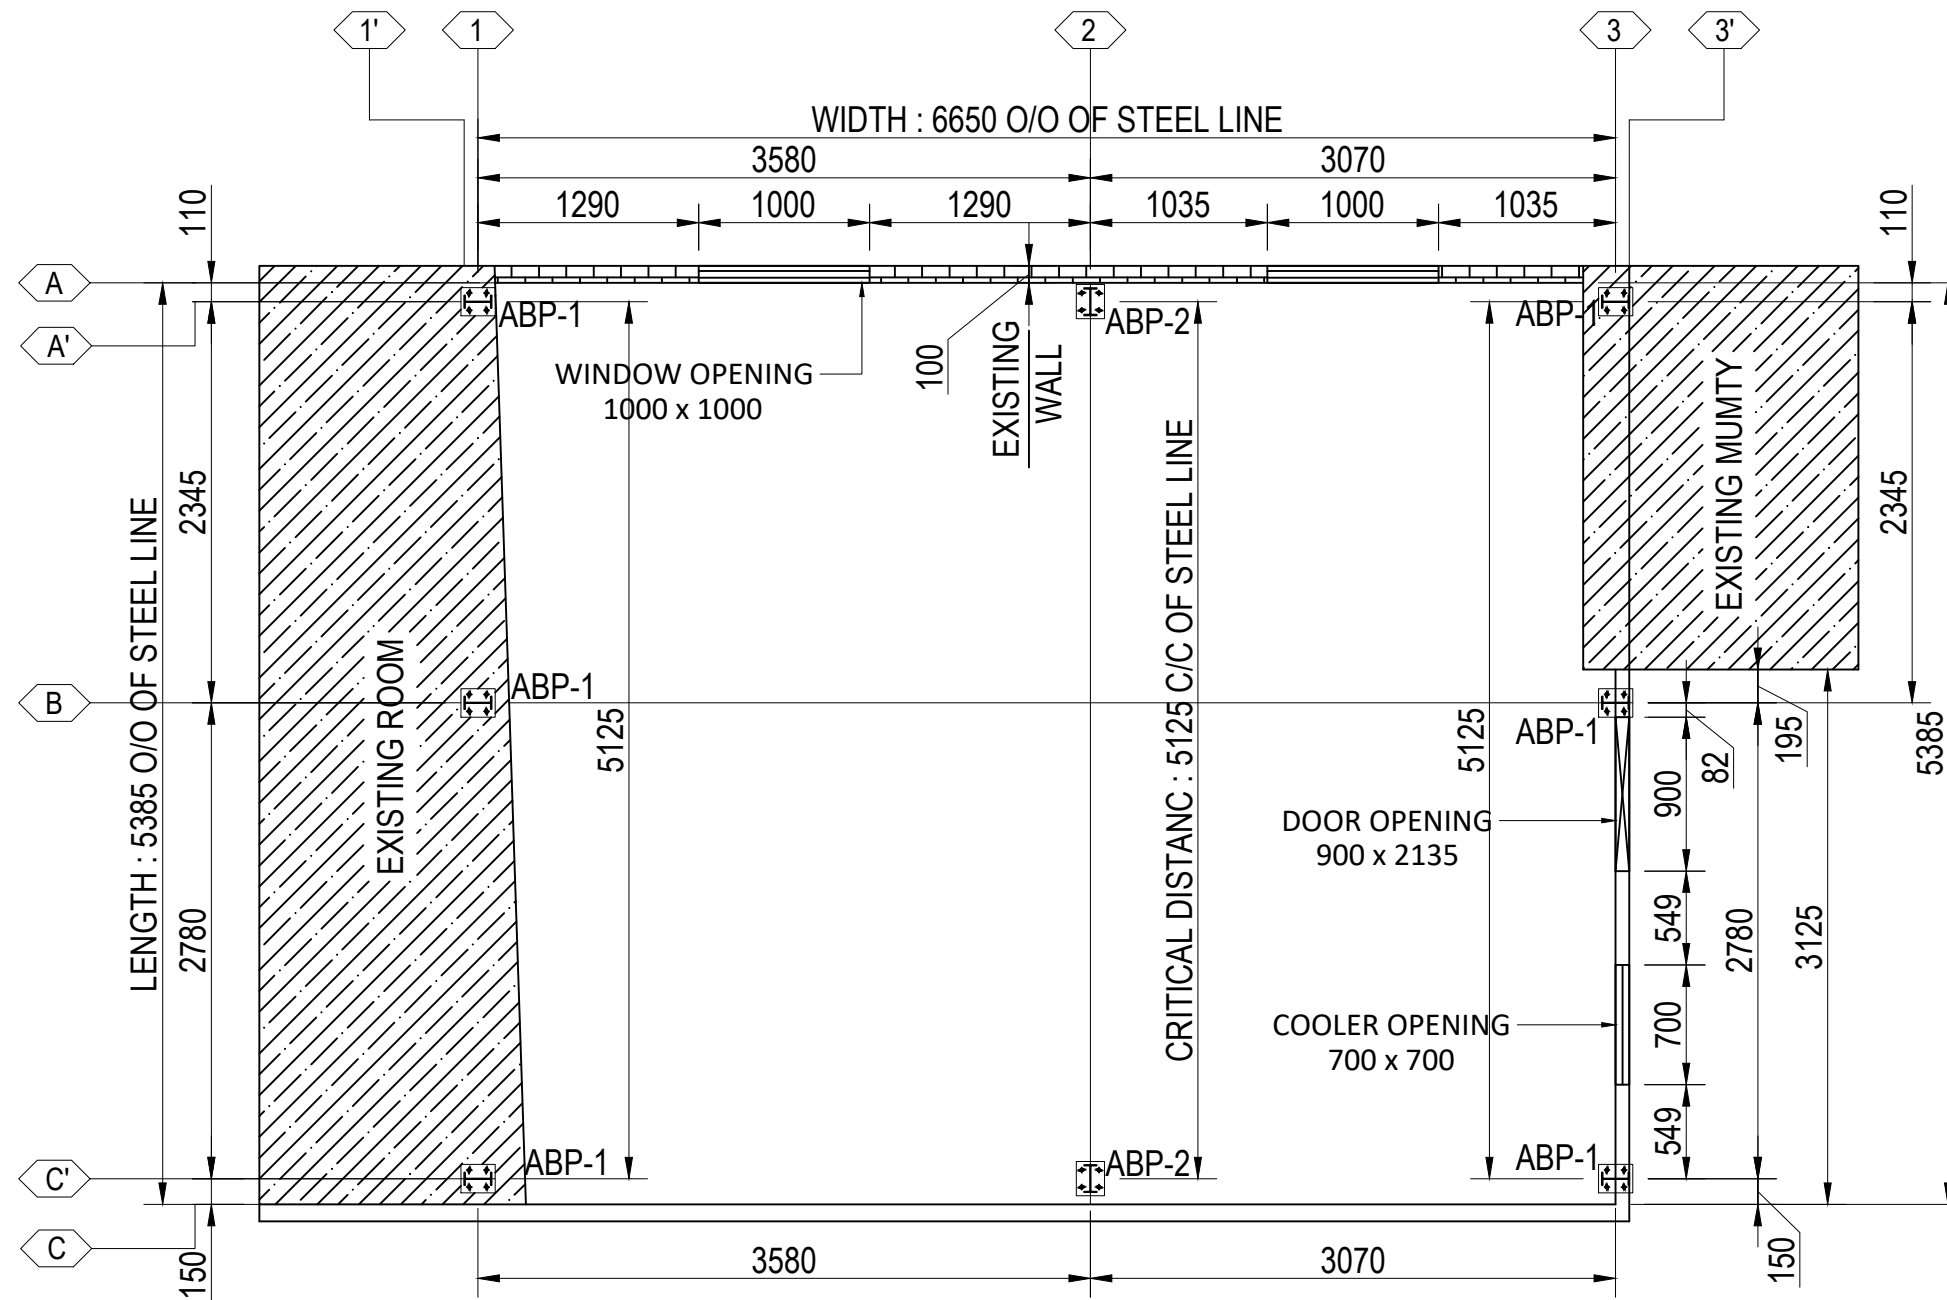

ANCHOR BOLT LAYOUT PLAN
NOTE : ALL CRITICAL DISTANCES ARE
FROM ONE INNER BOLT TO OTHER
INNER BOLT

FOR APPROVAL :

IN ORDER TO SCHEDULE THIS PROJECT IN AN EFFICIENT MANNER , KINDLY RETURN THESE DRAWINGS WITH YOUR ANY CHANGES MADE AFTER THE COMMENTS MARKED IN RED

APPROVAL OF THESE DRAWINGS MAY DELAY THE FABRICATION SCHEDULE AND SUBSEQUENTLY THE DELIVERY OF THE BUILDING.

PLEASE TICK MARK ONLY ONE OF THE FOLLOWING

☐ " APPROVED AS IS "

☐ " APPROVED AS NOTED "

☐ " RESUBMIT AS NOTED "

APPROVE : _____

SIGNATURE: _____

DATE : _____

00	17-05-22	ISSUED FOR APPROVAL	QSM	YEA	YEA
REV.	DATE	DESCRIPTION	DRWN BY	CHK BY	APR BY
MAIMAAR  MAIMAAR STEEL Pvt.Ltd 238, Raiwind Road, Thokar Niaz Baig ,LAHORE, Pakistan E-mail: nasir.abbas@maimaargroup.com E-mail: maimaar.steel@gmail.com Website: www.maimaargroup.com E-mail: nasir.abbas@maimaargroup.com Mob-1 : +(92-300) 807 4017 ,+(92-333) 807 1115					
JOB NO./QUOTE NO.			MSPL-037-22		BLDG #. 01
PROJECT NAME			MAIMAAR SHED		
CUSTOMER					
JOBSITE LOCATION			LAHORE		
ANCHOR BOLT LAYOUT PLAN					DWG. NO. 01