


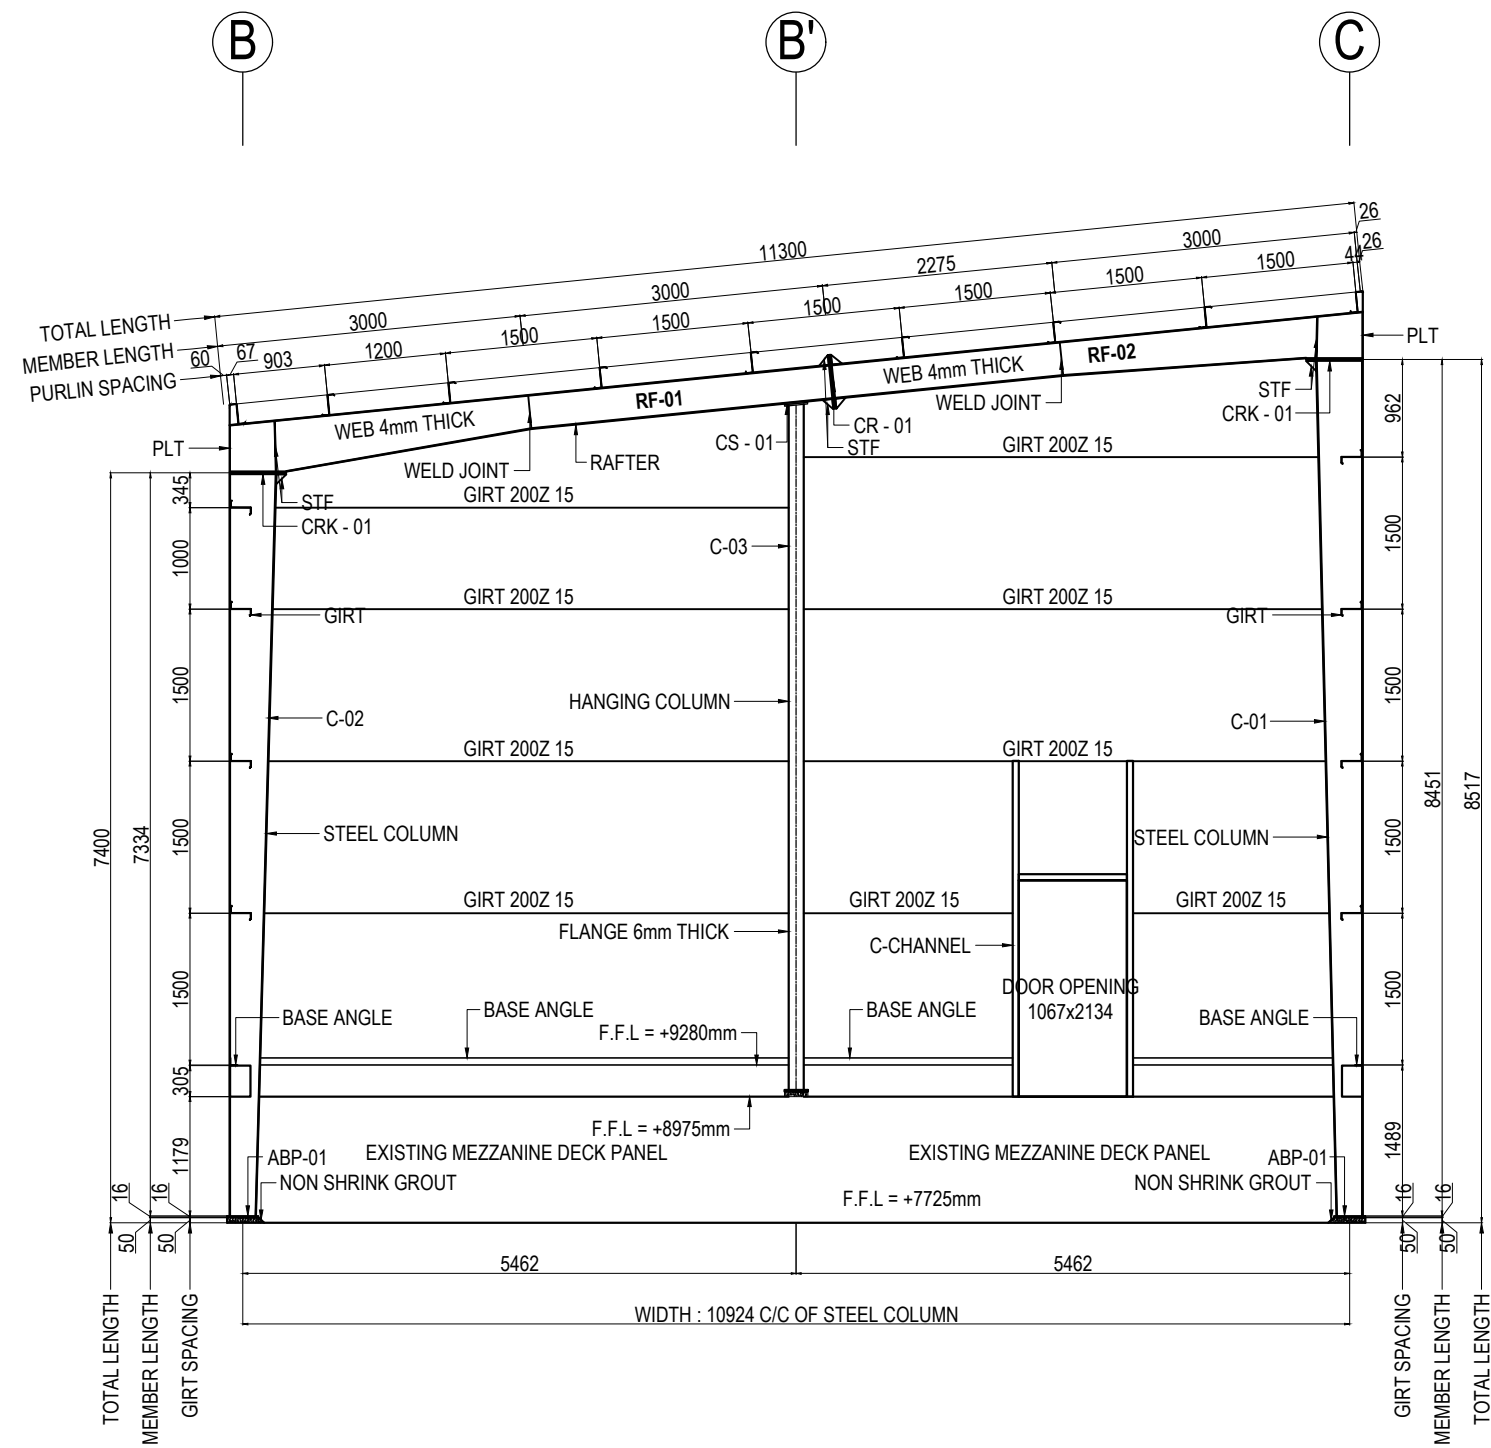

END WALL FRAMING @ GRID - 6

02	16-08-21	ISSUED FOR APPROVAL	FZN	YEA	YEA
01	21-06-21	ISSUED FOR APPROVAL	FZN	YEA	YEA
00	17-06-21	ISSUED FOR APPROVAL	FZN	YEA	YEA
REV.	DATE	DESCRIPTION	DRWN BY	CHK BY	APR BY



MAIMAAR STEEL Pvt.Ltd
 238, Raiwind Road, Thokar Niaz Baig ,LAHORE, Pakistan
 E-mail: nasir.abbas@maimaargroup.com
 E-mail: maimaar.steel@gmail.com
 Website: www.maimaargroup.com
 E-mail: nasir.abbas@maimaargroup.com
 Mob-1 : +(92-300) 807 4017 , +(92-333) 807 1115

JOB NO./QUOTE NO.	MSPL-025	BLDG #.	01
PROJECT NAME	BOILER HOUSE		
CUSTOMER	MAKKAH ENGINEERING		
JOBSITE LOCATION	KARACHI		
END WALL ELEVATION @ GRID - 6			DWG. NO. 13