



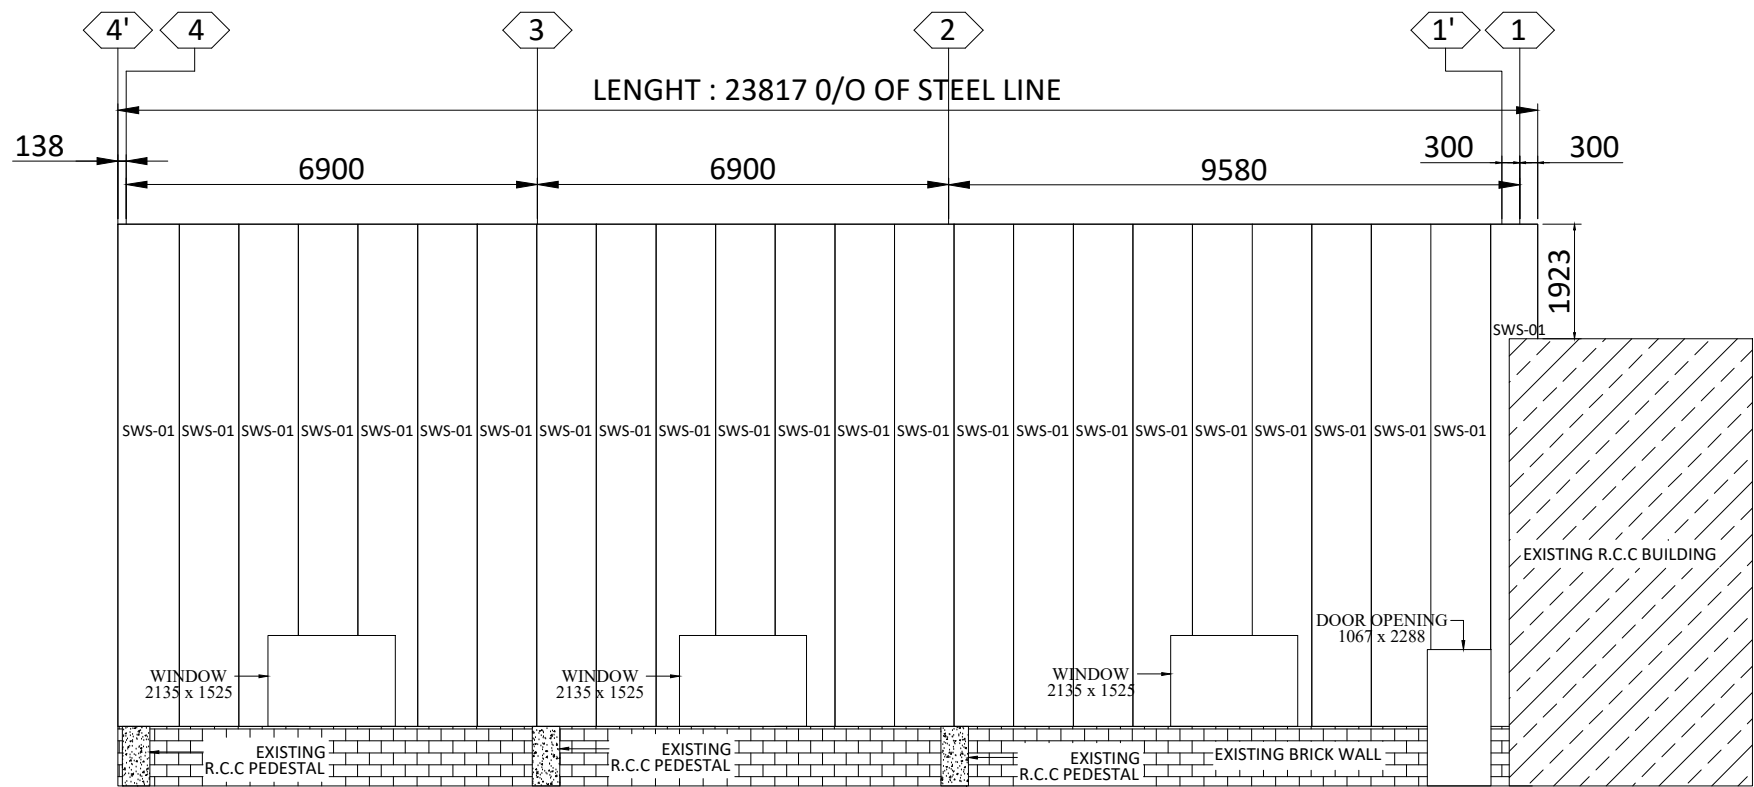

SIDE WALL SHEETING @ GRID - A

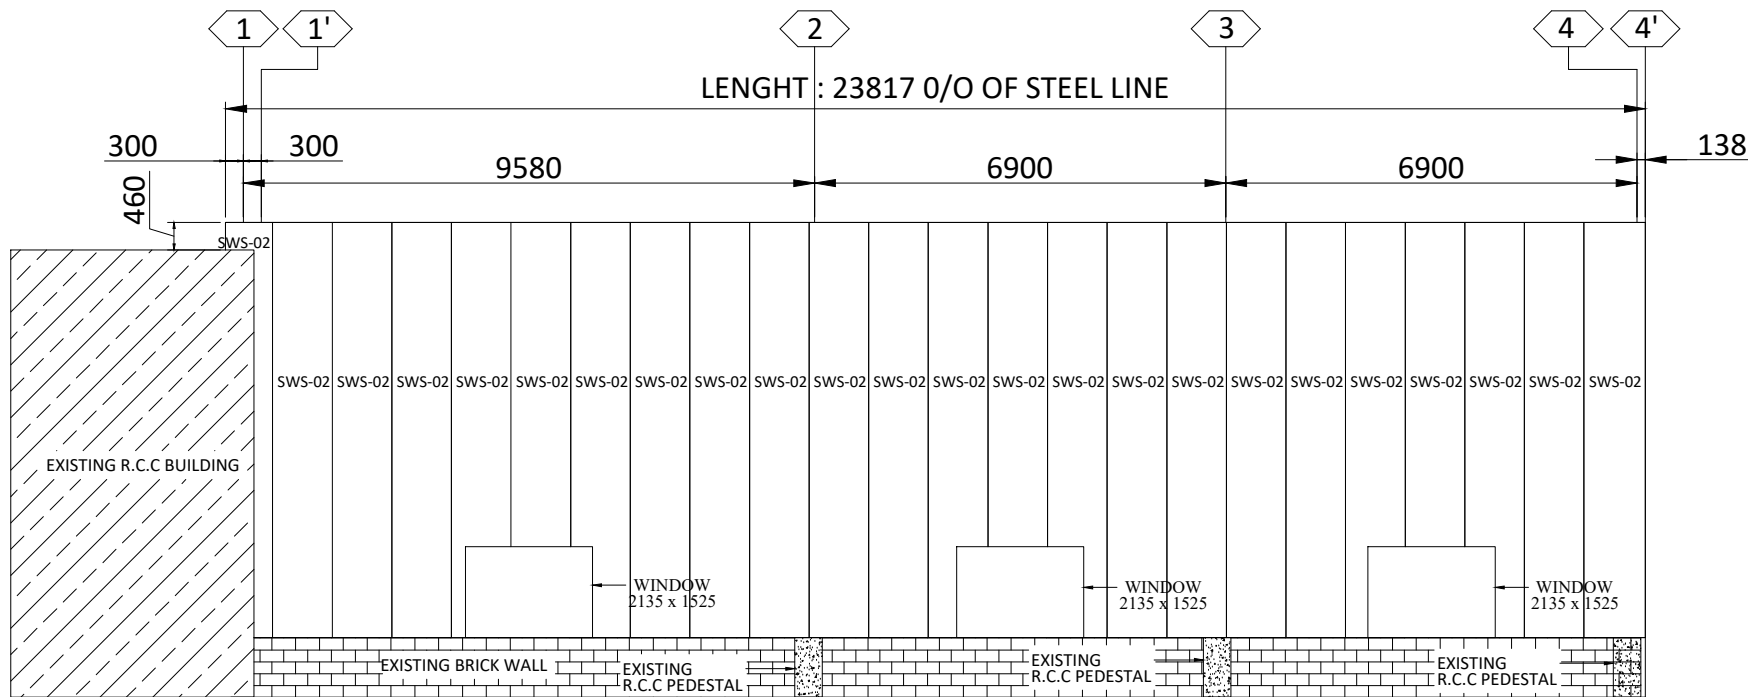

SIDE WALL SHEETING @ GRID - G

NOTE:
WALL SHEETING
0.5mm PPGI SHEETING PANEL
50mm FIBERGLASS INSULATION

FOR APPROVAL :

IN ORDER TO SCHEDULE THIS PROJECT
IN AN EFFICIENT MANNER , KINDLY
RETURN THESE DRAWINGS WITH YOUR
ANY CHANGES MADE AFTER THE
COMMENTS MARKED IN RED
APPROVAL OF THESE DRAWINGS MAY
DELAY THE FABRICATION SCHEDULE AND
SUBSEQUENTLY THE DELIVERY OF THE
BUILDING.
PLEASE TICK MARK ONLY ONE OF THE FOLLOWING

☐ " APPROVED AS IS "

☐ " APPROVED AS NOTED "

☐ " RESUBMIT AS NOTED "

APPROVE : _____

SIGNATURE: _____

DATE : _____

SIDE WALL SHEETING @ GRID -A				
MEMBER TABLE				
PART	MARK	LENGTH	WIDTH	QTY.
SIDE WALL SHEET	SWS-1	8423	1000	24

SIDE WALL SHEETING @ GRID -G				
MEMBER TABLE				
PART	MARK	LENGTH	WIDTH	QTY.
SIDE WALL SHEET	SWS-2	6960	1000	24

00	15-10-22	ISSUED FOR APPROVAL	QSM	YEA	YEA
REV.	DATE	DESCRIPTION	DRWN BY	CHK BY	APR BY

MAIMAAR



MAIMAAR STEEL Pvt.Ltd

238, Raiwind Road, Thokar Niaz Baig ,LAHORE, Pakistan

E-mail: nasir.abbas@maimaargroup.com

E-mail: maimaar.steel@gmail.com

Website: www.maimaargroup.com

E-mail: nasir.abbas@maimaargroup.com

Mob-1 : +(92-300) 807 4017 ,+(92-333) 807 1115

JOB NO.	MSPL-058	BLDG #.	01
PROJECT NAME	WAREHOUSE		
CUSTOMER	MARIA B		
JOBSITE LOCATION	LAHORE		

SIDE WALL SHEETING @ GRID - A & G			DWG. NO.
			09