


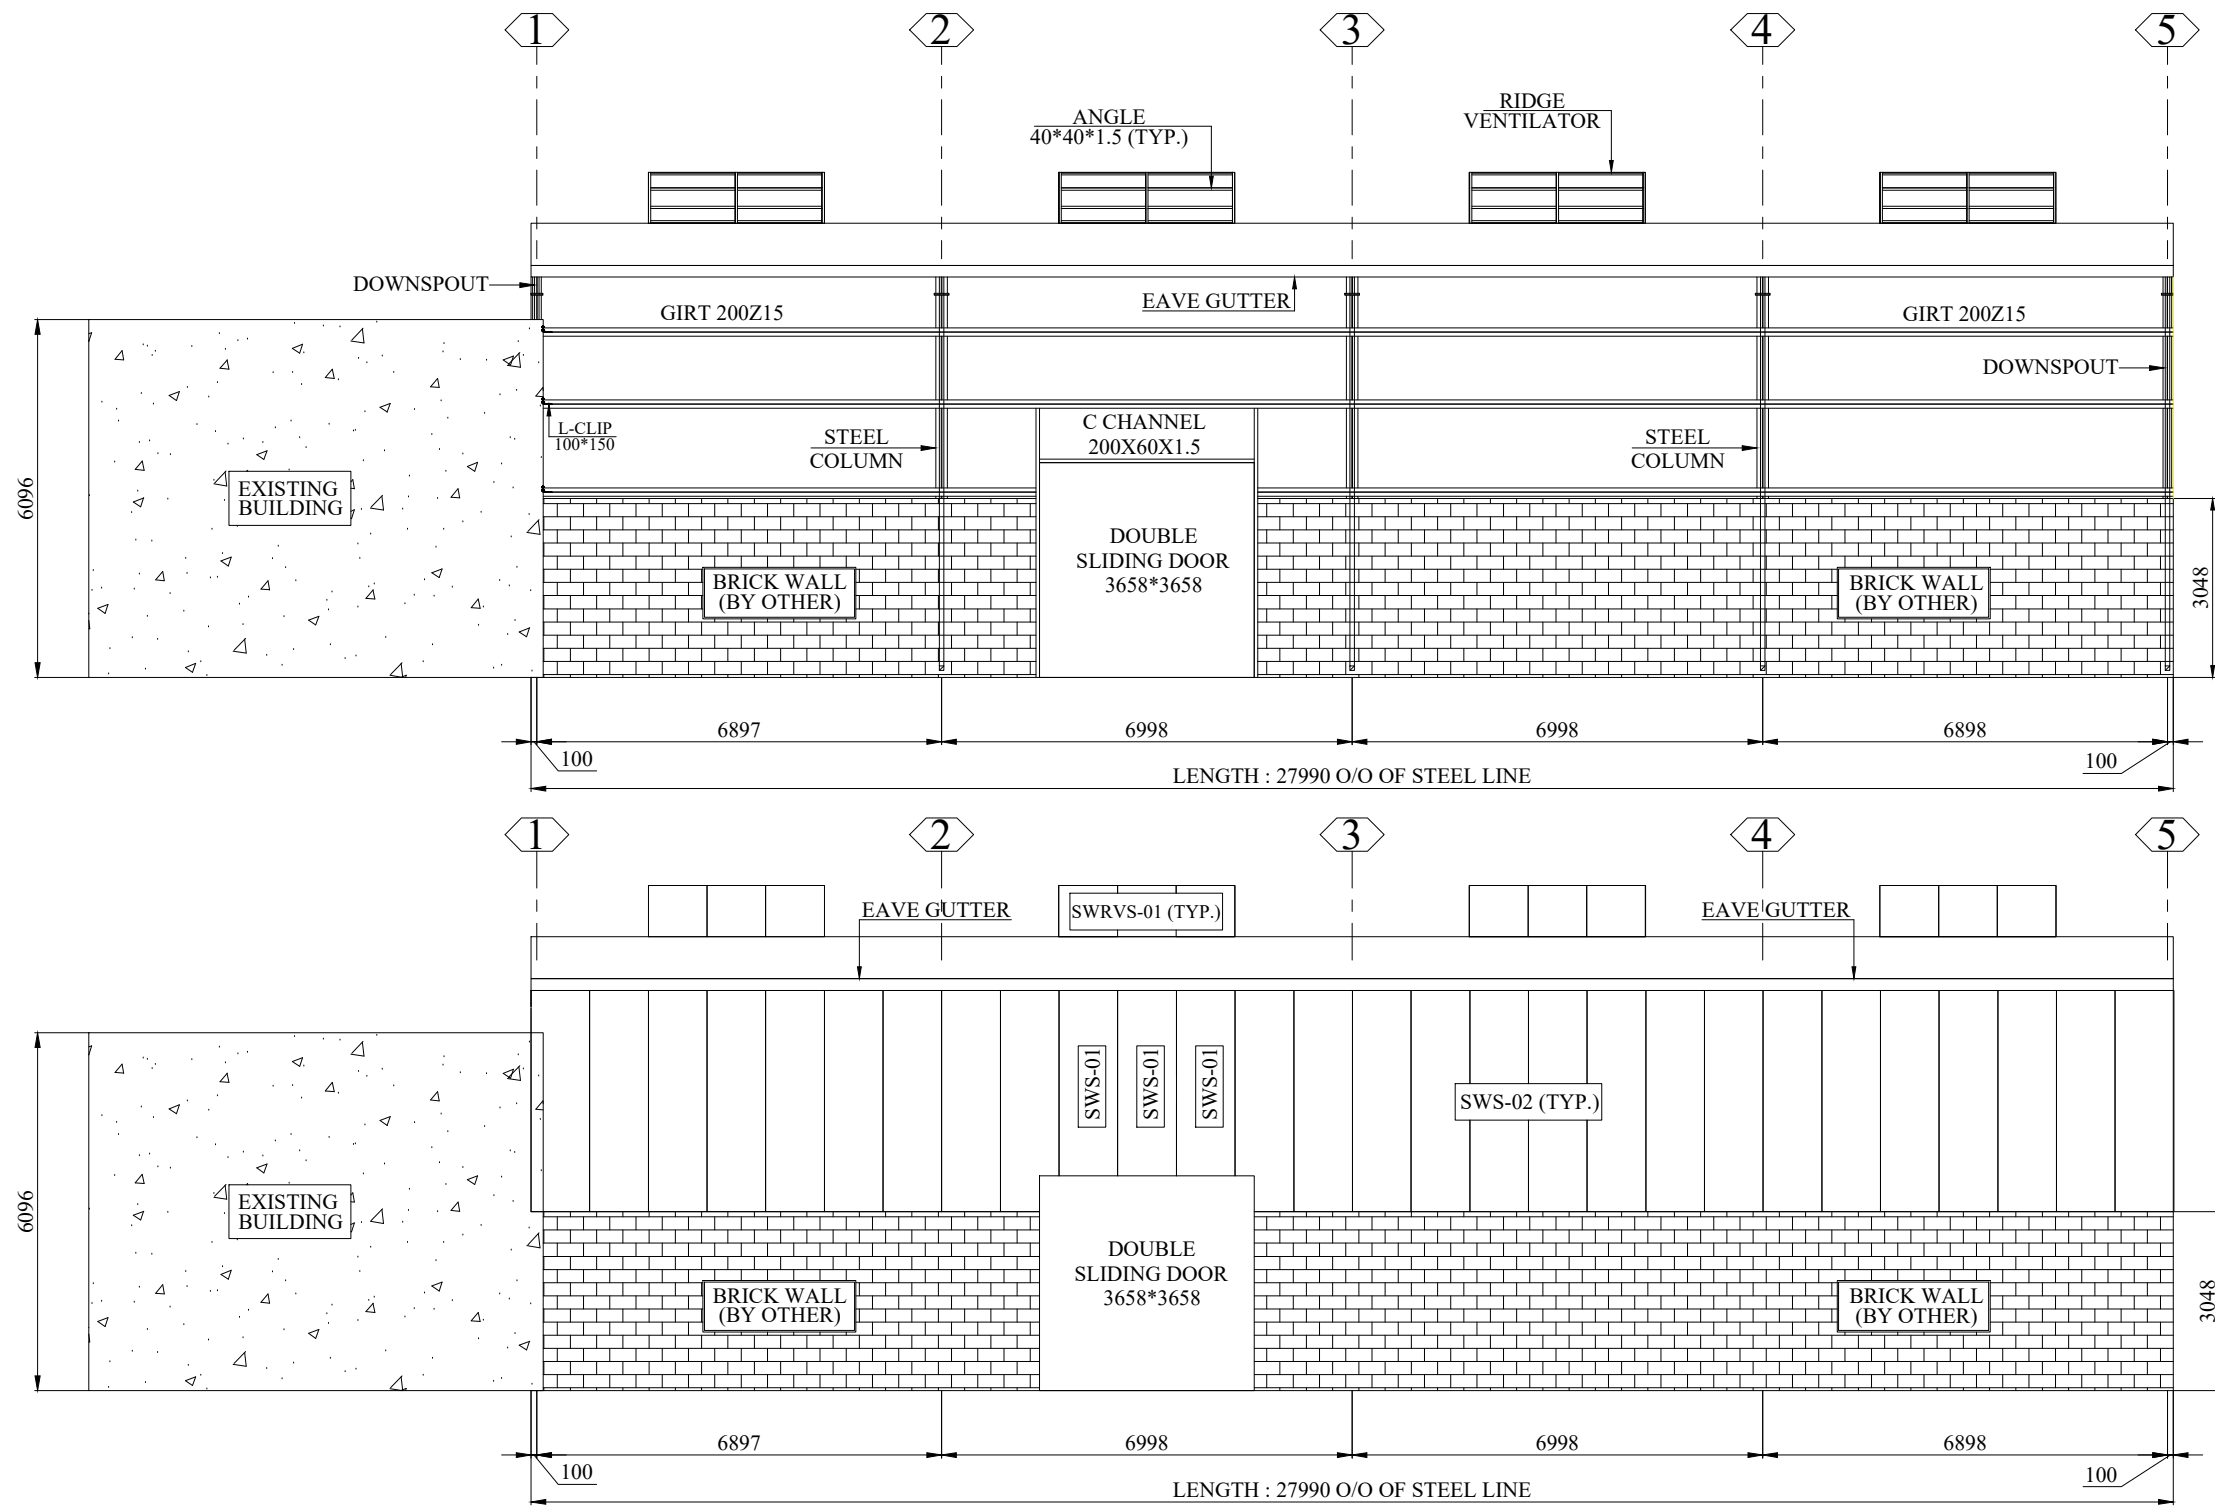


SIDE WALL FRAMING & SHEETING @ GRID - E

NOTE:-
50mm FIBERGLASS INSULATION
0.5mm PPGI SHEETING

SIDE WALL SHEETING

DESCRIPTIONS	PART	LENGTH (MM)	WIDTH (MM)	QUANT ITY
SIDE WALL SHEETING	SWS-01	3,160	1,000	3
SIDE WALL SHEETING	SWS-02	3,770	1,000	25
SIDE WALL ROOF VENTILATOR SHEETING	SWRS-01	872	1,000	12

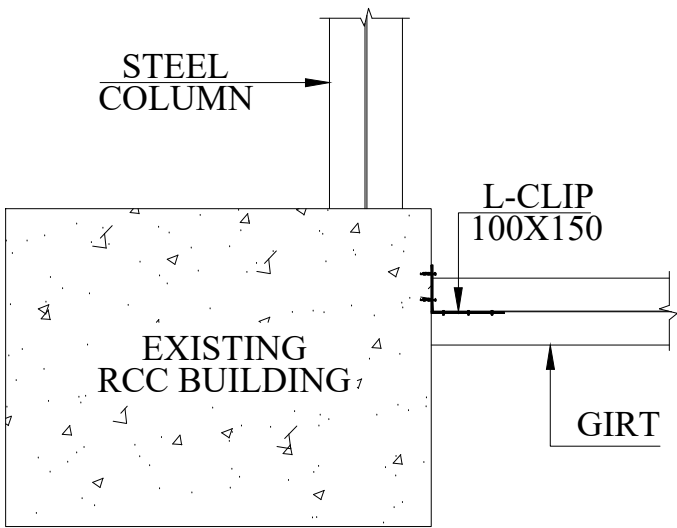

L-CLIP DETAIL

FOR APPROVAL :

IN ORDER TO SCHEDULE THIS PROJECT IN AN EFFICIENT MANNER , KINDLY RETURN THESE DRAWINGS WITH YOUR ANY CHANGES MADE AFTER THE COMMENTS MARKED IN RED

APPROVAL OF THESE DRAWINGS MAY DELAY THE FABRICATION SCHEDULE AND SUBSEQUENTLY THE DELIVERY OF THE BUILDING.

PLEASE TICK MARK ONLY ONE OF THE FOLLOWING

☐ " APPROVED AS IS "

☐ " APPROVED AS NOTED "

☐ " RESUBMIT AS NOTED "

APPROVE : _____

SIGNATURE: _____

DATE : _____

00	08-Oct-24	ISSUED FOR APPROVAL	I.U	M.B	NAS
REV.	DATE	DESCRIPTION	DRWN BY	CHK BY	APR BY



MAIMAAR STEEL Pvt.Ltd
238, Raiwind Road, Thokar Niaz Baig ,LAHORE, Pakistan
E-mail: nasir.abbas@maimaargroup.com
E-mail: maimaar.steel@gmail.com
Website: www.maimaargroup.com
E-mail: nasir.abbas@maimaargroup.com
Mob-1 : +(92-300) 807 4017 ,+(92-333) 807 1115

JOB NO.	MSPL-149	BUILDING #.	01
PROJECT NAME	SUPPLY & INSTALLATION OF CLEAR SPAN GABLE SHED		
CUSTOMER	NIAZ ENTERPRISES		
JOBSITE LOCATION	BHALWAL		

SIDE WALL FRAMING & SHEETING @ GRID - E