


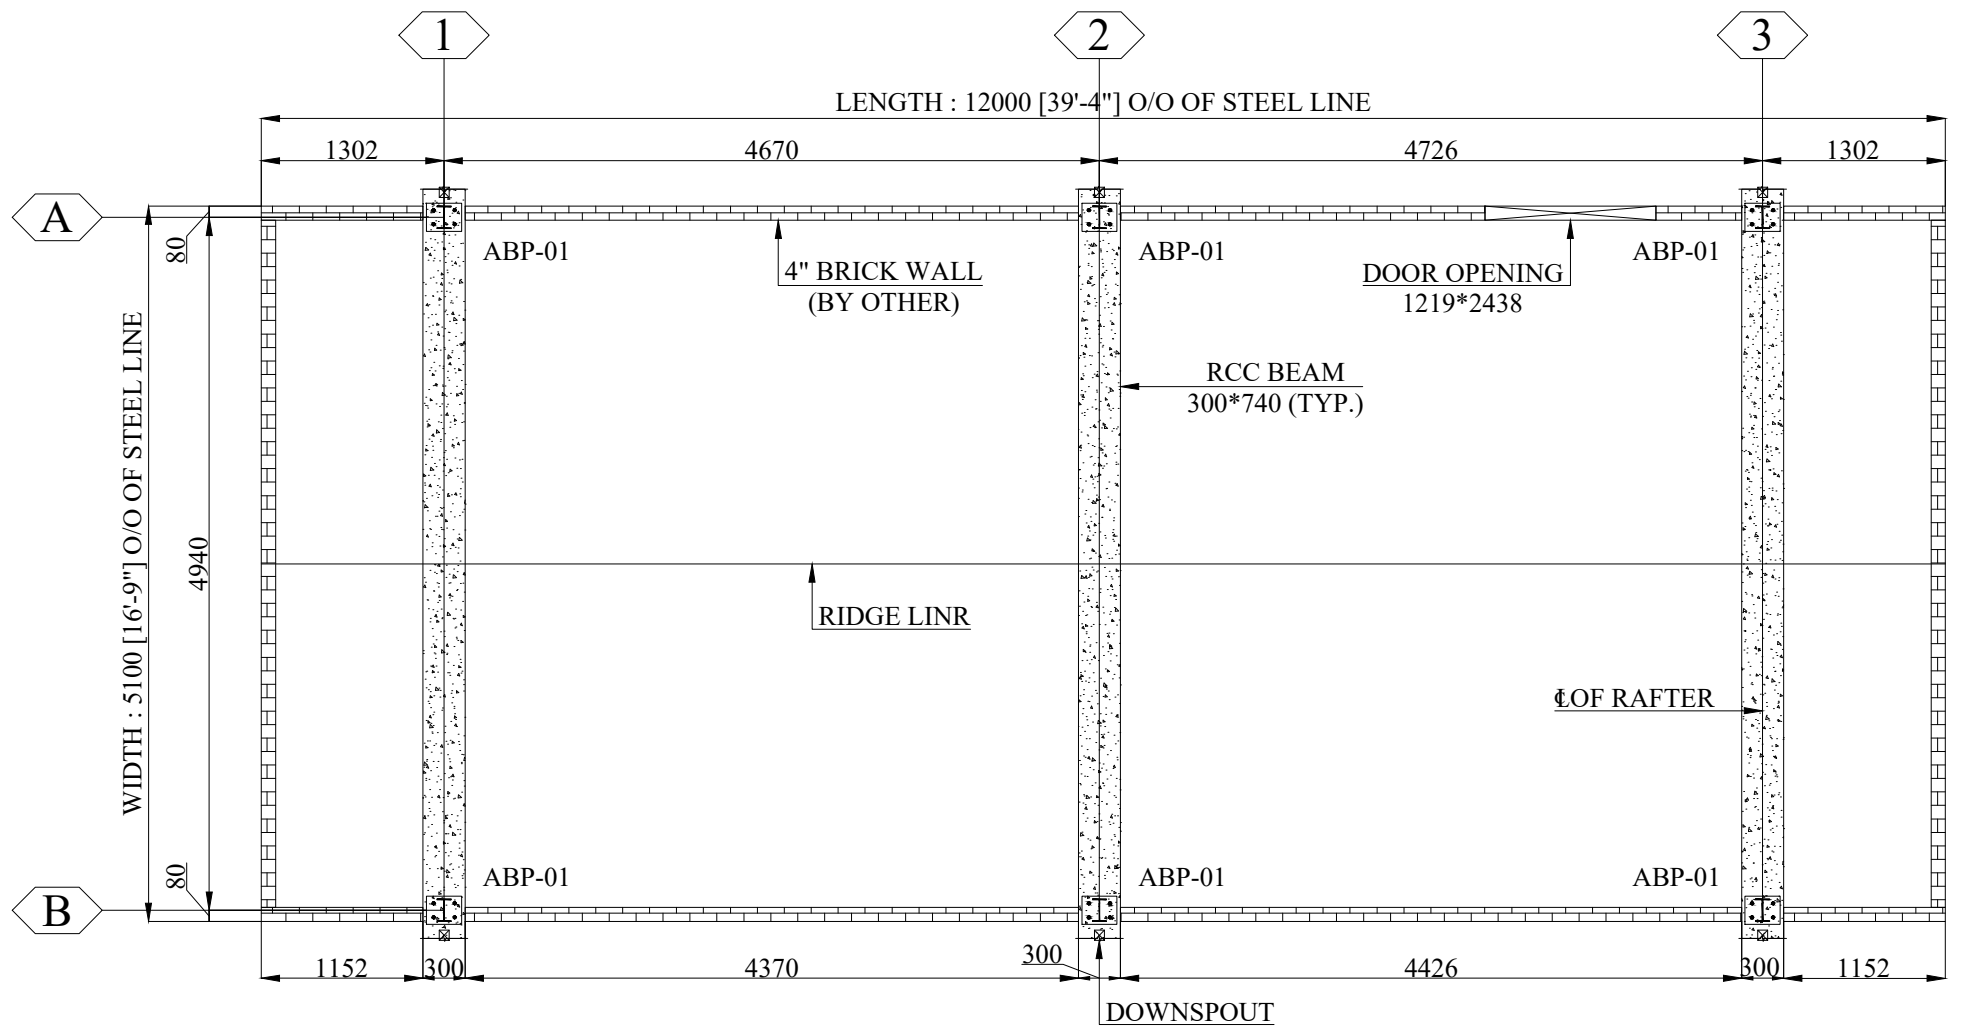

COLUMN LAYOUT PLAN

NOTE :

THE CUSTOMER WILL TELL US WHERE
OUR STARTING POINT WILL BE

BUILDING DESIGN LOADS:

- ☐ LIVE LOAD ON ROOF = .57 KN/SQ.M
- ☐ LIVE LOAD ON FRAME = .57 KN/SQ.M
- ☐ WIND LOAD = 135 KM/HR
- ☐ EXPOSURE = B
- ☐ SEISMIC ZONE AS PER UBC 1997 = 2A
- ☐ RAINFALL INTENSITY FOR DESIGN OF GUTTER & DOWNSPOUT = 150 MM/HR

APPROVE : _____
SIGNATURE: _____
DATE : _____

FOR APPROVAL :

IN ORDER TO SCHEDULE THIS PROJECT
IN AN EFFICIENT MANNER , KINDLY
RETURN THESE DRAWINGS WITH YOUR
ANY CHANGES MADE AFTER THE
COMMENTS MARKED IN RED
APPROVAL OF THESE DRAWINGS MAY
DELAY THE FABRICATION SCHEDULE AND
SUBSEQUENTLY THE DELIVERY OF THE
BUILDING.
PLEASE TICK MARK ONLY ONE OF THE FOLLOWING

- ☐ " APPROVED AS IS "
- ☐ " APPROVED AS NOTED "
- ☐ " RESUBMIT AS NOTED "

APPROVE : _____
SIGNATURE: _____
DATE : _____

00	07-Sep-24	ISSUED FOR APPROVAL	I.U	M.B	NAS
REV.	DATE	DESCRIPTION	DRWN BY	CHK BY	APR BY



MAIMAAR STEEL Pvt.Ltd
238, Raiwind Road, Thokar Niaz Baig ,LAHORE, Pakistan
E-mail: nasir.abbas@maimaargroup.com
E-mail: maimaar.steel@gmail.com
Website: www.maimaargroup.com
E-mail: nasir.abbas@maimaargroup.com
Mob-1 : +(92-300) 807 4017 ,+(92-333) 807 1115

JOB NO.	MSPL-144	UNIT #.	05
PROJECT NAME	INVERTER ROOM		
CUSTOMER	NISHAT POWER		
JOBSITE LOCATION	FAISALABAD		

COLUMN LAYOUT PLAN

DWG. NO.

01