
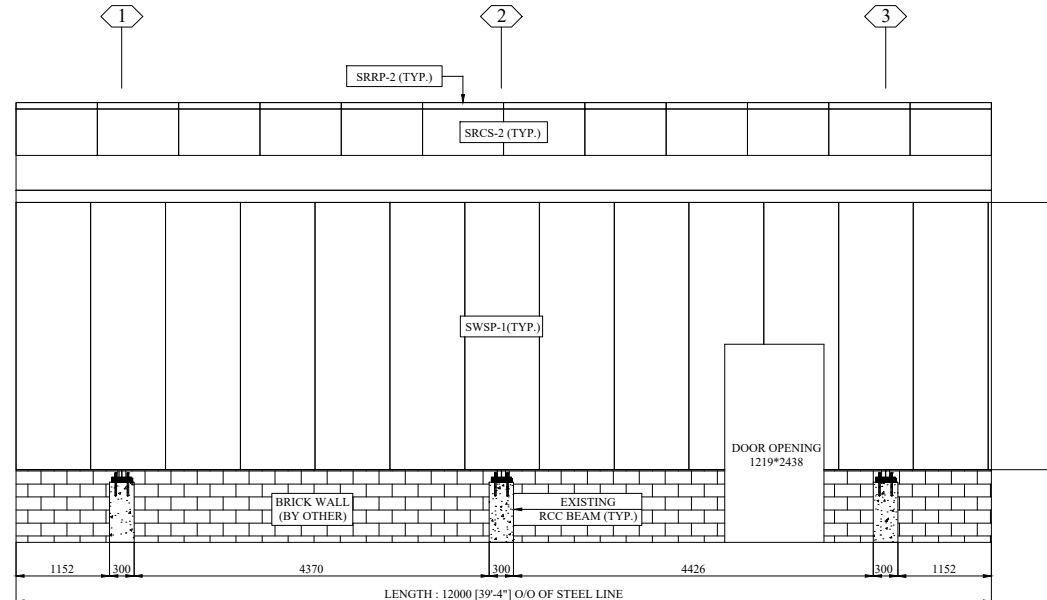


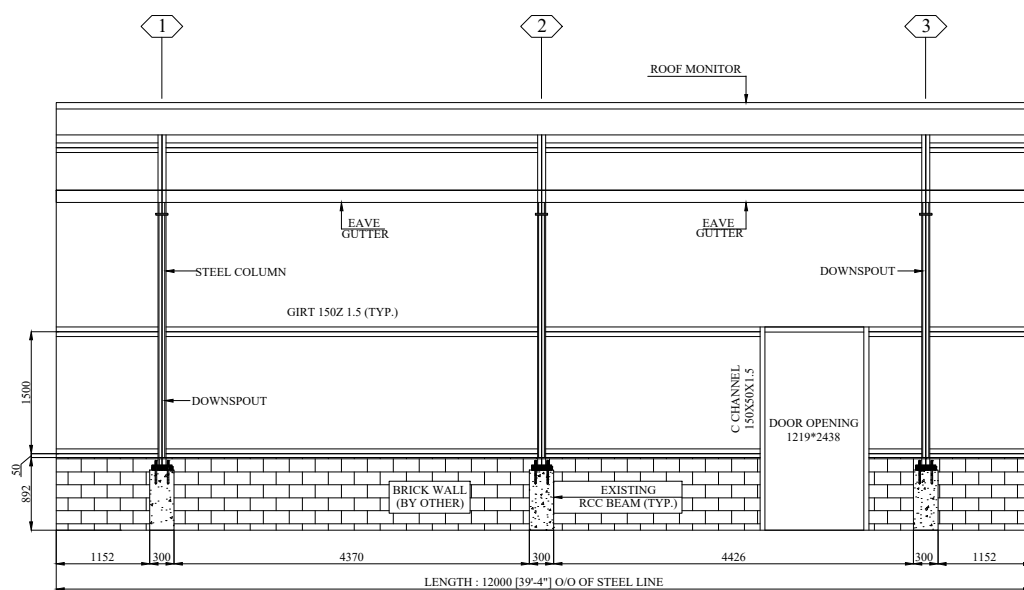

SIDE WALL FRAMING & SANDWICH PANEL & SHEETING @ GRID - A

SIDE WALL SANDWICH PANEL & ROOF CURVE SHEETING & ROOF RIDGE PANEL				
DESCRIPTIONS	PART	LENGTH (MM)	WIDTH (MM)	QUANTITY
SIDE WALL SANDWICH PANEL	SWSP-01	3,289	920	14
SIDE ROOF CURVE SHEETING	SRCS-01	571	1,000	12
SIDE ROOF RIDGE PANEL	SRRP-01	76	1,000	12

FOR APPROVAL :

IN ORDER TO SCHEDULE THIS PROJECT IN AN EFFICIENT MANNER , KINDLY RETURN THESE DRAWINGS WITH YOUR ANY CHANGES MADE AFTER THE COMMENTS MARKED IN RED APPROVAL OF THESE DRAWINGS MAY DELAY THE FABRICATION SCHEDULE AND SUBSEQUENTLY THE DELIVERY OF THE BUILDING.
PLEASE TICK MARK ONLY ONE OF THE FOLLOWING

☐ " APPROVED AS IS "
☐ " APPROVED AS NOTED "
☐ " RESUBMIT AS NOTED "

APPROVE : _____

SIGNATURE: _____

DATE : _____

00	07-Sep-24	ISSUED FOR APPROVAL	I.U	M.B	NAS
REV.	DATE	DESCRIPTION	DRWN BY	CHK BY	APR BY



MAIMAAR STEEL Pvt.Ltd
 238, Raiwind Road, Thokar Niaz Baig ,LAHORE, Pakistan
 E-mail: nasir.abbas@maimaargroup.com
 E-mail: maimaar.steel@gmail.com
 Website: www.maimaargroup.com
 E-mail: nasir.abbas@maimaargroup.com
 Mob-1 : +(92-300) 807 4017 , +(92-333) 807 1115

JOB NO.	MSPL-144	UNIT #.	05
PROJECT NAME	INVERTER ROOM		
CUSTOMER	NISHAT POWER		
JOBSITE LOCATION	FAISALABAD		
SIDE WALL FRAMING & SANDWICH PANEL & SHEETING @ GRID - A			DWG. NO. 10