


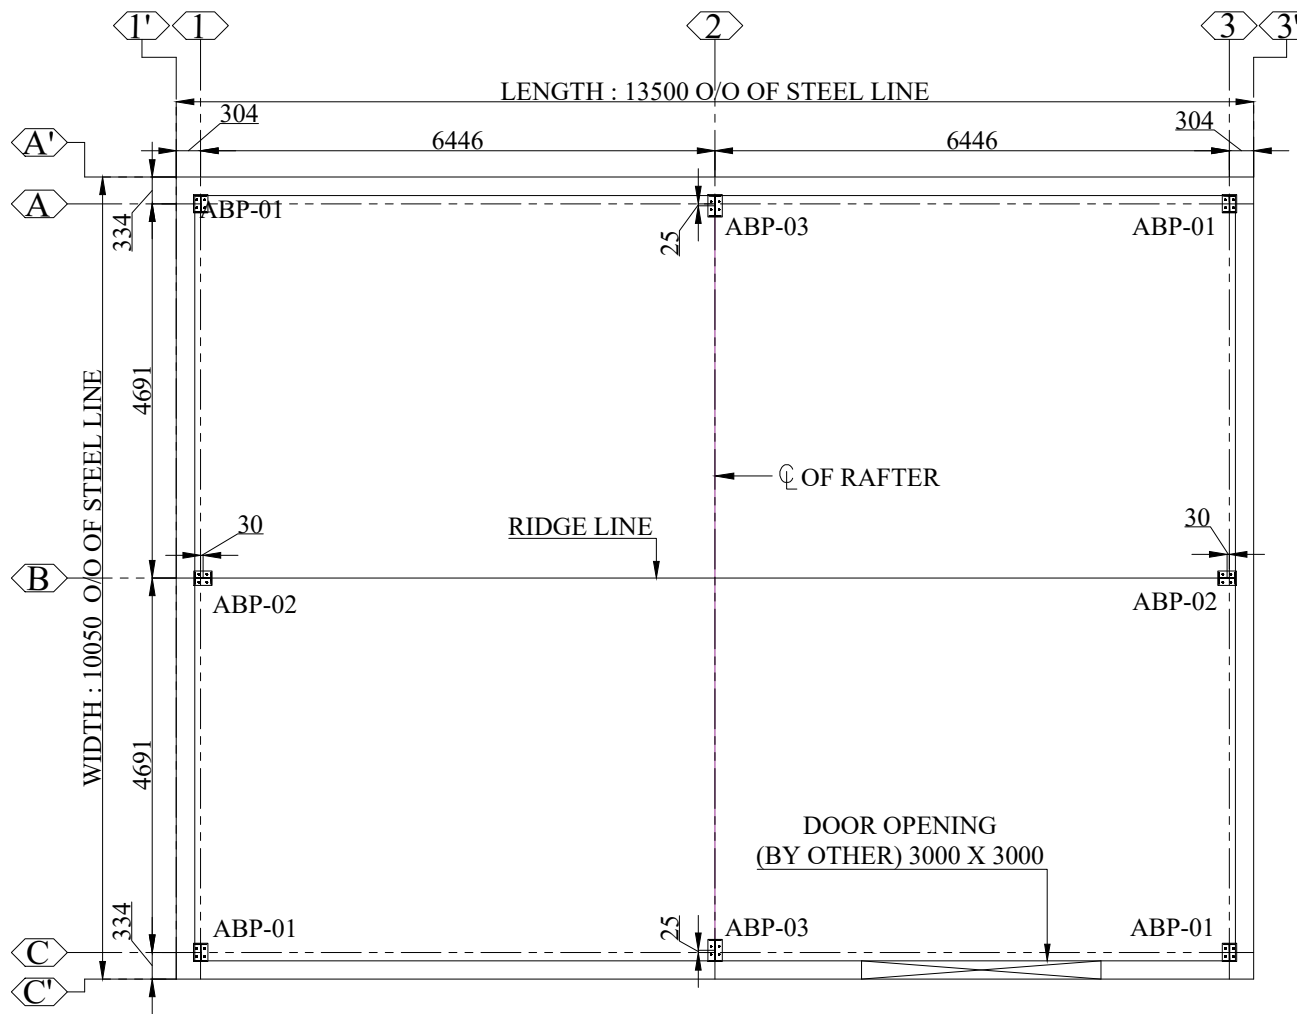

ANCHOR BOLT PLAN

BUILDING DESIGN LOADS:

- ☐ LIVE LOAD = 0.57 KN/SQ.M
☐ WIND SPEED = 160 KM/HR
☐ EXPOSURE = B

APPROVE : _____

SIGNATURE: _____

DATE : _____

FOR APPROVAL :

IN ORDER TO SCHEDULE THIS PROJECT
 IN AN EFFICIENT MANNER , KINDLY
 RETURN THESE DRAWINGS WITH YOUR
 ANY CHANGES MADE AFTER THE
 COMMENTS MARKED IN RED

APPROVAL OF THESE DRAWINGS MAY
 DELAY THE FABRICATION SCHEDULE AND
 SUBSEQUENTLY THE DELIVERY OF THE
 BUILDING.

PLEASE TICK MARK ONLY ONE OF THE FOLLOWING

- ☐ " APPROVED AS IS "
☐ " APPROVED AS NOTED "
☐ " RESUBMIT AS NOTED "

APPROVE : _____

SIGNATURE: _____

DATE : _____

02	12/12/25	ISSUED FOR APPROVAL	M.A	M.B	NAS
REV.	DATE	DESCRIPTION	DRWN BY	CHK BY	APR BY



MAIMAAR STEEL Pvt.Ltd

238, Raiwind Road, Thokar Niaz Baig ,LAHORE, Pakistan

E-mail: nasir.abbas@maimaargroup.com

E-mail: maimaar.steel@gmail.com

Website: www.maimaargroup.com

E-mail: nasir.abbas@maimaargroup.com

Mob-1 : +(92-300) 807 4017 ,+(92-333) 807 1115

JOB NO.	MSPL-214	BUILDING #.	01
PROJECT NAME	FABRIC GODOWN STEEL BUILDING EXTENSION		
CUSTOMER	NISHAT		
JOB SITE LOCATION	LAHORE		

ANCHOR BOLT PLAN

DWG. NO.

02