
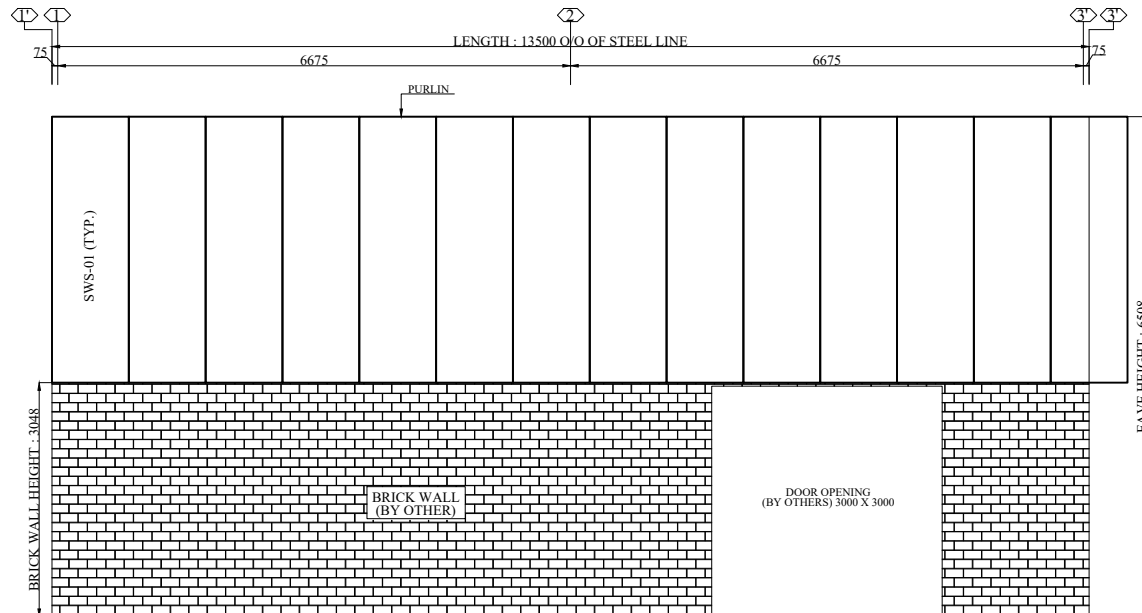


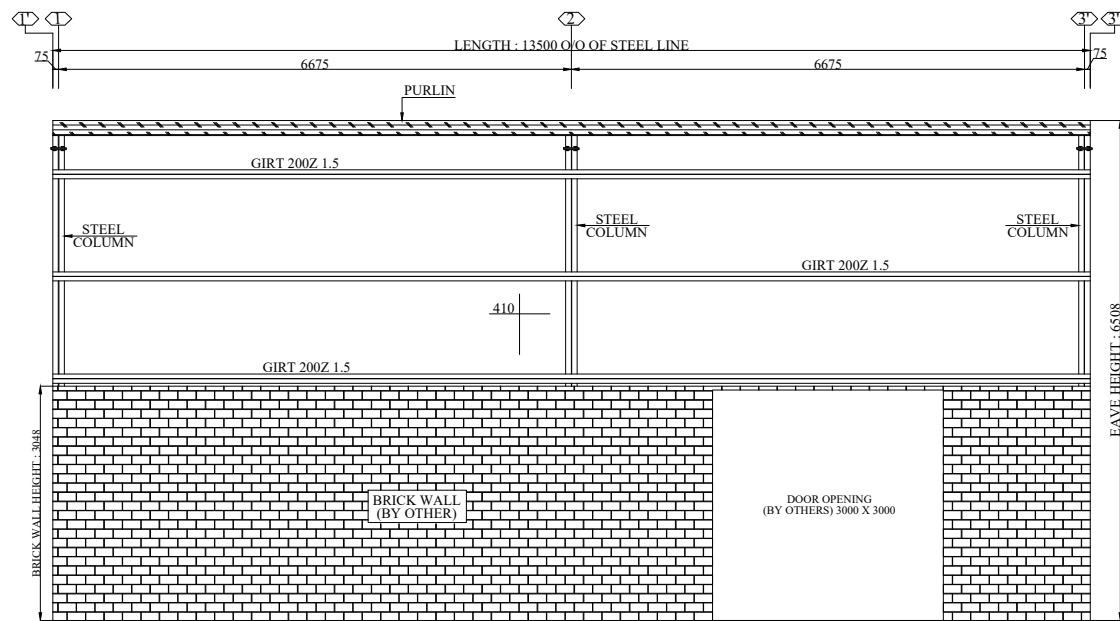

## WALL CLADDING 0.5mm ALUZINC SHEETING PANEL WITH 50mm FIBER GLASS INSULATION

## SIDE WALL FRAMING & SHEETING @ G.L -C'

### SIDE WALL SHEETING @ GL- C'

| DESCRIPTIONS       | PART   | LENGTH<br>(MM) | WIDTH<br>(MM) | QUANTITY |
|--------------------|--------|----------------|---------------|----------|
| SIDE WALL SHEETING | SWS-01 | 3,460          | 1,000         | 14       |

### FOR APPROVAL :

IN ORDER TO SCHEDULE THIS PROJECT  
IN AN EFFICIENT MANNER , KINDLY  
RETURN THESE DRAWINGS WITH YOUR  
ANY CHANGES MADE AFTER THE  
COMMENTS MARKED IN RED

APPROVAL OF THESE DRAWINGS MAY  
DELAY THE FABRICATION SCHEDULE AND  
SUBSEQUENTLY THE DELIVERY OF THE  
BUILDING.

PLEASE TICK MARK ONLY ONE OF THE FOLLOWING

- ☐ " APPROVED AS IS "
- ☐ " APPROVED AS NOTED "
- ☐ " RESUBMIT AS NOTED "

APPROVE : \_\_\_\_\_

SIGNATURE: \_\_\_\_\_

DATE : \_\_\_\_\_

|      |          |                     |         |        |        |
|------|----------|---------------------|---------|--------|--------|
| 00   | 03/12/25 | ISSUED FOR APPROVAL | M.A     | M.B    | NAS    |
| REV. | DATE     | DESCRIPTION         | DRWN BY | CHK BY | APR BY |



MAIMAAR STEEL Pvt.Ltd

238, Raiwind Road, Thokar Niaz Baig ,LAHORE, Pakistan

E-mail: nasir.abbas@maimaargroup.com

E-mail: maimaar.steel@gmail.com

Website: www.maimaargroup.com

E-mail: nasir.abbas@maimaargroup.com

Mob-1 : +(92-300) 807 4017 ,+(92-333) 807 1115

|                   |                                        |             |    |
|-------------------|----------------------------------------|-------------|----|
| JOB NO.           | MSPL-214                               | BUILDING #. | 01 |
| PROJECT NAME      | FABRIC GODOWN STEEL BUILDING EXTENSION |             |    |
| CUSTOMER          | NISHAT                                 |             |    |
| JOB SITE LOCATION | LAHORE                                 |             |    |

## SIDE WALL FRAMING & SHEETING @ G.L -C'

DWG. NO.

13