
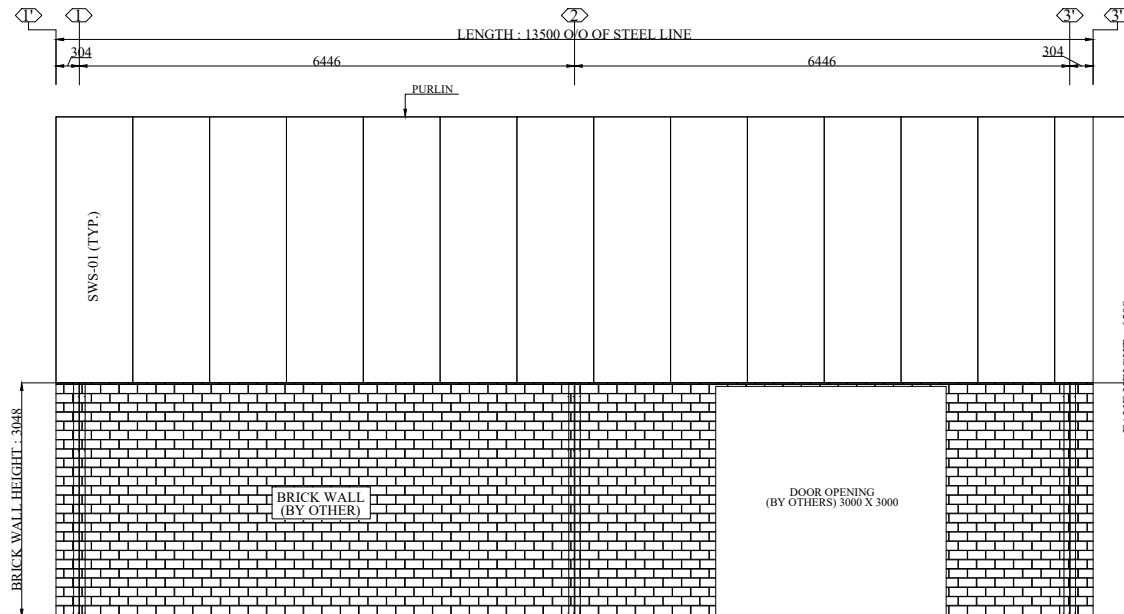


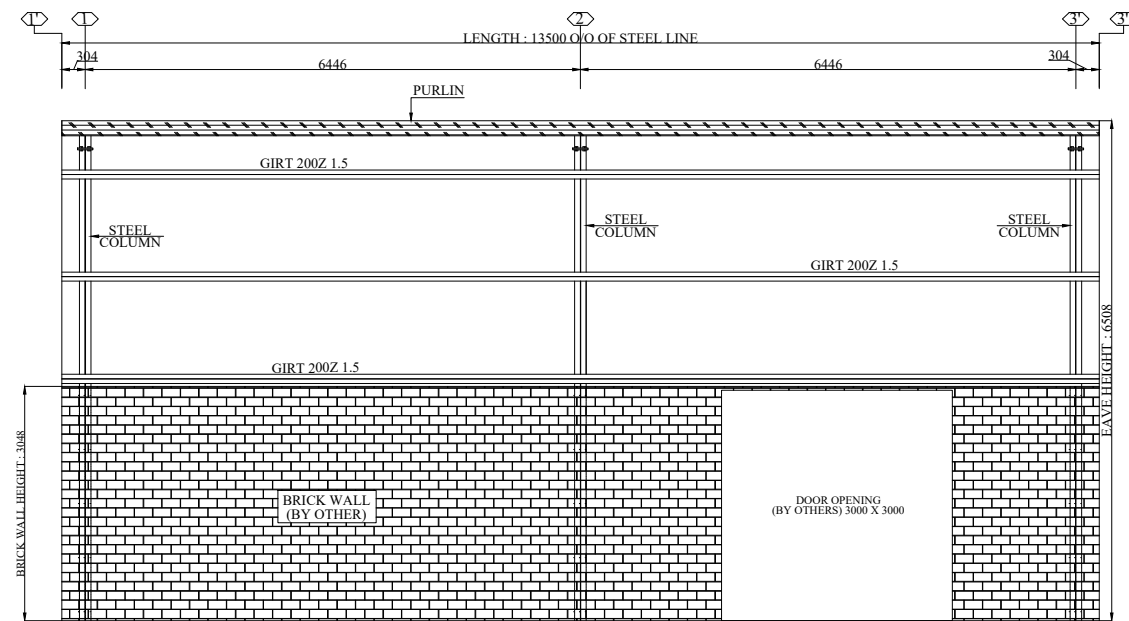

WALL CLADDING 0.5mm ALUZINC SHEETING PANEL WITH 50mm FIBER GLASS INSULATION

SIDE WALL SHEETING @ GL- C'

DESCRIPTIONS	PART	LENGTH (MM)	WIDTH (MM)	QUANTITY
SIDE WALL SHEETING	SWS-01	3,460	1,000	14

SIDE WALL FRAMING & SHEETING @ G.L -C'

FOR APPROVAL :

IN ORDER TO SCHEDULE THIS PROJECT
IN AN EFFICIENT MANNER , KINDLY
RETURN THESE DRAWINGS WITH YOUR
ANY CHANGES MADE AFTER THE
COMMENTS MARKED IN RED
APPROVAL OF THESE DRAWINGS MAY
DELAY THE FABRICATION SCHEDULE AND
SUBSEQUENTLY THE DELIVERY OF THE
BUILDING.
PLEASE TICK MARK ONLY ONE OF THE FOLLOWING

- ☐ " APPROVED AS IS "
- ☐ " APPROVED AS NOTED "
- ☐ " RESUBMIT AS NOTED "

APPROVE : _____

SIGNATURE: _____

DATE : _____

REV.	DATE	DESCRIPTION	DRWN BY	CHK BY	APR BY
02	12/12/25	ISSUED FOR APPROVAL	M.A	M.B	NAS



MAIMAAR STEEL Pvt.Ltd

238, Raiwind Road, Thokar Niaz Baig ,LAHORE, Pakistan
E-mail: nasir.abbas@maimaargroup.com
E-mail: maimaar.steel@gmail.com
Website: www.maimaargroup.com
E-mail: nasir.abbas@maimaargroup.com
Mob-1 : +(92-300) 807 4017 ,+(92-333) 807 1115

JOB NO.	MSPL-214	BUILDING #.	01
PROJECT NAME	FABRIC GODOWN STEEL BUILDING EXTENSION		
CUSTOMER	NISHAT		
JOB SITE LOCATION	LAHORE		

SIDE WALL FRAMING & SHEETING @ G.L -C'

DWG. NO.

14