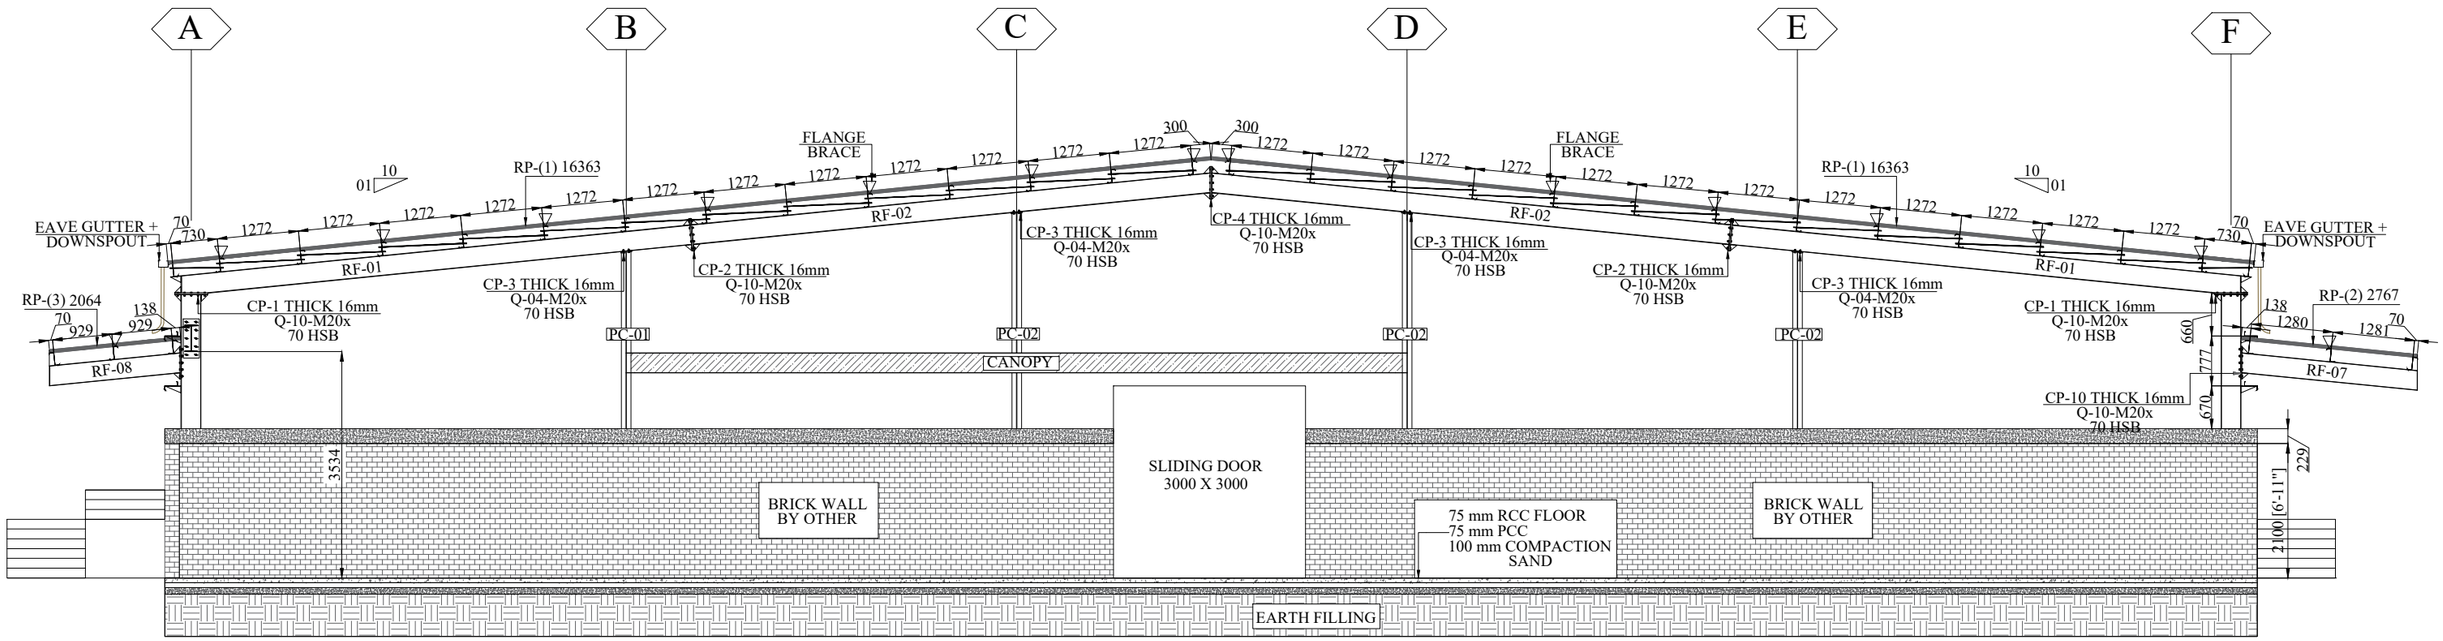


# ELEVATION @ GRID-07

FOR APPROVAL :

IN ORDER TO SCHEDULE THIS PROJECT IN AN EFFICIENT MANNER , KINDLY RETURN THESE DRAWINGS WITH YOUR ANY CHANGES MADE AFTER THE COMMENTS MARKED IN RED APPROVAL OF THESE DRAWINGS MAY DELAY THE FABRICATION SCHEDULE AND SUBSEQUENTLY THE DELIVERY OF THE BUILDING.

PLEASE TICK MARK ONLY ONE OF THE FOLLOWIMG

☐ " APPROVED AS IS "
☐ " APPROVED AS NOTED"
☐ " RESUBMIT AS NOTED "

APPROVE : _____

SIGNATURE: _____

DATE : _____

| REV | DATE | DESCRIPTION | DRAWN BY | CHK BY | APR BY |
|---|---|---|---|---|---|
| 06 | 05-Sep-24 | ISSUED FOR APPROVAL | IU | KAS | NAS |

MAIMAAR

MAIMAAR STEEL Pvt.Ltd
238, Raiwind Road, Thokar Niaz Baig, Lahore, Pakistan
E-mail: nasir.abbas@maimaargroup.com
E-mail: maimaar.steel@gmail.com
Website: www.maimaargroup.com
E-mail: info@maimaargroup.com
Mob-1 : +(92-300) 807 4017 ,+(92-333) 807 1115

| | | | |
|---|---|---|---|
| JOB NO./QUOTE NO. | MSPL-135 | BUILDING # | 01 |
| PROJECT NAME | DRY FRUITS PROCESSING DERA ISMAIL KHAN | | |
| CUSTOMER | 45 ENGINEER DIVISION | | |
| JOB SITE LOCATION | DERA ISMAIL KHAN | | |

ELEVATION @ GRID-07

DWG NO. E05