



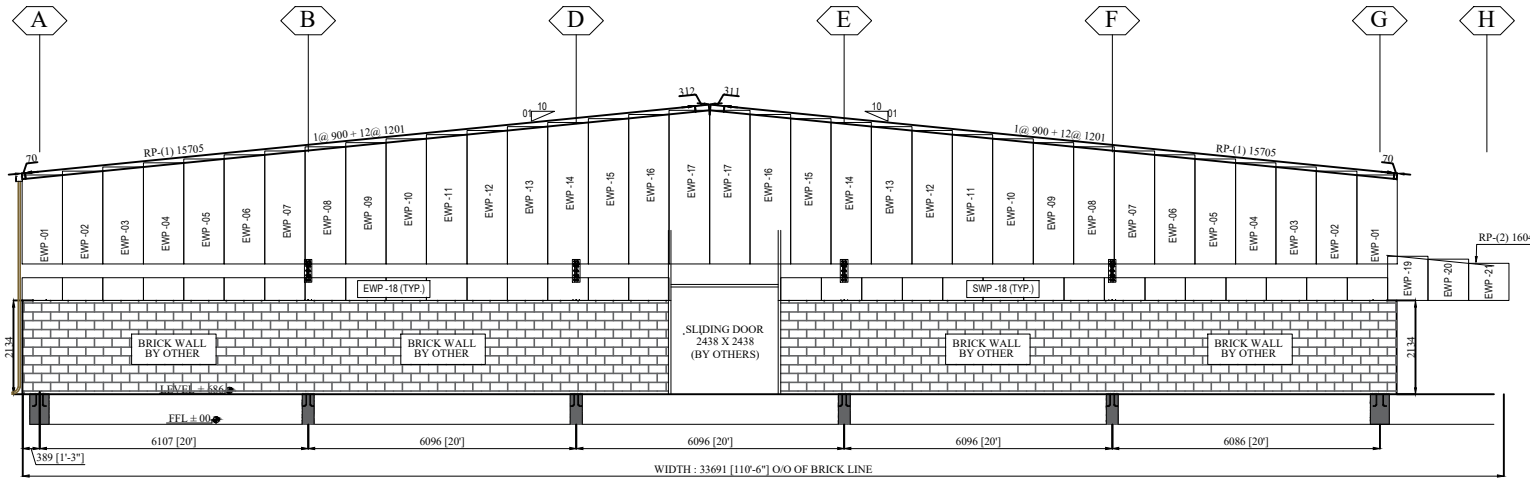

END WALL PANELS

DESCRIPTIONS	PART	LENGTH (MM)	WIDTH (MM)	QUANTITY
END WALL PANEL	EWP-01	2,023	920	2
END WALL PANEL	EWP-02	2,115	920	2
END WALL PANEL	EWP-03	2,207	920	2
END WALL PANEL	EWP-04	2,299	920	2
END WALL PANEL	EWP-05	2,391	920	2
END WALL PANEL	EWP-06	2,482	920	2
END WALL PANEL	EWP-07	2,574	920	2
END WALL PANEL	EWP-08	2,666	920	2
END WALL PANEL	EWP-09	2,758	920	2
END WALL PANEL	EWP-10	2,850	920	2
END WALL PANEL	EWP-11	2,942	920	2
END WALL PANEL	EWP-12	3,034	920	2
END WALL PANEL	EWP-13	3,126	920	2
END WALL PANEL	EWP-14	3,218	920	2
END WALL PANEL	EWP-15	3,310	920	2
END WALL PANEL	EWP-16	3,402	920	2
END WALL PANEL	EWP-17	3,494	920	2
END WALL PANEL	EWP-18	519	920	31
END WALL PANEL	EWP-19	1,006	920	1
END WALL PANEL	EWP-20	936	920	1
END WALL PANEL	EWP-21	844	920	1

REV	DATE	DESCRIPTION	DRAWN BY	CHK BY	APR BY
01	10-Jun-24	ISSUED FOR APPROVAL	MA	KAS	NAS

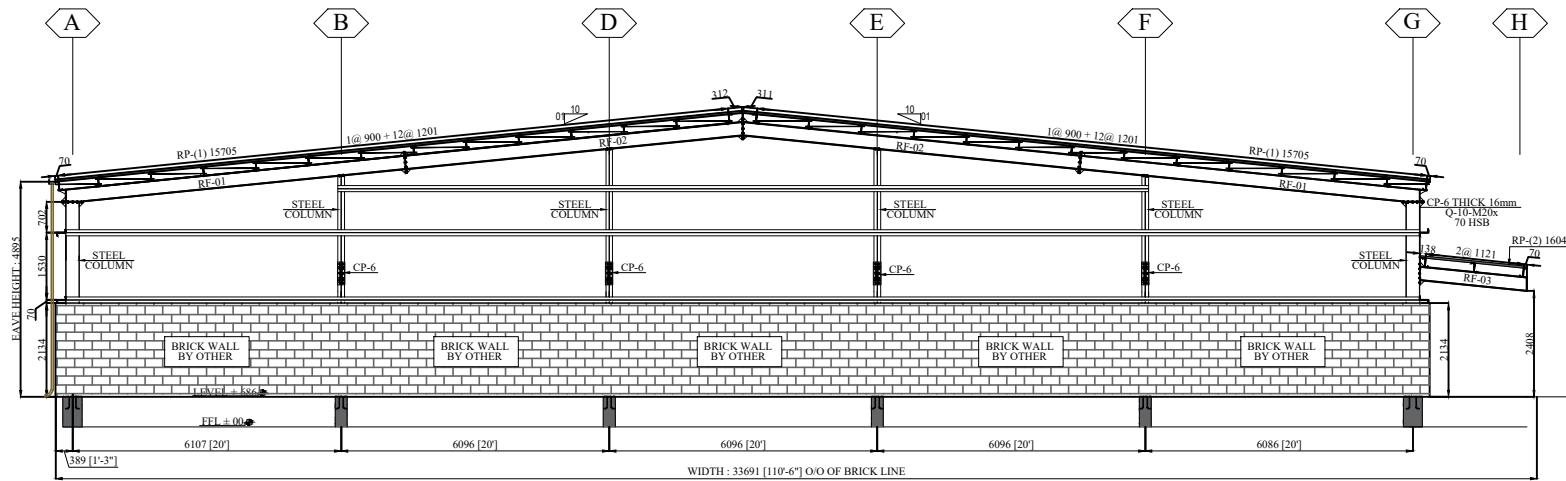

MAIMAAR STEEL Pvt.Ltd
 238, Raiwind Road, Thokar Niaz Baig, Lahore, Pakistan
 E-mail: nasir.abbas@maimaargroup.com
 E-mail: maimaar.steel@gmail.com
 Website: www.maimaargroup.com
 E-mail: info@maimaargroup.com
 Mob-I : +(92-300) 807 4017, +(92-333) 807 1115

JOB NO./QUOTE NO.	MSPL-135	BUILDING #	01
PROJECT NAME	DRY FRUITS PROCESSING DERA ISMAIL KHAN		
CUSTOMER	45 ENGINEER DIVISION		
JOB SITE LOCATION	DERA ISMAIL KHAN		

END WALL FRAMING & SHEETING @ GRID 07

DWG NO.

E07

END WALL FRAMING & SHEETING @ GRID 07

FOR APPROVAL :

IN ORDER TO SCHEDULE THIS PROJECT
 IN AN EFFICIENT MANNER, KINDLY
 RETURN THESE DRAWINGS WITH YOUR
 ANY CHANGES MADE AFTER THE
 COMMENTS MARKED IN RED

- ☐ " APPROVED AS IS "
- ☐ " APPROVED AS NOTED "
- ☐ " RESUBMIT AS NOTED "

APPROVAL OF THESE DRAWINGS MAY
 DELAY THE FABRICATION SCHEDULE AND
 SUBSEQUENTLY THE DELIVERY OF THE
 BUILDING.

APPROVE : _____

SIGNATURE : _____

DATE : _____

PLEASE TICK MARK ONLY ONE OF THE FOLLOWING