



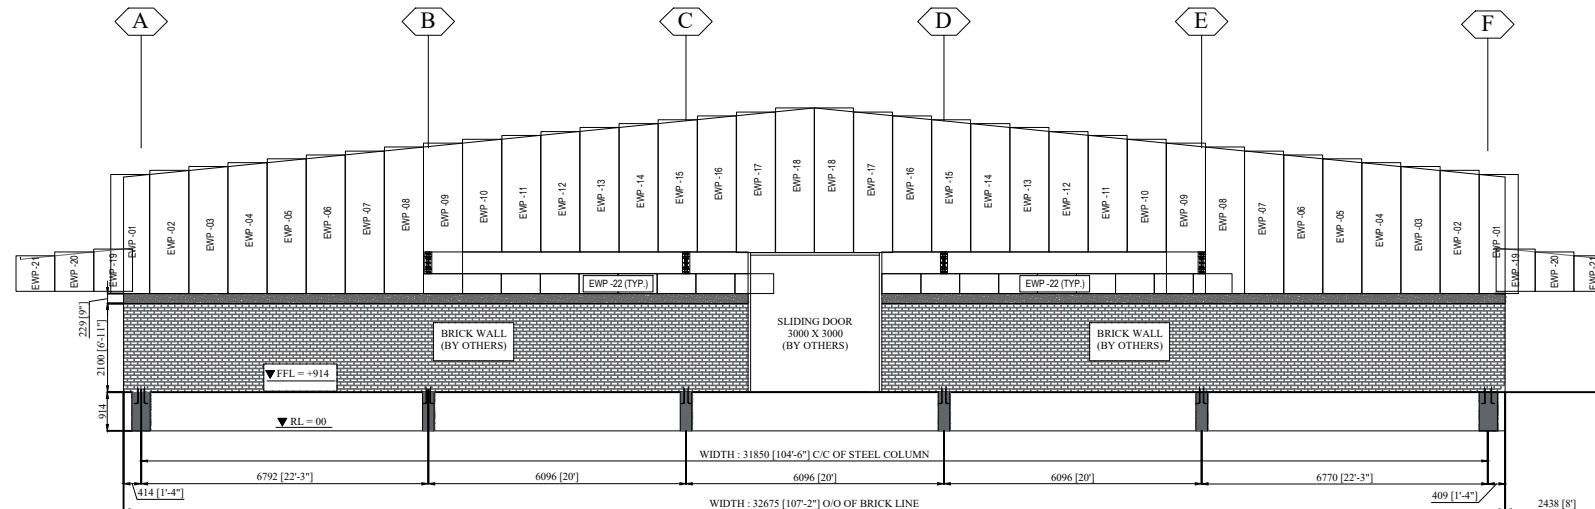

## END WALL PANELS

| DESCRIPTIONS   | PART   | LENGTH (MM) | WIDTH (MM) | QUANTITY |
|----------------|--------|-------------|------------|----------|
| END WALL PANEL | EWP-01 | 2,822       | 920        | 2        |
| END WALL PANEL | EWP-02 | 2,914       | 920        | 2        |
| END WALL PANEL | EWP-03 | 3,006       | 920        | 2        |
| END WALL PANEL | EWP-04 | 3,099       | 920        | 2        |
| END WALL PANEL | EWP-05 | 3,191       | 920        | 2        |
| END WALL PANEL | EWP-06 | 3,283       | 920        | 2        |
| END WALL PANEL | EWP-07 | 3,376       | 920        | 2        |
| END WALL PANEL | EWP-08 | 3,468       | 920        | 2        |
| END WALL PANEL | EWP-09 | 3,560       | 920        | 2        |
| END WALL PANEL | EWP-10 | 2,668       | 920        | 2        |
| END WALL PANEL | EWP-11 | 2,760       | 920        | 2        |
| END WALL PANEL | EWP-12 | 2,852       | 920        | 2        |
| END WALL PANEL | EWP-13 | 2,945       | 920        | 2        |
| END WALL PANEL | EWP-14 | 3,037       | 920        | 2        |
| END WALL PANEL | EWP-15 | 3,129       | 920        | 2        |
| END WALL PANEL | EWP-16 | 3,222       | 920        | 2        |
| END WALL PANEL | EWP-17 | 3,325       | 920        | 2        |
| END WALL PANEL | EWP-18 | 3,418       | 920        | 2        |
| END WALL PANEL | EWP-19 | 1,006       | 920        | 1        |
| END WALL PANEL | EWP-20 | 936         | 920        | 1        |
| END WALL PANEL | EWP-21 | 844         | 920        | 1        |
| END WALL PANEL | EWP-22 | 473         | 920        | 18       |

| REV | DATE      | DESCRIPTION         | DRAWN BY | CHK BY | APR BY |
|-----|-----------|---------------------|----------|--------|--------|
| 03  | 20-Jun-24 | ISSUED FOR APPROVAL | IU       | KAS    | NAS    |

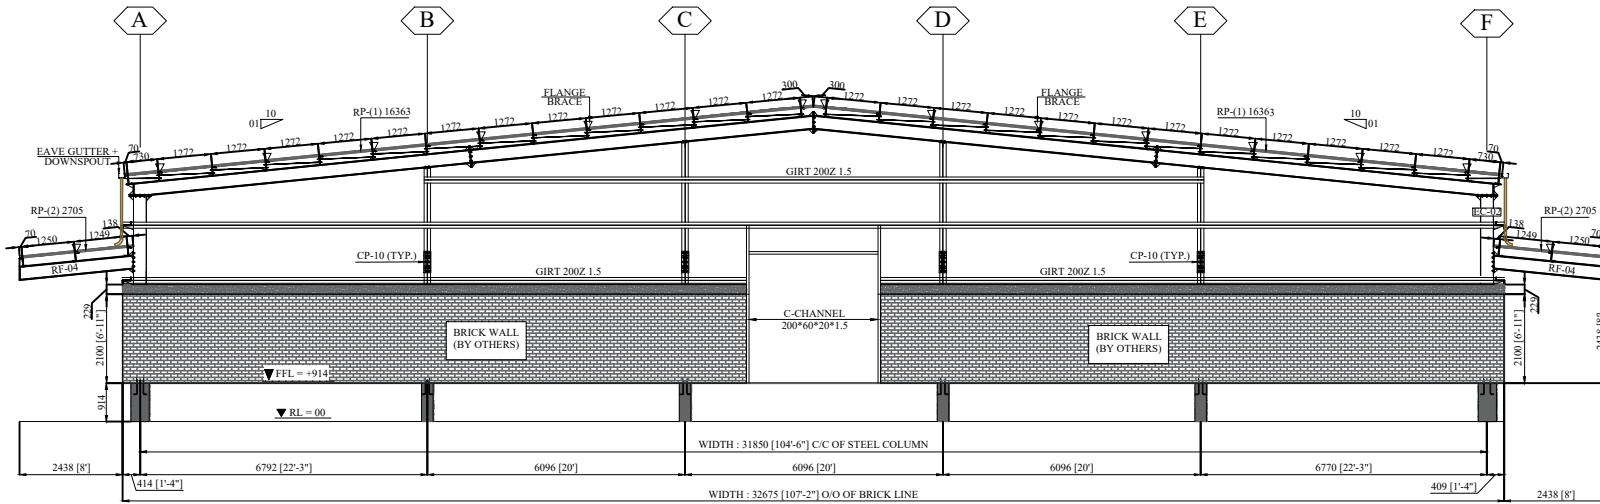

MAIMAAR STEEL Pvt.Ltd  
 238, Raiwind Road, Thokar Niaz Baig, Lahore, Pakistan  
 E-mail: nasir.abbas@maimaargroup.com  
 E-mail: maimaar.steel@gmail.com  
 Website: www.maimaargroup.com  
 E-mail: info@maimaargroup.com  
 Mob-I : +(92-300) 807 4017 ,+(92-333) 807 1115

|                   |                                        |            |    |
|-------------------|----------------------------------------|------------|----|
| JOB NO./QUOTE NO. | MSPL-135                               | BUILDING # | 01 |
| PROJECT NAME      | DRY FRUITS PROCESSING DERA ISMAIL KHAN |            |    |
| CUSTOMER          | 45 ENGINEER DIVISION                   |            |    |
| JOB SITE LOCATION | DERA ISMAIL KHAN                       |            |    |

## END WALL FRAMING & SHEETING @ GRID 07

DWG NO.  
E09

## END WALL FRAMING & SHEETING @ GRID 07

### FOR APPROVAL :

IN ORDER TO SCHEDULE THIS PROJECT IN AN EFFICIENT MANNER , KINDLY RETURN THESE DRAWINGS WITH YOUR ANY CHANGES MADE AFTER THE COMMENTS MARKED IN RED

APPROVAL OF THESE DRAWINGS MAY DELAY THE FABRICATION SCHEDULE AND SUBSEQUENTLY THE DELIVERY OF THE BUILDING.

PLEASE TICK MARK ONLY ONE OF THE FOLLOWING

- ☐ " APPROVED AS IS "
- ☐ " APPROVED AS NOTED "
- ☐ " RESUBMIT AS NOTED "

APPROVE : \_\_\_\_\_

SIGNATURE: \_\_\_\_\_

DATE : \_\_\_\_\_