


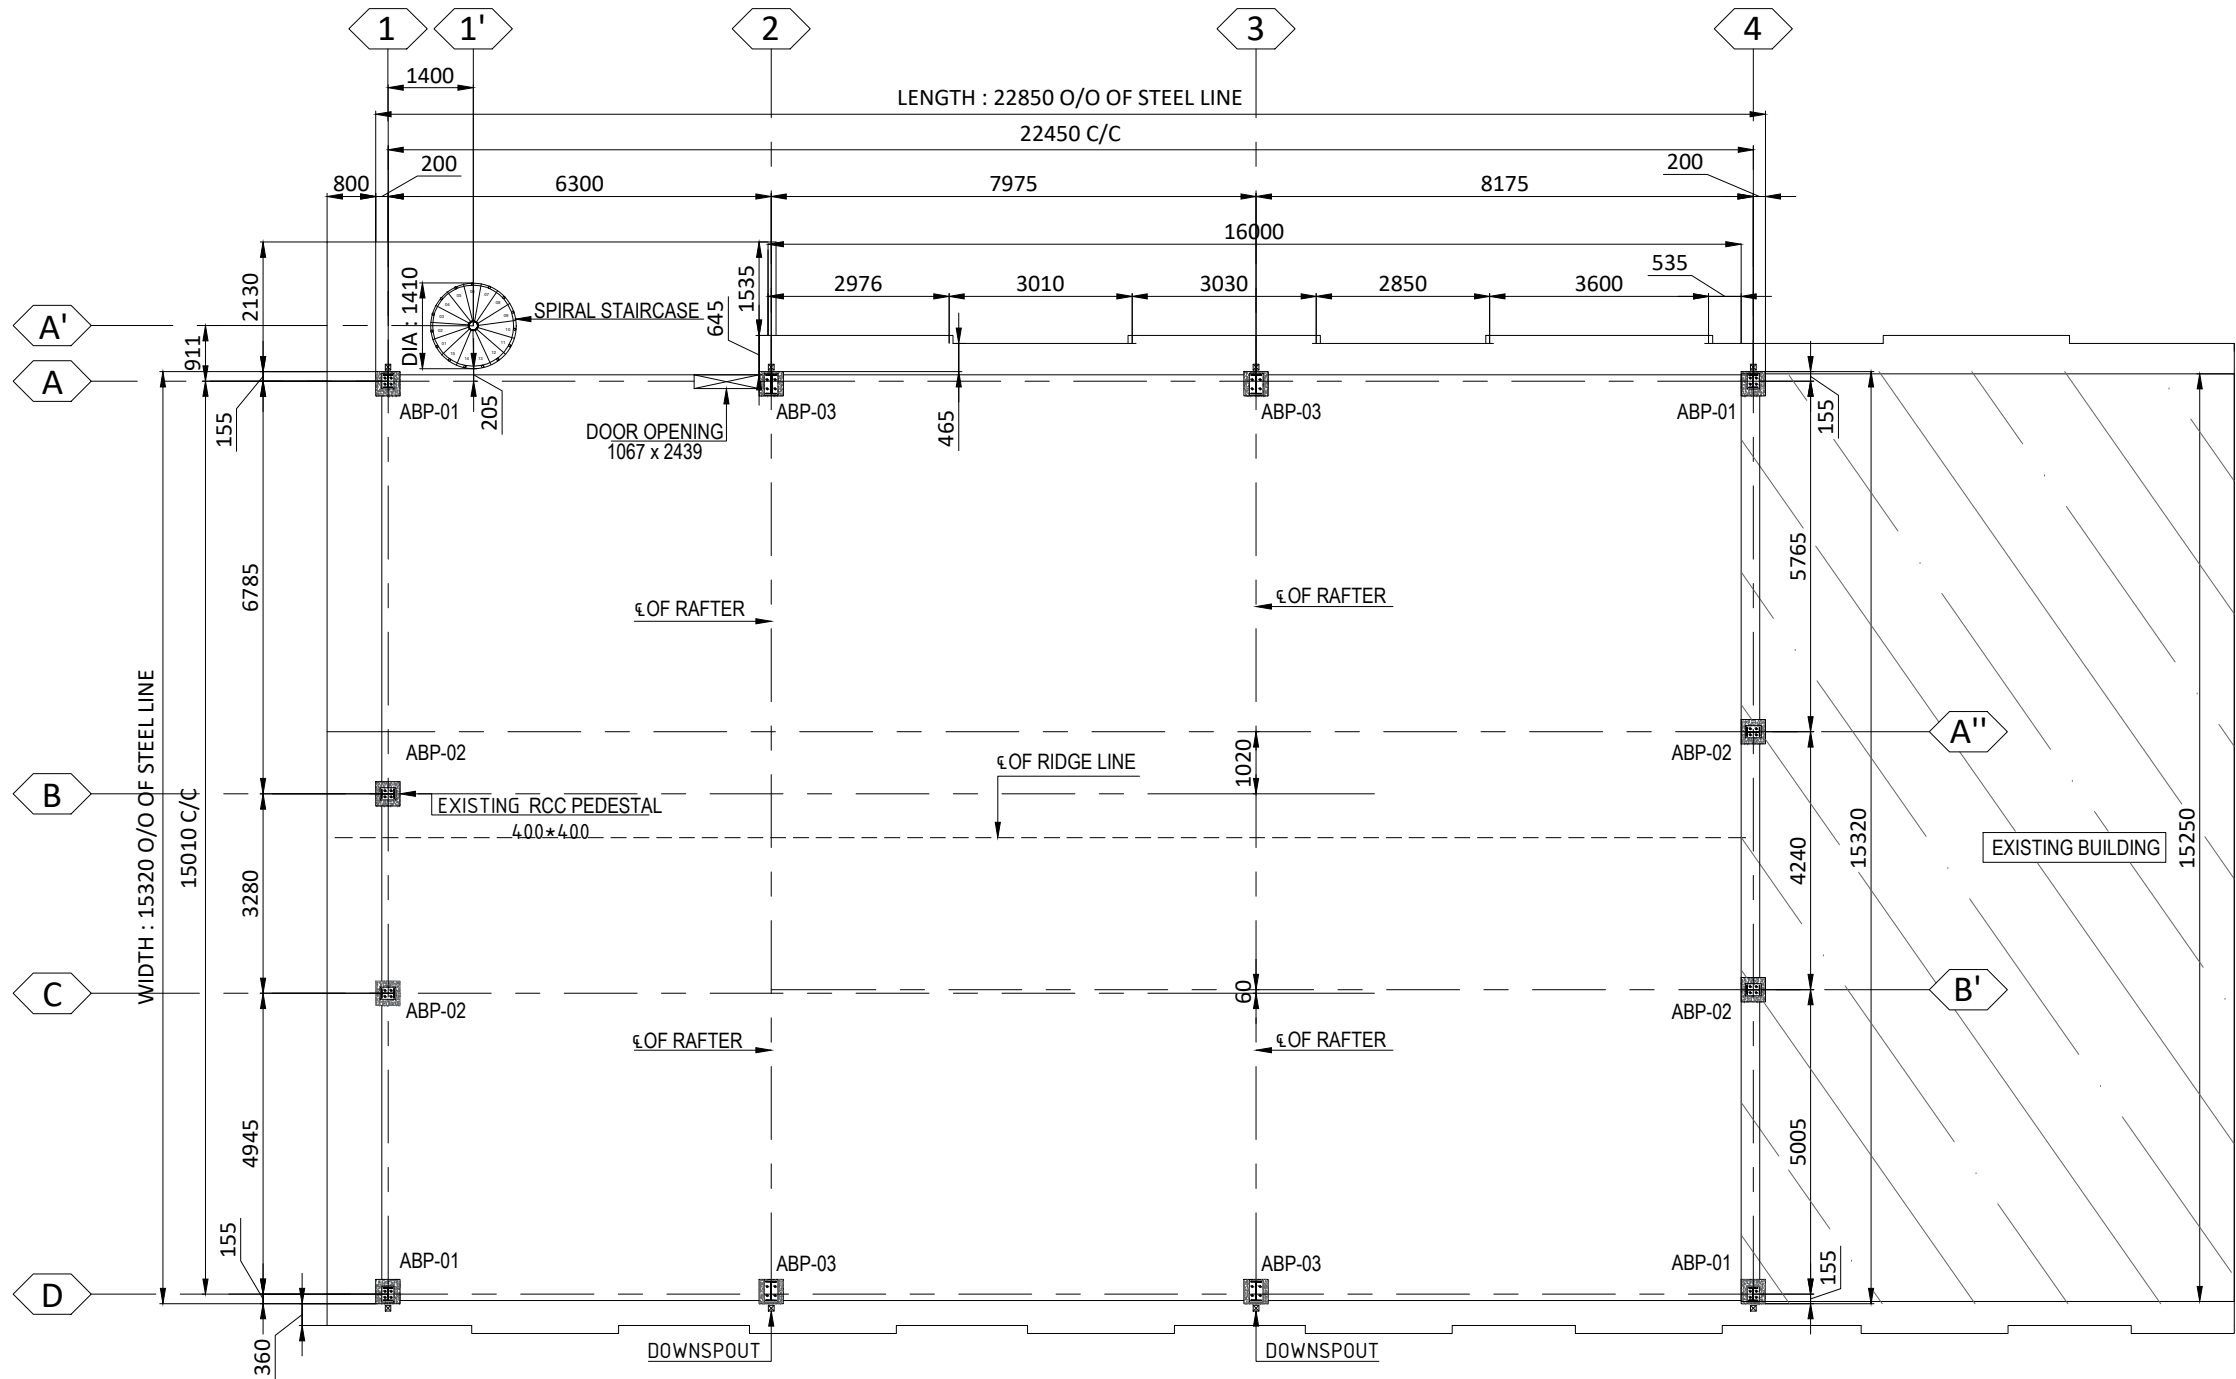

COLUMN LAYOUT PLAN

FOR APPROVAL :

IN ORDER TO SCHEDULE THIS PROJECT IN AN EFFICIENT MANNER , KINDLY RETURN THESE DRAWINGS WITH YOUR COMMENTS MARKED IN RED

APPROVAL OF THESE DRAWINGS MAY DELAY THE FABRICATION SCHEDULE AND SUBSEQUENTLY THE DELIVERY OF THE BUILDING.

PLEASE TICK MARK ONLY ONE OF THE FOLLOWING

☐ " APPROVED AS IS "

☐ " APPROVED AS NOTED"

☐ " RESUBMIT AS NOTED "

APPROVE : _____

SIGNATURE: _____

DATE : _____

BUILDING DESIGN LOADS:

☐ LIVE LOAD ON ROOF = 0.41 KN/SQ.M

☐ LIVE LOAD ON FRAME = 0.57 KN/SQ.M

☐ COLLATERAL LOAD = 0.16 KN/SQ.M

☐ RAINFALL INTENSITY FOR DESIGN OF GUTTERS & DOWNSPOUT = 0.16 KN/SQ.M

☐ WIND SPEED = 135 KM/H

☐ EXPOSURE = B

APPROVE : _____

SIGNATURE: _____

DATE : _____

00	20-12-23	ISSUED FOR APPROVAL	I.U	T.K	YEH
REV.	DATE	DESCRIPTION	DRWN BY	CHK BY	APR BY



MAIMAAR STEEL Pvt.Ltd
238, Raiwind Road, Thokar Niaz Baig ,LAHORE, Pakistan
E-mail: nasir.abbas@maimaargroup.com
E-mail: maimaar.steel@gmail.com
Website: www.maimaargroup.com
E-mail: nasir.abbas@maimaargroup.com
Mob-1 : +(92-300) 807 4017 ,+(92-333) 807 1115

JOB NO./QUOTE NO.	MSPL-112-23	BUILDING #	01
PROJECT NAME	ROOF SHED		
CUSTOMER	SKI BRO		
JOBSITE LOCATION	SIALKOT		

COLUMN LAYOUT PLAN