


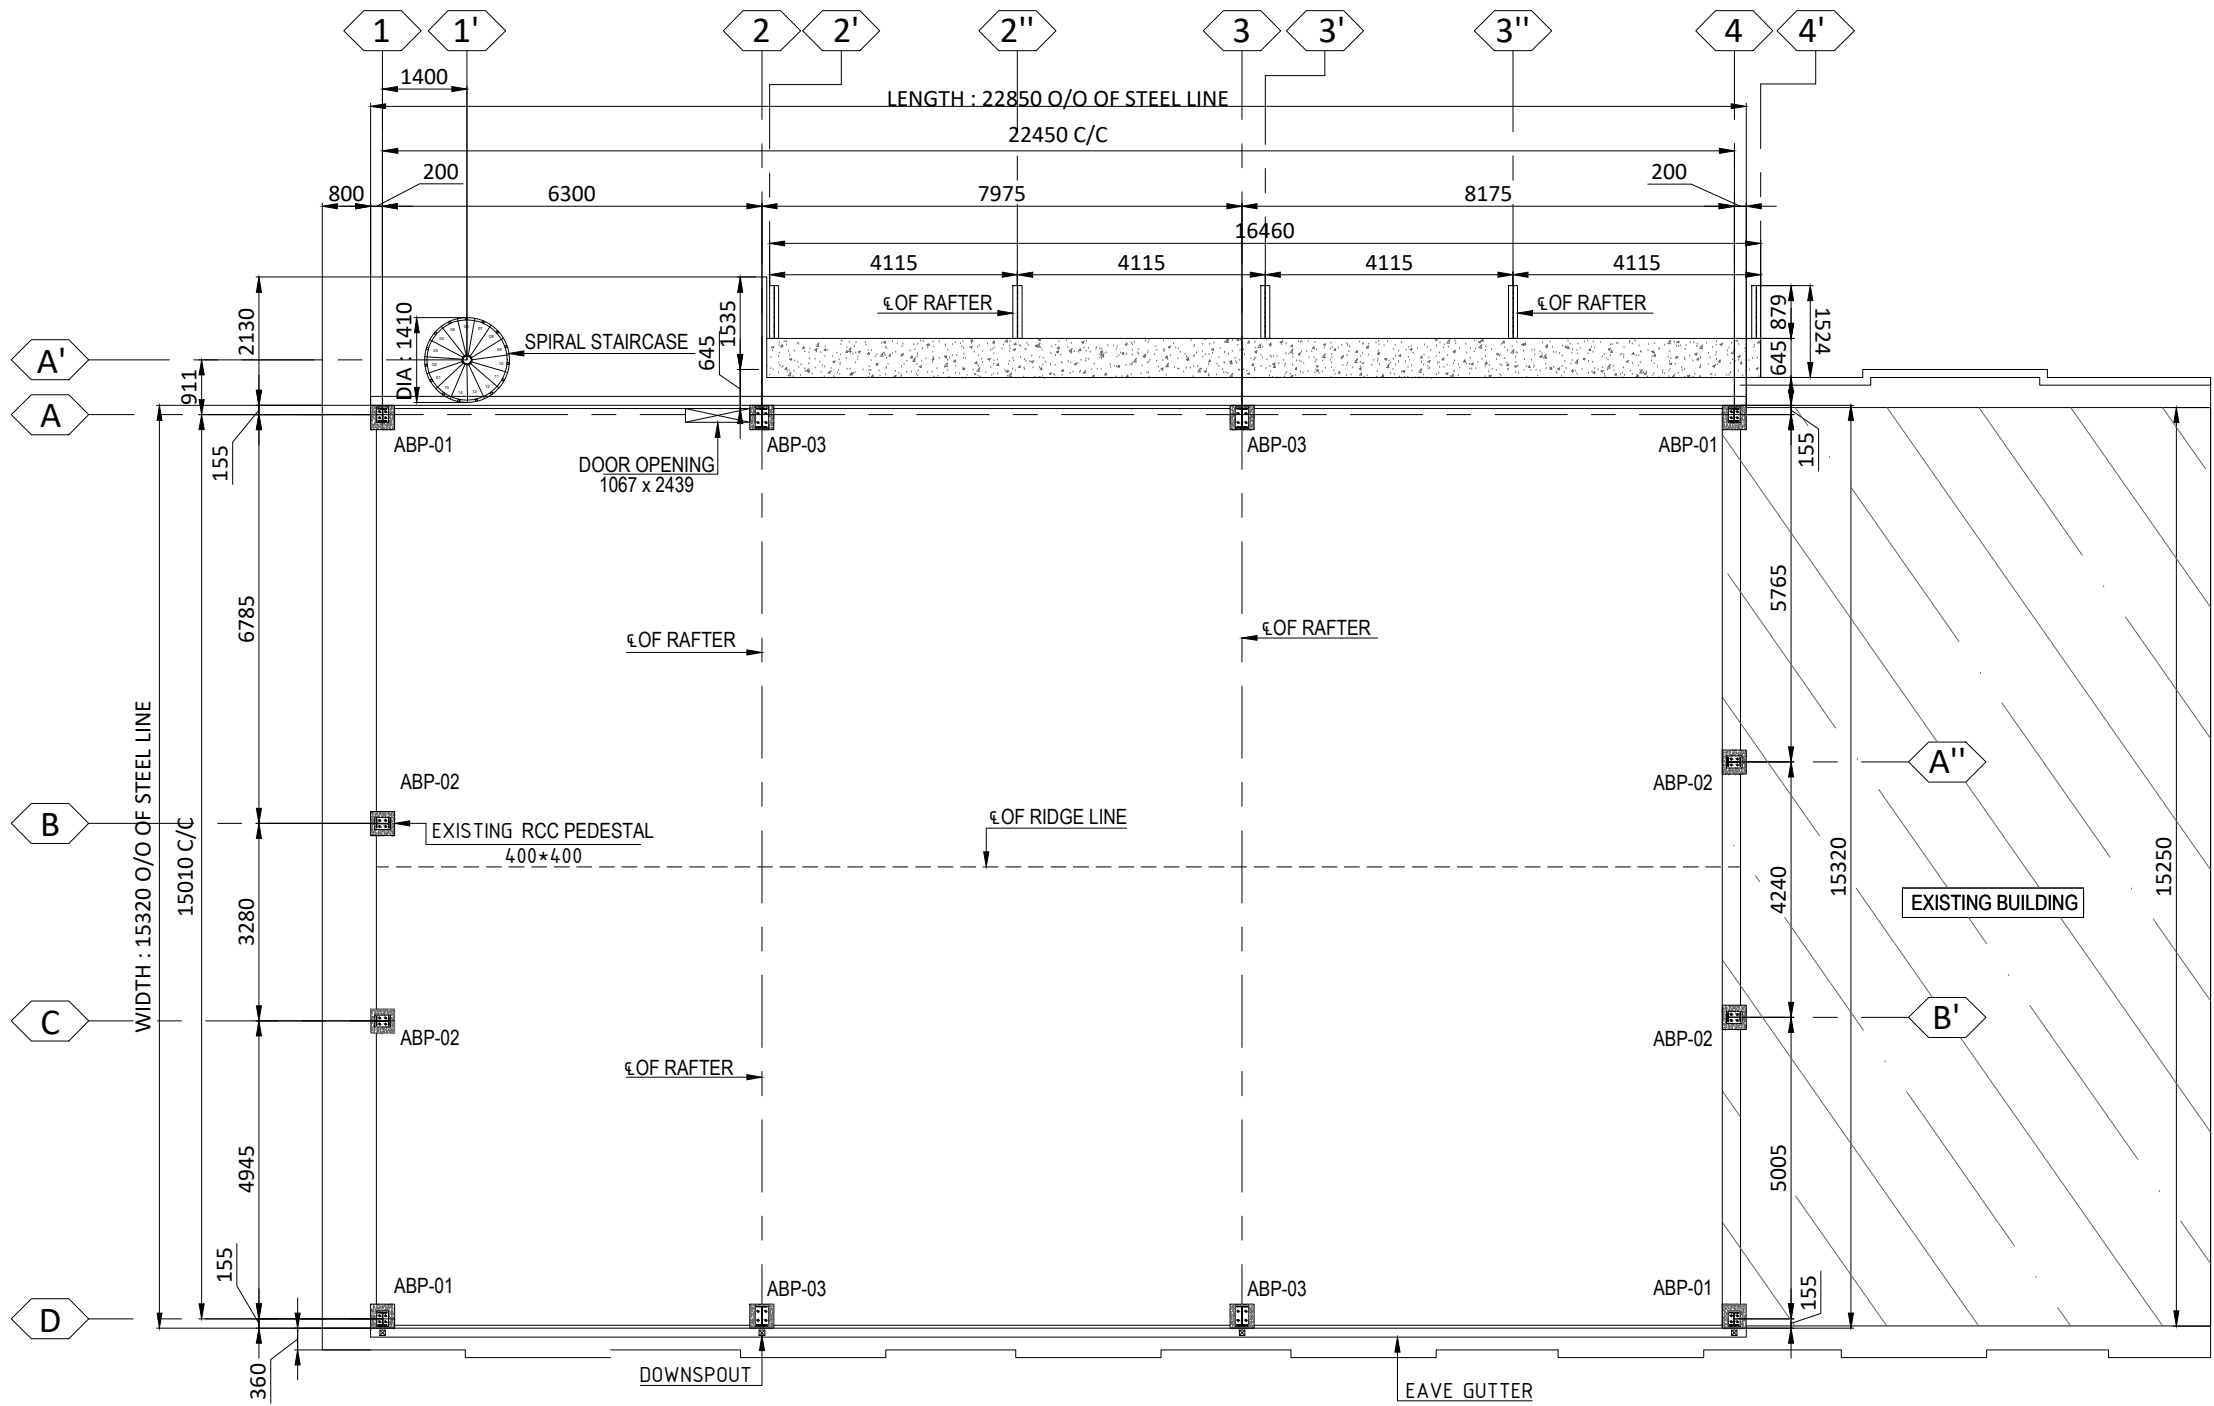

PLATFORM RAFTER LAYOUT PLAN

FOR APPROVAL :

IN ORDER TO SCHEDULE THIS PROJECT IN AN EFFICIENT MANNER , KINDLY RETURN THESE DRAWINGS WITH YOUR COMMENTS MARKED IN RED APPROVAL OF THESE DRAWINGS MAY DELAY THE FABRICATION SCHEDULE AND SUBSEQUENTLY THE DELIVERY OF THE BUILDING. PLEASE TICK MARK ONLY ONE OF THE FOLLOWING

☐ " APPROVED AS IS "

☐ " APPROVED AS NOTED "

☐ " RESUBMIT AS NOTED "

APPROVE : \_\_\_\_\_

SIGNATURE: \_\_\_\_\_

DATE : \_\_\_\_\_

BUILDING DESIGN LOADS:

☐ LIVE LOAD ON ROOF = 0.41 KN/SQ.M

☐ LIVE LOAD ON FRAME = 0.57 KN/SQ.M

☐ COLLATERAL LOAD = 0.16 KN/SQ.M

☐ RAINFALL INTENSITY FOR DESIGN OF GUTTERS & DOWNSPOUT = 0.16 KN/SQ.M

☐ WIND SPEED = 135 KM/H

☐ EXPOSURE = B

APPROVE : \_\_\_\_\_

SIGNATURE: \_\_\_\_\_

DATE : \_\_\_\_\_

|      |          |                     |         |        |        |
|------|----------|---------------------|---------|--------|--------|
| 00   | 20-12-23 | ISSUED FOR APPROVAL | I.U     | T.K    | YEH    |
| REV. | DATE     | DESCRIPTION         | DRWN BY | CHK BY | APR BY |



MAIMAAR STEEL Pvt.Ltd  
238, Raiwind Road, Thokar Niaz Baig ,LAHORE, Pakistan  
E-mail: nasir.abbas@maimaargroup.com  
E-mail: maimaar.steel@gmail.com  
Website: www.maimaargroup.com  
E-mail: nasir.abbas@maimaargroup.com  
Mob-1 : +(92-300) 807 4017 ,+(92-333) 807 1115

|                   |             |            |    |
|-------------------|-------------|------------|----|
| JOB NO./QUOTE NO. | MSPL-112-23 | BUILDING # | 01 |
| PROJECT NAME      | ROOF SHED   |            |    |
| CUSTOMER          | SKI BRO     |            |    |
| JOBSITE LOCATION  | SIALKOT     |            |    |

PLATE FORM RAFTER LAYOUT PLAN

DWG. NO.  
07