

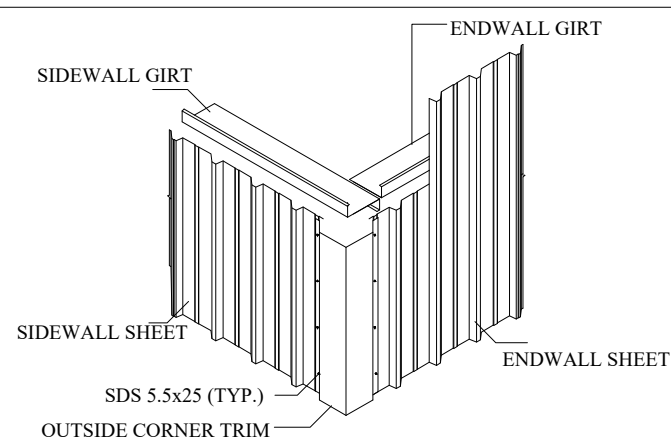


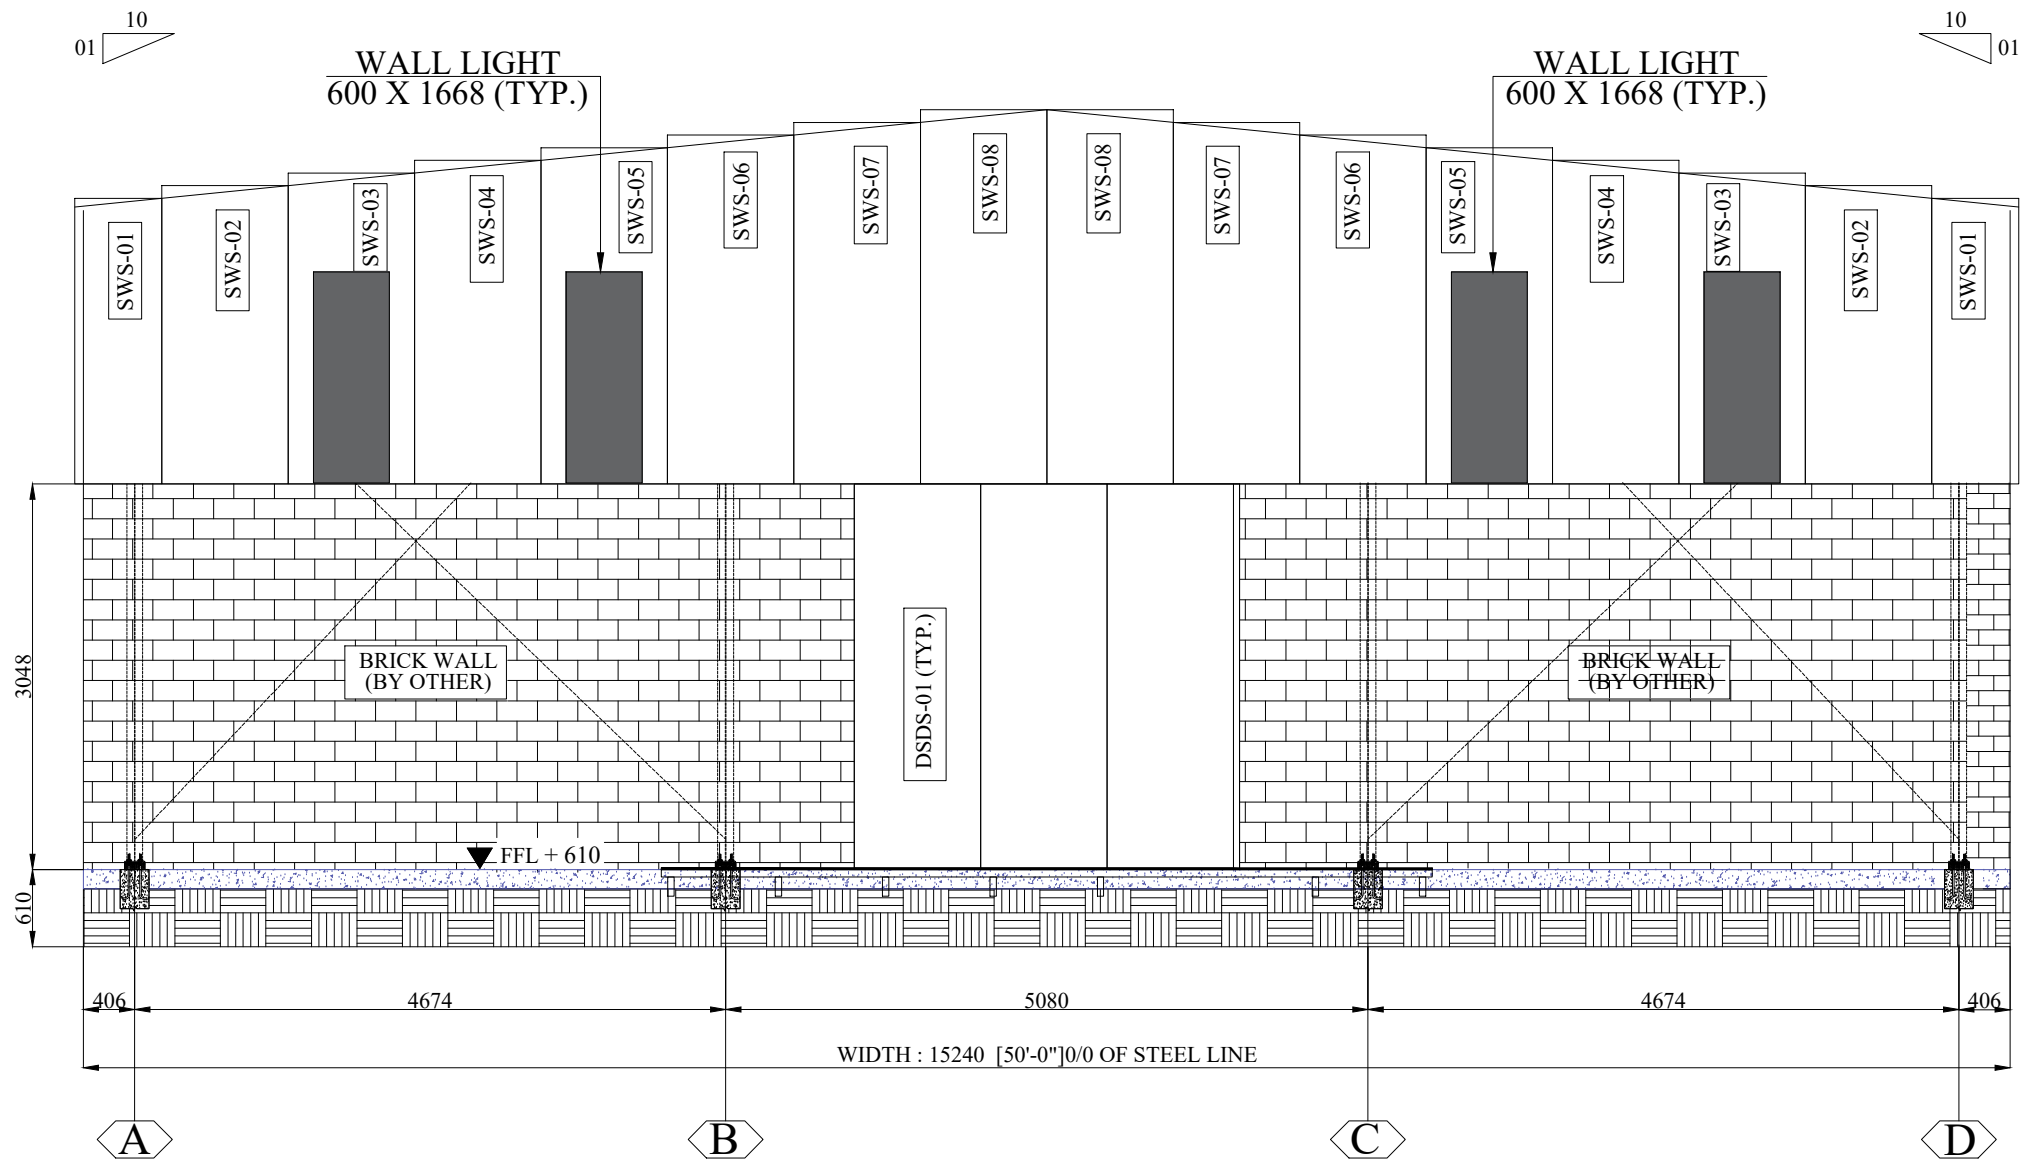

CORNER TRIM DETAIL (3-D)

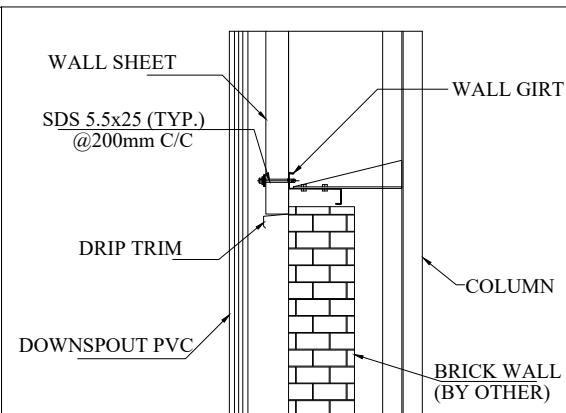

DRIP TRIM DETAIL

END WALL SHEETING @ GL- 1 (WALL CLADDING 0.5MM PPGL SHEETING)				
DESCRIPTIONS	PART	LENGTH (MM)	WIDTH (MM)	QUANTITY
END WALL SHEETING	EWS-01	2,260	1,000	2
END WALL SHEETING	EWS-02	2,360	1,000	2
END WALL SHEETING	EWS-03	2,460	1,000	2
END WALL SHEETING	EWS-04	2,560	1,000	2
END WALL SHEETING	EWS-05	2,660	1,000	2
END WALL SHEETING	EWS-06	2,760	1,000	2
END WALL SHEETING	EWS-07	2,860	1,000	2
END WALL SHEETING	EWS-08	2,960	1,000	2
DOUBLE SLIDING DOOR SHEETING	DSDS-01	3,048	1,000	4
00		DESCRIPTION		DRAWN BY
ISSUED FOR APPROVAL		IUMR		CHK BY
JOB NO .		MSPL-242		DATE
CLIENT		STARCH PACK		DWG NO.
		01		15-04-26
				10

S.NO	Description	Rev.	DATE
0.			
1.			
2.			



MAIMAAR STEEL Pvt.Ltd
 238, Raiwind Road, Thokar Niaz Baig, Lahore, Pakistan
 E-mail: nasir.abbas@maimaargroup.com
 E-mail: maimaar.steel@gmail.com
 Website: www.maimaargroup.com
 E-mail: info@maimaargroup.com
 Mob-1 : +(92-300) 807 4017 ,+(92-333) 807 1115

Drawing Title	
END WALL SHEETING @ GL. 01	
LOCATION	KASUR