

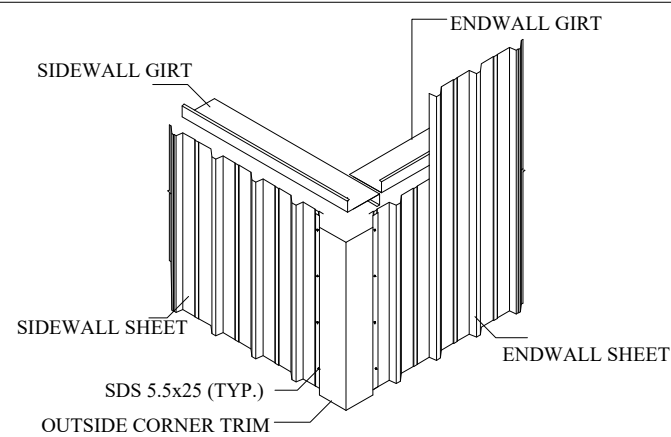


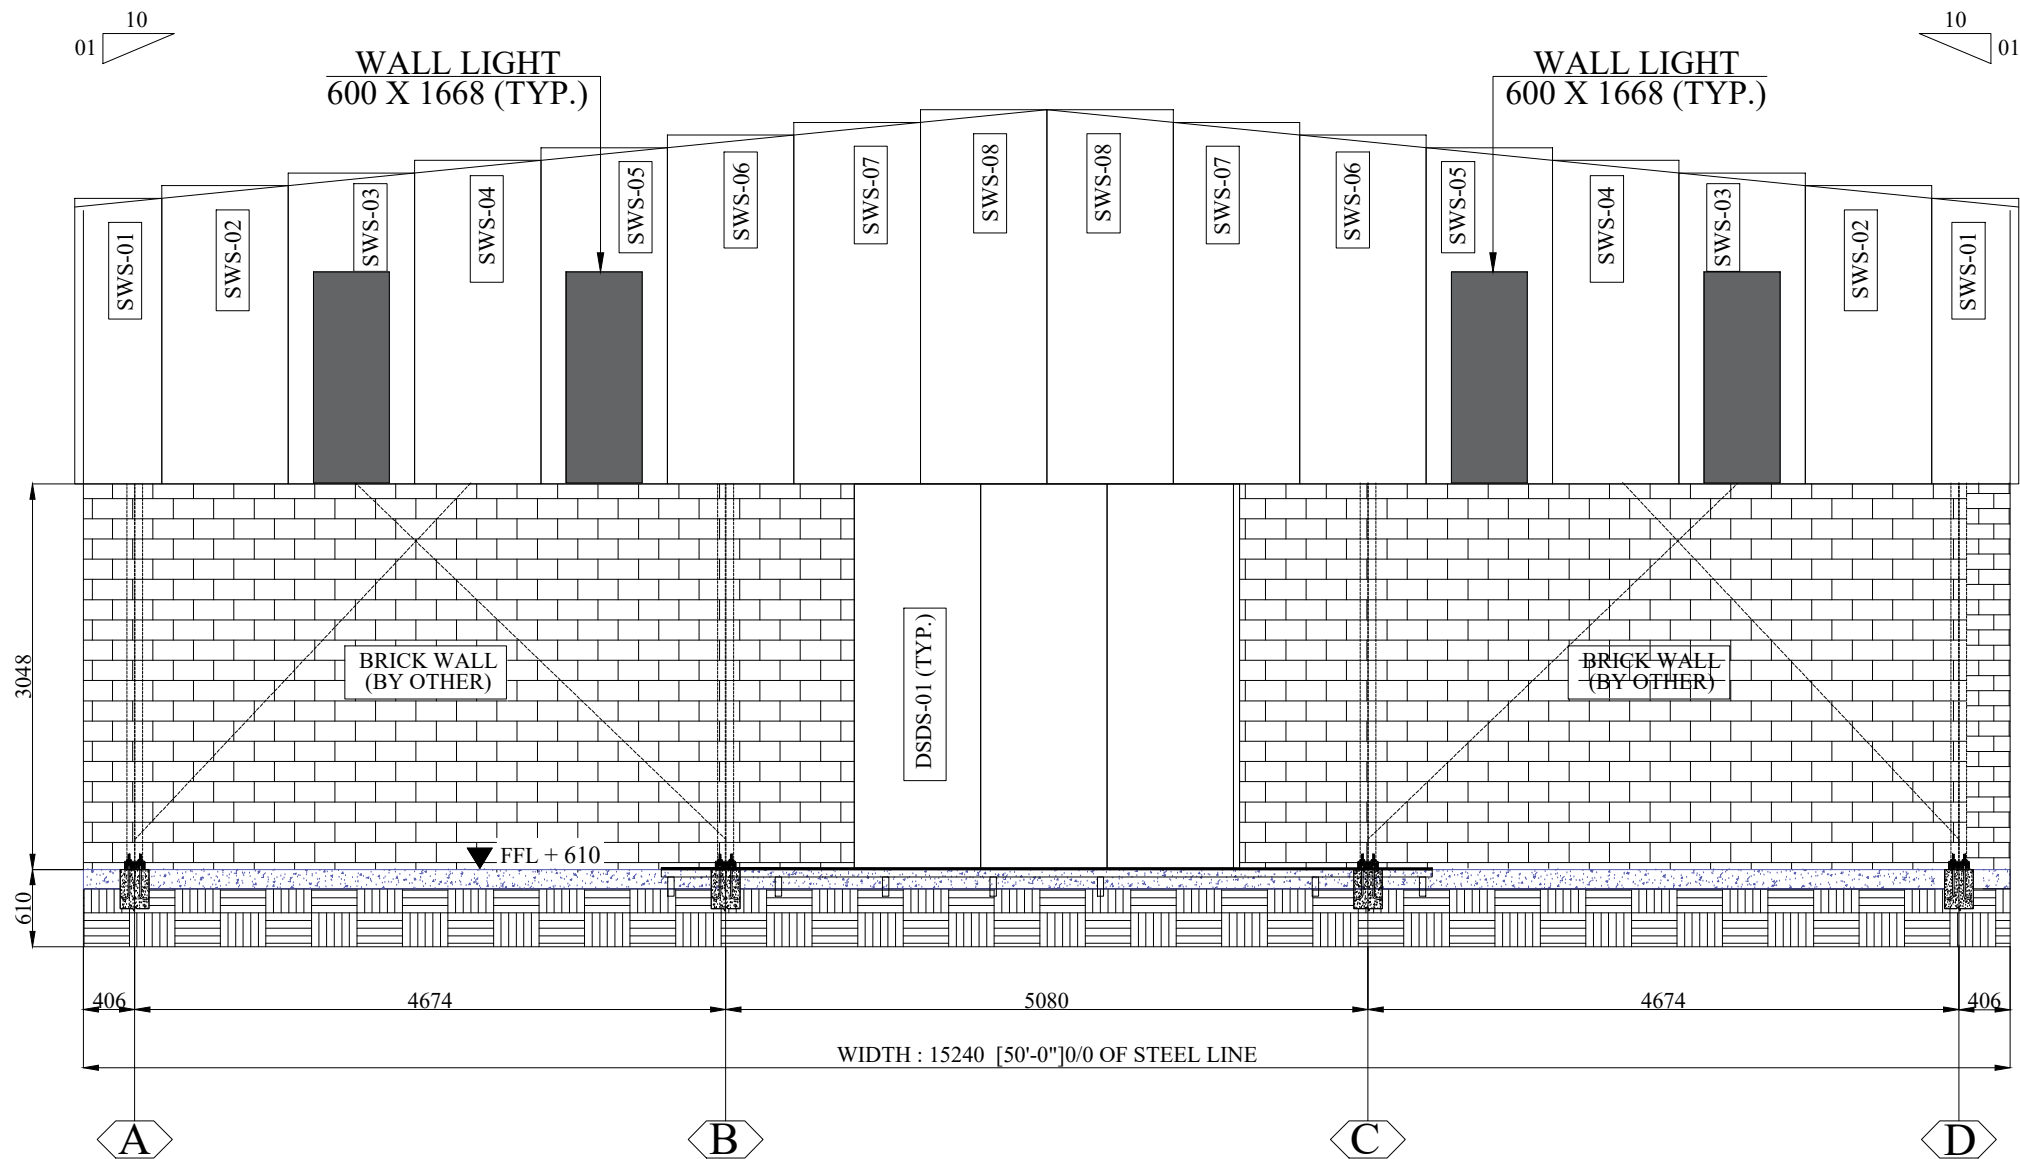

CORNER TRIM DETAIL (3-D)

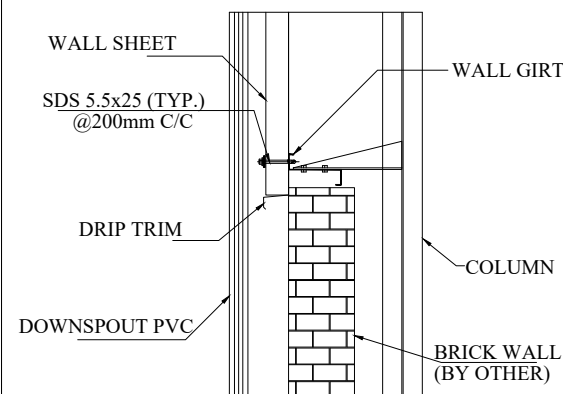

DRIP TRIM DETAIL

END WALL SHEETING @ GL- 1
(WALL CLADDING 0.5MM PPGL SHEETING)

DESCRIPTIONS	PART	LENGTH (MM)	WIDTH (MM)	QUANTITY
END WALL SHEETING	EWS-01	2,260	1,000	2
END WALL SHEETING	EWS-02	2,360	1,000	2
END WALL SHEETING	EWS-03	2,460	1,000	2
END WALL SHEETING	EWS-04	2,560	1,000	2
END WALL SHEETING	EWS-05	2,660	1,000	2
END WALL SHEETING	EWS-06	2,760	1,000	2
END WALL SHEETING	EWS-07	2,860	1,000	2
END WALL SHEETING	EWS-08	2,960	1,000	2
DOUBLE SLIDING DOOR SHEETING	DSDS-01	3,048	1,000	4

S.NO	Description	Rev.	DATE
0.			
1.			
2.			



MAIMAAR STEEL Pvt.Ltd
238, Raiwind Road, Thokar Niaz Baig, Lahore, Pakistan
E-mail: nasir.abbas@maimaargroup.com
E-mail: maimaar.steel@gmail.com
Website: www.maimaargroup.com
E-mail: info@maimaargroup.com
Mob-1 : +(92-300) 807 4017 ,+(92-333) 807 1115

Drawing Title	
END WALL SHEETING @ GL. 01	
LOCATION	KASUR

DESCRIPTION	DRAWN BY	CHK BY	APR BY
00 ISSUED FOR APPROVAL	IUMR	S.SAQ	S.SAQ
JOB NO . MSPL-242	BUILDING #	DATE	DWG NO.
CLIENT STARCH PACK	01	15-04-26	10